



- PROPOSED POWER CABLE
- PROPOSED POWER CABLE
- PROPOSED GROUNDING C
- PROPOSED HYBRID CABLE
- PROPOSED OPTICAL CABL
- COAXIAL CABLE
- EXISTING FEEDER
- EXISTING JUMPER
- PROPOSED JUMPER
- PROPOSED CABINET
- DISMANTLE EQUIPMENT
- EXISTING EQUIPMENT

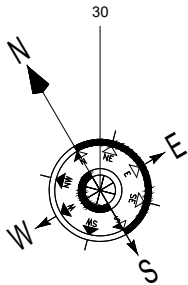

2T2R L900_(10)+4T4R L1800_(30)+4T4R L2100_(25)+HOS2

- Existing 1pcs Antenna IOH APE4517R2
- Dismantle 2pcs Antenna IOH APE4517R2
- Proposed 2pcs Antenna IOH AMB4519R5v09
- Proposed 4pcs RRU5516 18000-2100
- Dismantle 4pcs RRU3959a (1800M)
- Dismantle 4pcs RRU3959a (2100M)
- Existing 2pcsRRU3959a (1800M)
- Existing 2pcsRRU3959a (2100M)
- Existing 1pcsRRU5910 (900M)
- Existing 1pcsRRU5909 (900M)

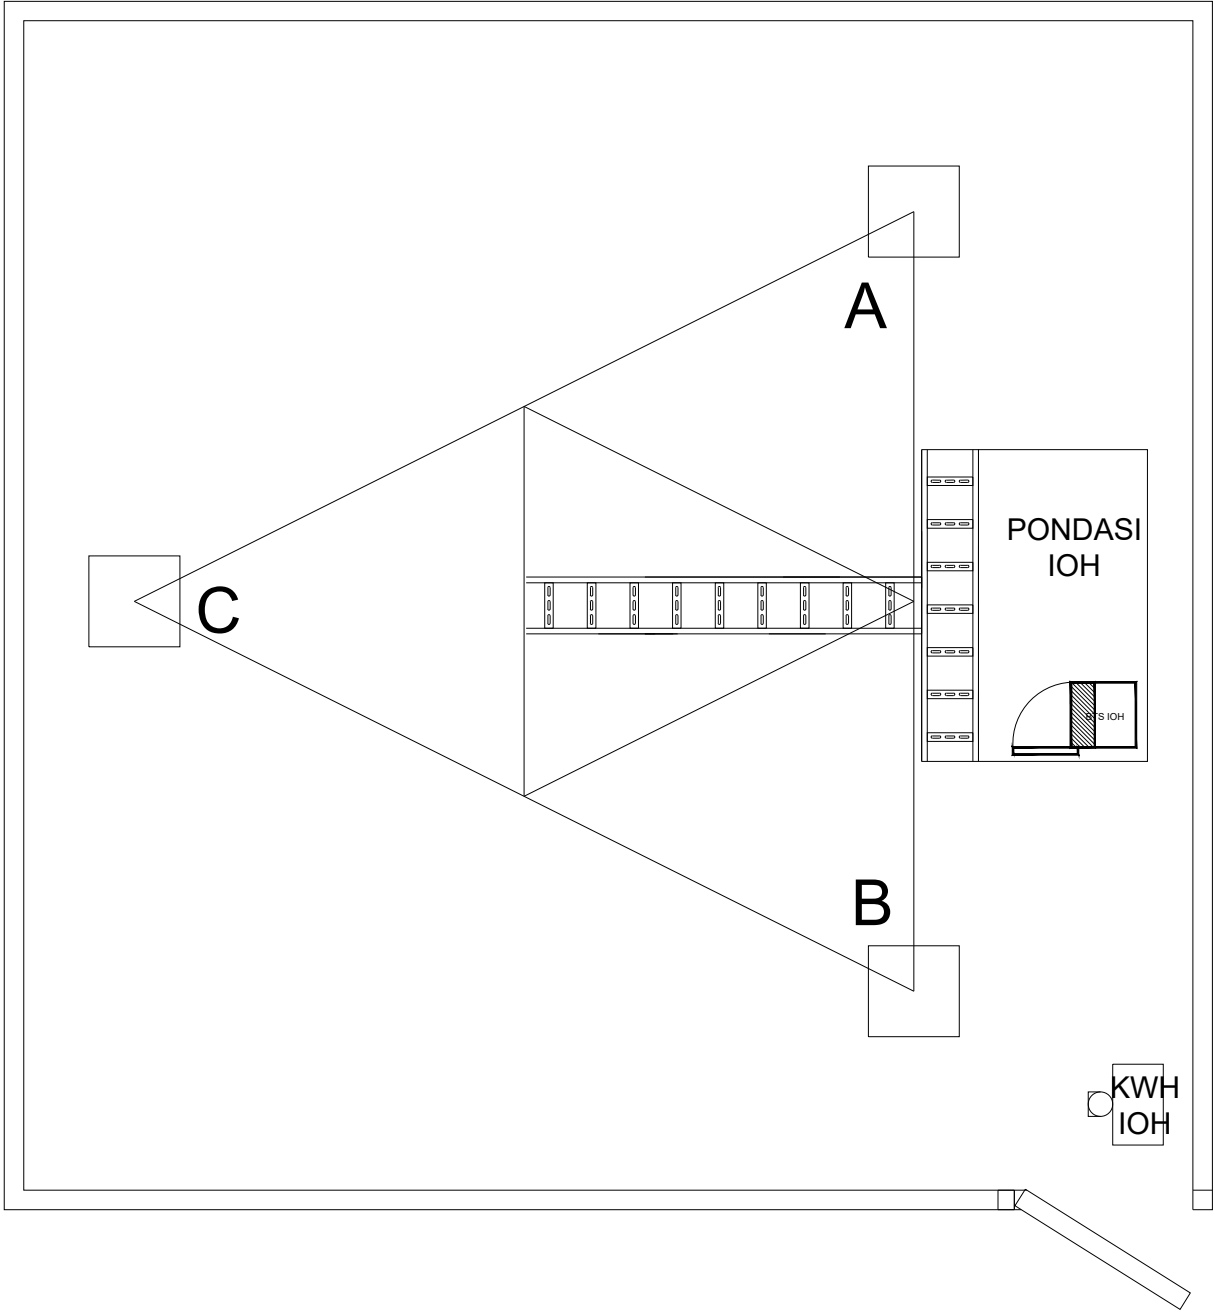

REMARKS

1.

ALL DIMENSIONS ARE IN MILIMETER UNLESS NOTED ON THE DRAWING

2.

ALL DIMENSIONS SHALL BE CONFIRMED ON SITES

APPROVED BY

PT. INDOSAT OOREDOO HUTCHISON

CHECKED BY

 PT. HUAWEI TECH INVESTMENT

REGIONAL_PROJECT_MANAGER_AREA

CHECKED BY

DATE	REVISION	SIGN

THIS DOCUMENT AND ALL MATERIAL CONTAINED HEREIN IS PROTECTED BY COPYRIGHT, TRADEMARKS AND OTHER RIGHTS WHICH ARE OWNED AND/OR CONTROLLED BY PT INDOSAT AND/OR ITS AFFILIATES OR BY OTHER PARTIES THAT HAVE LICENSED THEIR MATERIAL TO ITS AFFILIATES

PROJECT NAME

DRAWING TITLE

SITE NAME	MEKARTANI_PARABON_PL
SITE ID	13CJR0456_LBRN_EXP
SCALE	
DRAWING BY	
CHECKED BY	
VERIFIED BY	
CONTRACT NO	
PROJECT NO	

DRAWING NUMBER

TOTAL DRAWING

PAGE NUMBER

TOTAL PAGE

PROPOSED POWER CABLE

PROPOSED POWER CABLE

PROPOSED GROUNDING C

PROPOSED HYBRID CABLE

PROPOSED OPTICAL CABL

COAXIAL CABLE

EXISTING FEEDER


EXISTING JUMPER

PROPOSED JUMPER

PROPOSED CABINET

DISMANTLE EQUIPMENT

EXISTING EQUIPMENT

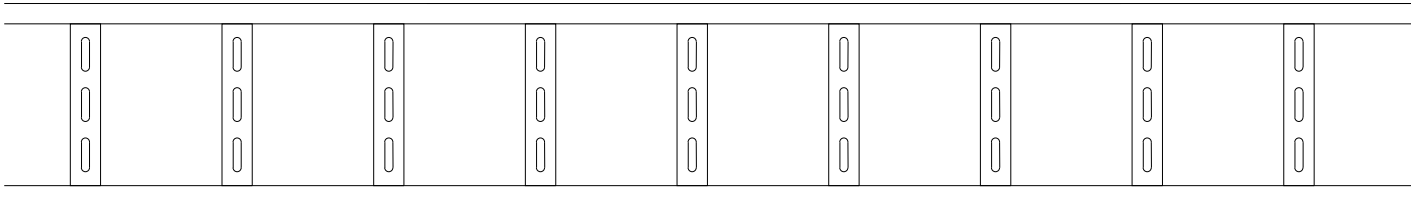

REMARKS

1. ALL DIMENSIONS ARE IN MILIMETER UNLESS NOTED ON THE DRAWING

2. ALL DIMENSIONS SHALL BE CONFIRMED ON SITES

APPROVED BY

PT. INDOSAT OOREDOO HUTCHISON

CHECKED BY

PT. HUAWEI TECH INVESTMENT

REGIONAL_PROJECT_MANAGER_AREA

CHECKED BY

DATE	REVISION	SIGN

THIS DOCUMENT AND ALL MATERIAL CONTAINED HEREIN IS PROTECTED BY COPYRIGHT, TRADEMARKS AND OTHER RIGHTS WHICH ARE OWNED AND/OR CONTROLLED BY PT INDOSAT AND/OR ITS AFFILIATES OR BY OTHER PARTIES THAT HAVE LICENSED THEIR MATERIAL TO ITS AFFILIATES

PROJECT NAME

DRAWING TITLE

SITE NAME	MEKARTANI_PARABON_PL
SITE ID	13CJR0456_LBRN_EXP
SCALE	
DRAWING BY	
CHECKED BY	
VERIFIED BY	
CONTRACT NO	
PROJECT NO	

DRAWING NUMBER	TOTAL DRAWING
PAGE NUMBER	TOTAL PAGE

PROPOSED POWER CABLE

PROPOSED POWER CABLE

PROPOSED GROUNDING C

PROPOSED HYBRID CABLE

PROPOSED OPTICAL CABL

COAXIAL CABLE

EXISTING FEEDER


EXISTING JUMPER

PROPOSED JUMPER

PROPOSED CABINET

DISMANTLE EQUIPMENT

EXISTING EQUIPMENT

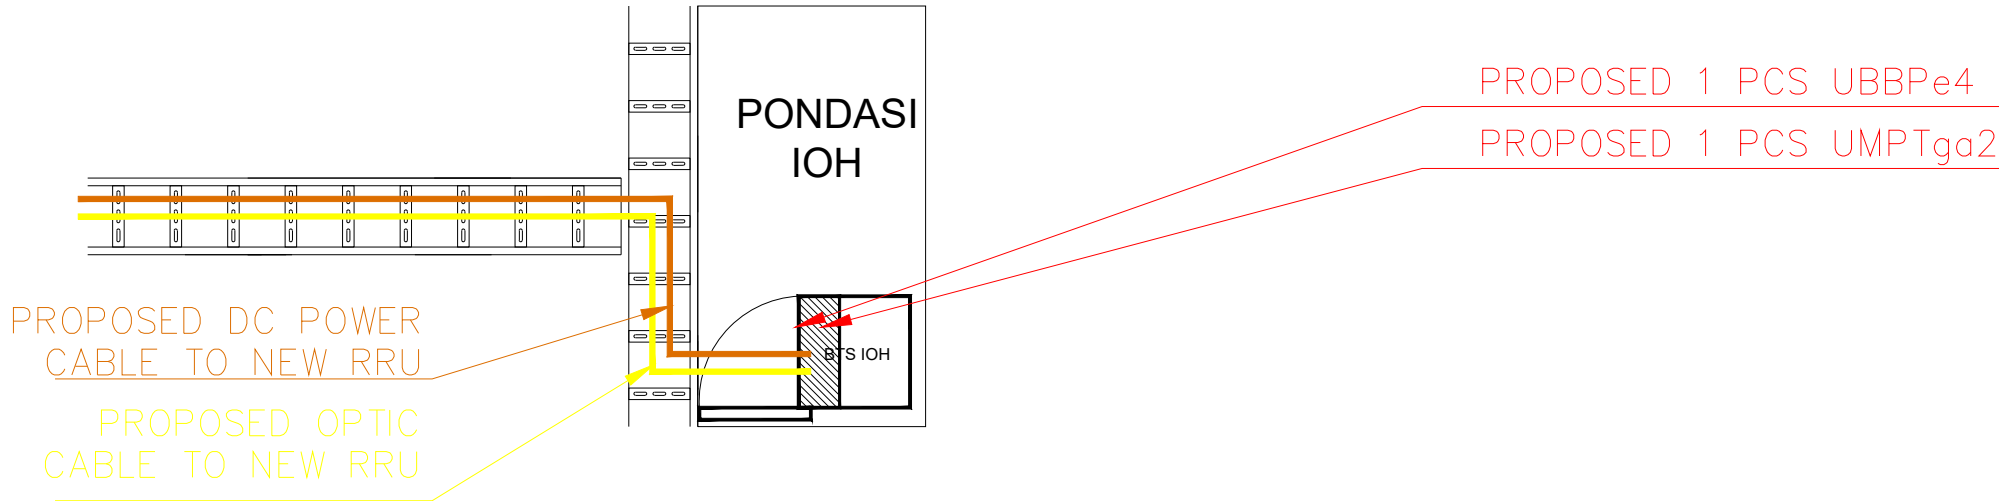

indosat

OOREDOO HUTCHISON

REMARKS

1. ALL DIMENSIONS ARE IN MILIMETER UNLESS NOTED ON THE DRAWING

2. ALL DIMENSIONS SHALL BE CONFIRMED ON SITES

APPROVED BY

PT. INDOSAT OOREDOO HUTCHISON

CHECKED BY

PT. HUAWEI TECH INVESTMENT

REGIONAL_PROJECT_MANAGER_AREA

CHECKED BY

DATE	REVISION	SIGN

THIS DOCUMENT AND ALL MATERIAL CONTAINED HEREIN IS PROTECTED BY COPYRIGHT, TRADEMARKS AND OTHER RIGHTS WHICH ARE OWNED AND/OR CONTROLLED BY PT INDOSAT AND/OR ITS AFFILIATES OR BY OTHER PARTIES THAT HAVE LICENSED THEIR MATERIAL TO ITS AFFILIATES

PROJECT NAME

DRAWING TITLE

SITE NAME	MEKARTANI_PARABON_PL
SITE ID	13CJR0456_LBRN_EXP
SCALE	
DRAWING BY	
CHECKED BY	
VERIFIED BY	
CONTRACT NO	
PROJECT NO	
DRAWING NUMBER	TOTAL DRAWING
PAGE NUMBER	TOTAL PAGE

REMARKS

1. ALL DIMENSIONS ARE IN MILIMETER UNLESS NOTED ON THE DRAWING

2. ALL DIMENSIONS SHALL BE CONFIRMED ON SITES

APPROVED BY

PT. INDOSAT OOREDOO HUTCHISON

CHECKED BY

 PT. HUAWEI TECH INVESTMENT

REGIONAL_PROJECT_MANAGER_AREA

CHECKED BY

DATE	REVISION	SIGN

THIS DOCUMENT AND ALL MATERIAL CONTAINED HEREIN IS PROTECTED BY COPYRIGHT, TRADEMARKS AND OTHER RIGHTS WHICH ARE OWNED AND/OR CONTROLLED BY PT INDOSAT AND/OR ITS AFFILIATES OR BY OTHER PARTIES THAT HAVE LICENSED THEIR MATERIAL TO ITS AFFILIATES


PROJECT NAME

DRAWING TITLE


SITE NAME	MEKARTANI_PARABON_PL
SITE ID	13CJR0456_LBRN_EXP
SCALE	
DRAWING BY	
CHECKED BY	
VERIFIED BY	
CONTRACT NO	
PROJECT NO	

DRAWING NUMBER	TOTAL DRAWING
PAGE NUMBER	TOTAL PAGE

TOWER HEIGH 71 M

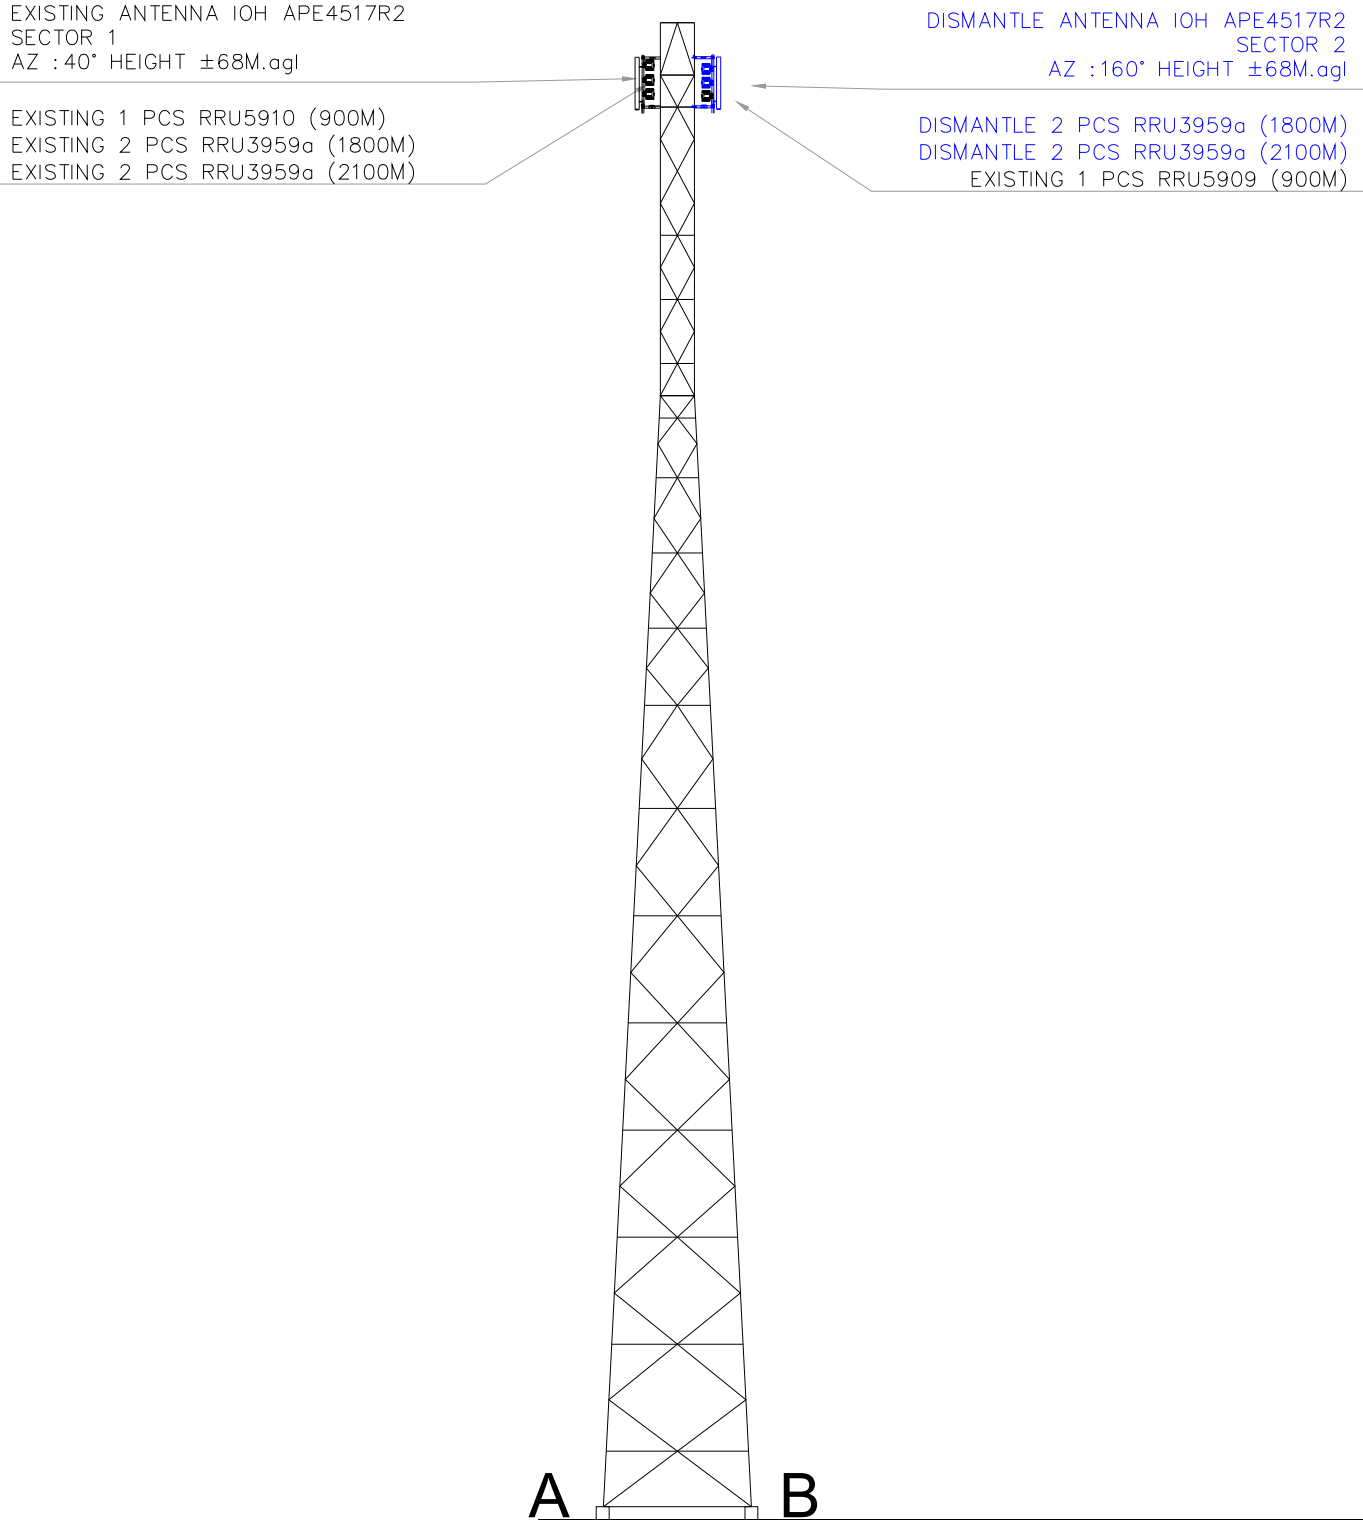

TOWER HEIGH 72 M

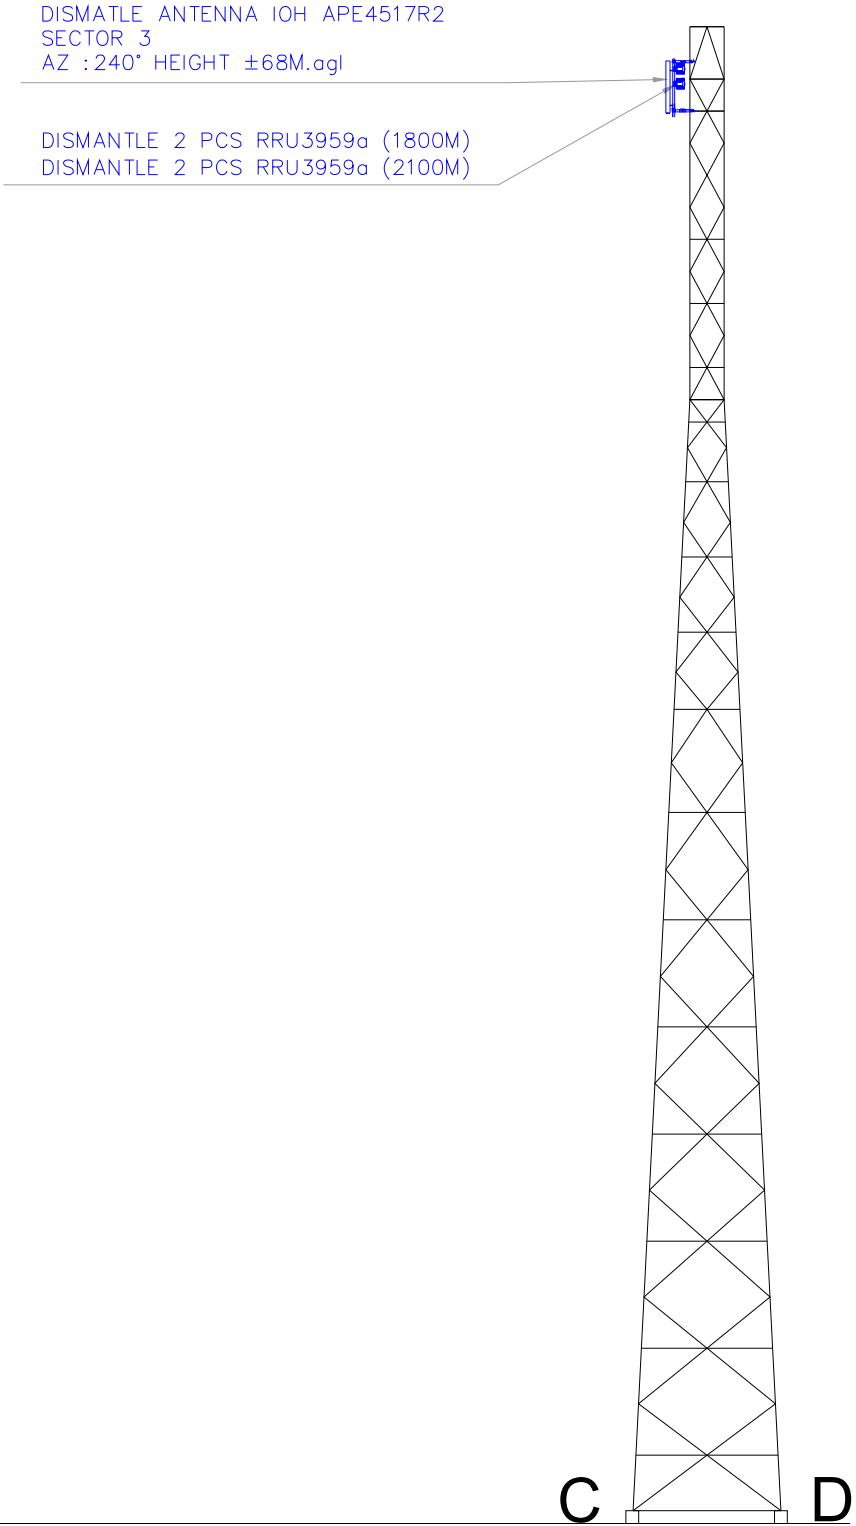

REMARKS

1. ALL DIMENSIONS ARE IN MILIMETER UNLESS NOTED ON THE DRAWING

2. ALL DIMENSIONS SHALL BE CONFIRMED ON SITES

APPROVED BY

PT. INDOSAT OOREDOO HUTCHISON

CHECKED BY

 PT. HUAWEI TECH INVESTMENT

REGIONAL_PROJECT_MANAGER_AREA

CHECKED BY


DATE	REVISION	SIGN

THIS DOCUMENT AND ALL MATERIAL CONTAINED HEREIN IS PROTECTED BY COPYRIGHT, TRADEMARKS AND OTHER RIGHTS WHICH ARE OWNED AND/OR CONTROLLED BY PT INDOSAT AND/OR ITS AFFILIATES OR BY OTHER PARTIES THAT HAVE LICENSED THEIR MATERIAL TO ITS AFFILIATES


PROJECT NAME

DRAWING TITLE


SITE NAME	MEKARTANI_PARABON_PL
SITE ID	13CJR0456_LBRN_EXP
SCALE	
DRAWING BY	
CHECKED BY	
VERIFIED BY	
CONTRACT NO	
PROJECT NO	
DRAWING NUMBER	TOTAL DRAWING
PAGE NUMBER	TOTAL PAGE

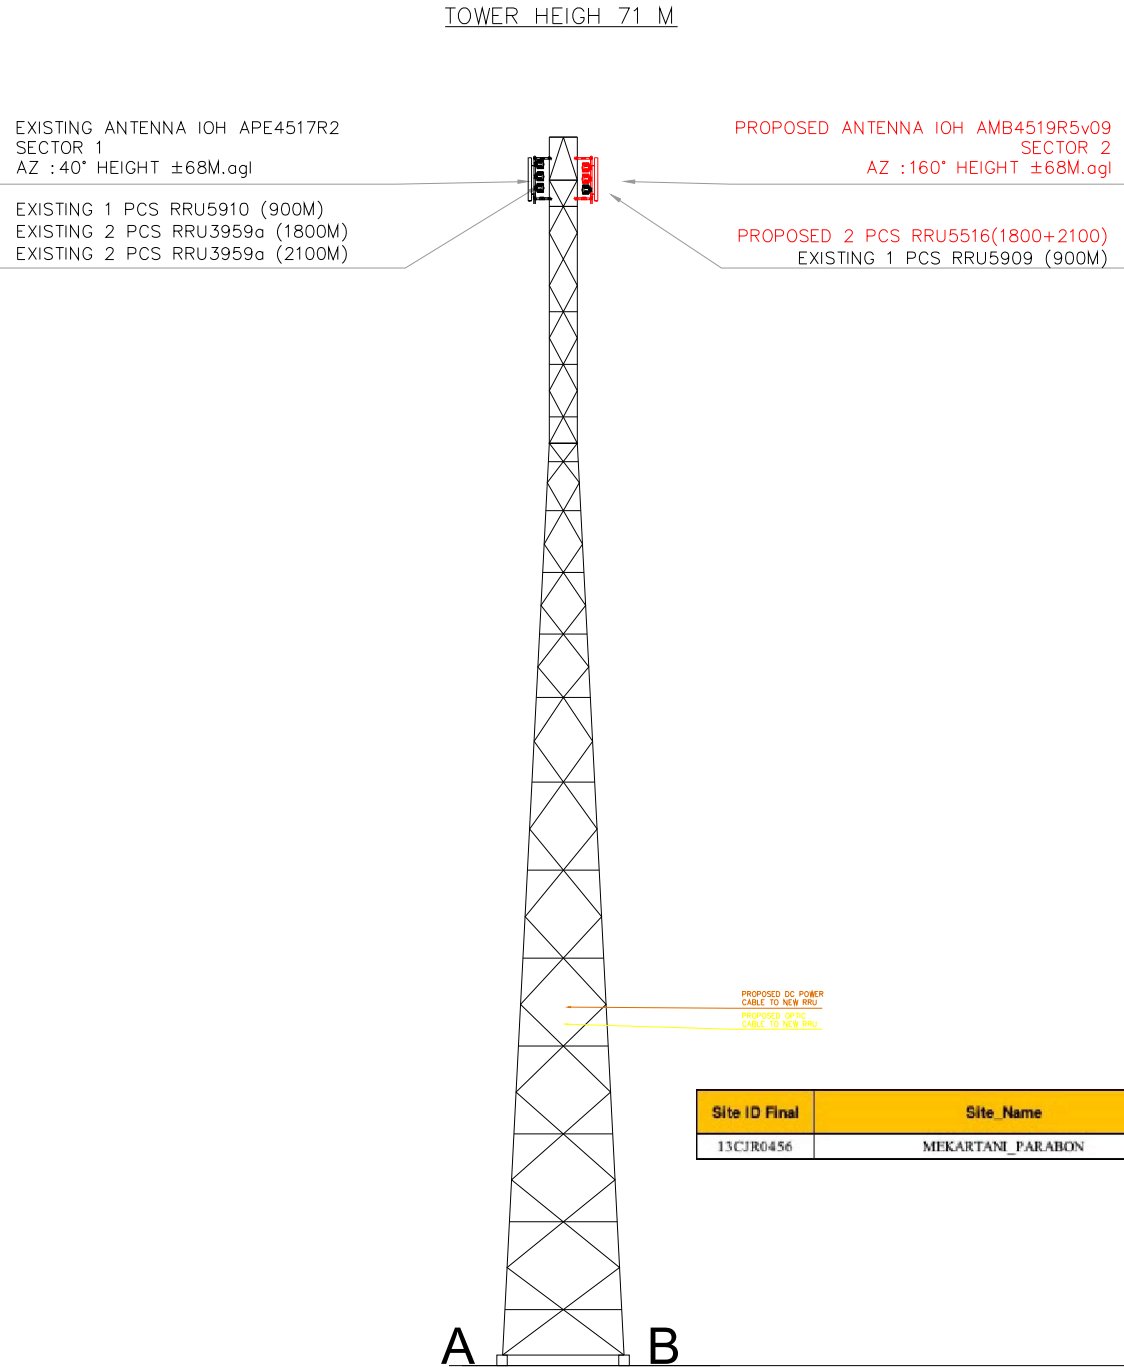

Site ID Final	Site Name	Height NFt	Final Azimuth	Final M-Tilt	Final E-Tilt
13CJR0456	MEKARTANI_PARABON	69,5	40/160235	2/2/2	2/3/3

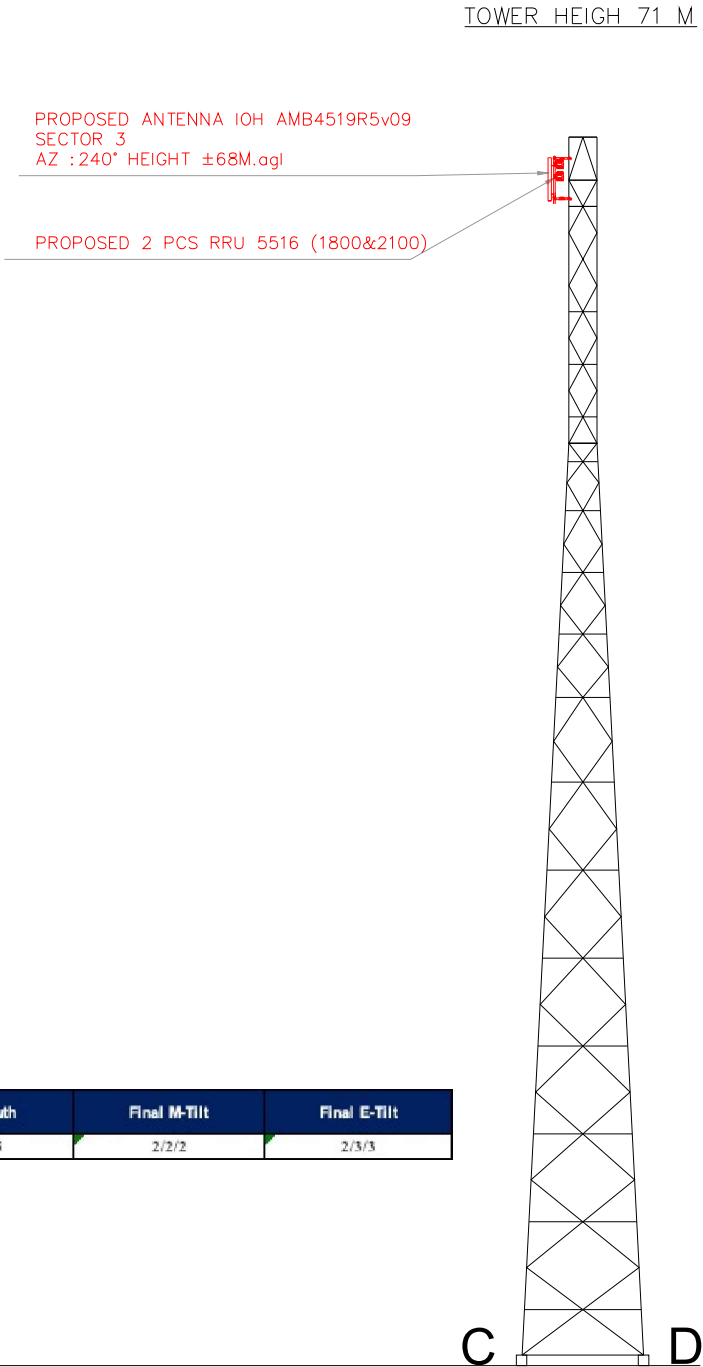

N = NEW E = EXISTING R = REMOVE	EQUIPMENT								
	EQUIPMENT TYPE	NO	SEC	TYPE	SIZE	AZ	HEIGHT	POLE/LEG	FAR-END
E	RF ANTENNA (ISAT)	A01	1	APE4517R2		40°	68,00 m	A	
R	RF ANTENNA (ISAT)	A01	2	APE4517R2		160°	68,00 m	B	
R	RF ANTENNA (ISAT)	A01	3	APE4517R2		240°	68,00 m	C	
N	RF ANTENNA (ISAT)	A02	2	AMB4519R5v09		160°	68,00 m	B	
N	RF ANTENNA (ISAT)	A02	3	AMB4519R5v10		260°	68,00 m	B	
E	RRU		1	RRU3959a (1800M)			68,00 m	A	
E	RRU		1	RRU3959a (1800M)			69,00 m	A	
E	RRU		1	RRU3959a (2100M)			68,00 m	A	
E	RRU		1	RRU3959a (2100M)			68,00 m	A	
E	RRU		1&3	RRU5910 (900M)			68,00 m	A	
E	RRU		2	RRU5909 (900M)			68,00 m	B	
R	RRU		2	RRU3959a (1800M)			68,00 m	B	
R	RRU		2	RRU3959a (1800M)			68,00 m	B	
R	RRU		3	RRU3959a (1800M)			68,00 m	C	
R	RRU		3	RRU3959a (1800M)			68,00 m	C	
R	RRU		2	RRU3959a (2100M)			68,00 m	B	
R	RRU		2	RRU3959a (2100M)			68,00 m	B	
R	RRU		3	RRU3959a (2100M)			68,00 m	C	
R	RRU		3	RRU3959a (2100M)			68,00 m	C	
N	RRU		2	RRU5516(1800+2100)			68,00 m	B	
N	RRU		2	RRU5516(1800+2100)			68,00 m	B	
N	RRU		3	RRU5516(1800+2100)			68,00 m	C	
N	RRU		3	RRU5516(1800+2100)			68,00 m	C	

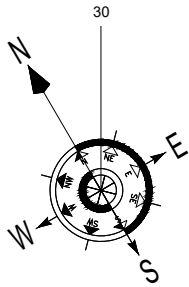

EXISTING ANTENNA IOH APE4517R2
SECTOR 1
AZ : 40° HEIGHT ±68M.agl

EXISTING 1 PCS RRU5910 (900M)
EXISTING 2 PCS RRU3959a (1800M)
EXISTING 2 PCS RRU3959a (2100M)

DISMANTLE ANTENNA IOH APE4517R2
SECTOR 3
AZ : 260° HEIGHT ±68M.agl

DISMANTLE 2 PCS RRU3959a (1800M)
DISMANTLE 2 PCS RRU3959a (2100M)

DISMANTLE ANTENNA IOH APE4517R2
SECTOR 2
AZ : 160° HEIGHT ±68M.agl

DISMANTLE 2 PCS RRU3959a (1800M)
DISMANTLE 2 PCS RRU3959a (2100M)
EXISTING 1 PCS RRU5909 (900M)

REMARKS

1. ALL DIMENSIONS ARE IN MILIMETER UNLESS NOTED ON THE DRAWING
2. ALL DIMENSIONS SHALL BE CONFIRMED ON SITES

APPROVED BY

PT. INDOSAT OOREDOO HUTCHISON

CHECKED BY

PT. HUAWEI TECH INVESTMENT

REGIONAL_PROJECT_MANAGER_AREA

CHECKED BY

DATE	REVISION	SIGN

THIS DOCUMENT AND ALL MATERIAL CONTAINED HEREIN IS PROTECTED BY COPYRIGHT, TRADEMARKS AND OTHER RIGHTS WHICH ARE OWNED AND/OR CONTROLLED BY PT INDOSAT AND/OR ITS AFFILIATES OR BY OTHER PARTIES THAT HAVE LICENSED THEIR MATERIAL TO ITS AFFILIATES



PROJECT NAME

DRAWING TITLE

SITE NAME	MEKARTANI_PARABON_PL
SITE ID	13CJR0456_LBRN_EXP
SCALE	
DRAWING BY	
CHECKED BY	
VERIFIED BY	
CONTRACT NO	
PROJECT NO	

DRAWING NUMBER TOTAL DRAWING

PAGE NUMBER TOTAL PAGE

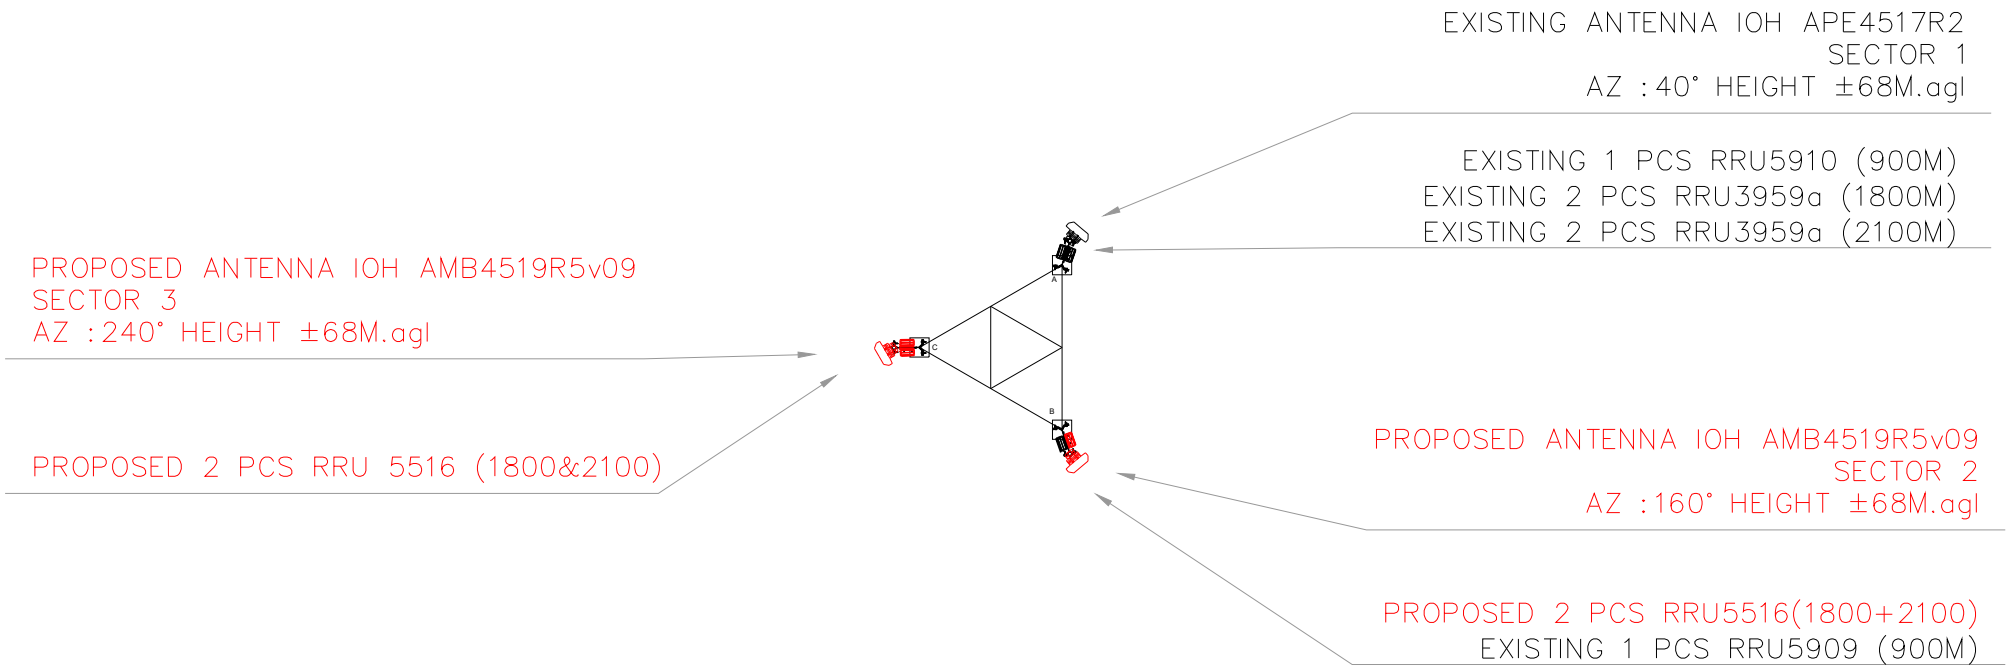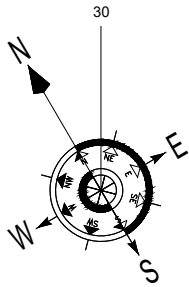

REMARKS

1. ALL DIMENSIONS ARE IN MILIMETER UNLESS NOTED ON THE DRAWING

2. ALL DIMENSIONS SHALL BE CONFIRMED ON SITES

APPROVED BY

PT. INDOSAT OOREDOO HUTCHISON

CHECKED BY

 PT. HUAWEI TECH INVESTMENT

REGIONAL_PROJECT_MANAGER_AREA

CHECKED BY

DATE	REVISION	SIGN

THIS DOCUMENT AND ALL MATERIAL CONTAINED HEREIN IS PROTECTED BY COPYRIGHT, TRADEMARKS AND OTHER RIGHTS WHICH ARE OWNED AND/OR CONTROLLED BY PT INDOSAT AND/OR ITS AFFILIATES OR BY OTHER PARTIES THAT HAVE LICENSED THEIR MATERIAL TO ITS AFFILIATES

PROJECT NAME

DRAWING TITLE

SITE NAME	MEKARTANI_PARABON_PL
SITE ID	13CJR0456_LBRN_EXP
SCALE	
DRAWING BY	
CHECKED BY	
VERIFIED BY	
CONTRACT NO	
PROJECT NO	

DRAWING NUMBER	TOTAL DRAWING
----------------	---------------

PAGE NUMBER	TOTAL PAGE
-------------	------------

REMARKS

1. ALL DIMENSIONS ARE IN MILIMETER UNLESS NOTED ON THE DRAWING

2. ALL DIMENSIONS SHALL BE CONFIRMED ON SITES

APPROVED BY

PT. INDOSAT OOREDOO HUTCHISON

CHECKED BY

 PT. HUAWEI TECH INVESTMENT

REGIONAL_PROJECT_MANAGER_AREA

CHECKED BY

DATE	REVISION	SIGN

THIS DOCUMENT AND ALL MATERIAL CONTAINED HEREIN IS PROTECTED BY COPYRIGHT, TRADEMARKS AND OTHER RIGHTS WHICH ARE OWNED AND/OR CONTROLLED BY PT INDOSAT AND/OR ITS AFFILIATES OR BY OTHER PARTIES THAT HAVE LICENSED THEIR MATERIAL TO ITS AFFILIATES


PROJECT NAME

DRAWING TITLE

SITE NAME	MEKARTANI_PARABON_PL
SITE ID	13CJR0456_LBRN_EXP
SCALE	
DRAWING BY	
CHECKED BY	
VERIFIED BY	
CONTRACT NO	
PROJECT NO	

DRAWING NUMBER	TOTAL DRAWING
----------------	---------------

PAGE NUMBER	TOTAL PAGE
-------------	------------

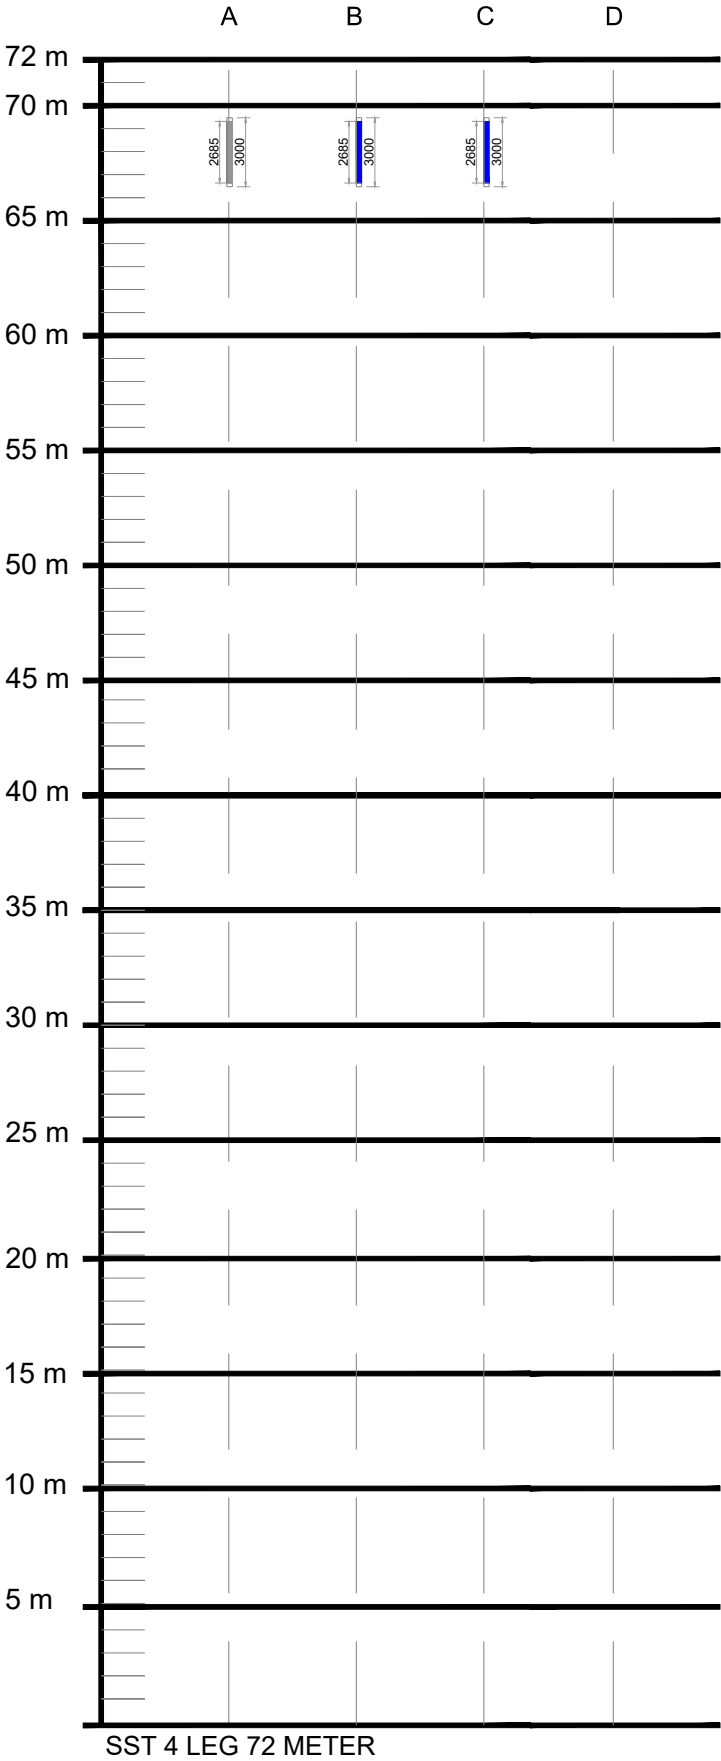

TOWER LEG ID
(CLOCKWISE FROM NORTH DIRECTION)

2685

3000

2685

3000

2685

3000

DISMANTLE RF ANTENNA IOH (ex-IOH)

EXISTING RF ANTENNA IOH (ex-IOH)

EXISTING RF ANTENNA TSEL & XL

EXISTING RRU IOH

DISMANTLE RRU IOH

3000

EXISTING MW ANTENNA IOH

REMARKS

1. ALL DIMENSIONS ARE IN MILIMETER UNLESS NOTED ON THE DRAWING

2. ALL DIMENSIONS SHALL BE CONFIRMED ON SITES

APPROVED BY

PT. INDOSAT OOREDOO HUTCHISON

CHECKED BY

 PT. HUAWEI TECH INVESTMENT

REGIONAL_PROJECT_MANAGER_AREA

CHECKED BY

DATE	REVISION	SIGN

THIS DOCUMENT AND ALL MATERIAL CONTAINED HEREIN IS PROTECTED BY COPYRIGHT, TRADEMARKS AND OTHER RIGHTS WHICH ARE OWNED AND/OR CONTROLLED BY PT INDOSAT AND/OR ITS AFFILIATES OR BY OTHER PARTIES THAT HAVE LICENSED THEIR MATERIAL TO ITS AFFILIATES


PROJECT NAME

DRAWING TITLE

SITE NAME	MEKARTANI_PARABON_PL
SITE ID	13CJR0456_LBRN_EXP
SCALE	
DRAWING BY	
CHECKED BY	
VERIFIED BY	
CONTRACT NO	
PROJECT NO	

DRAWING NUMBER	TOTAL DRAWING
----------------	---------------

PAGE NUMBER	TOTAL PAGE
-------------	------------

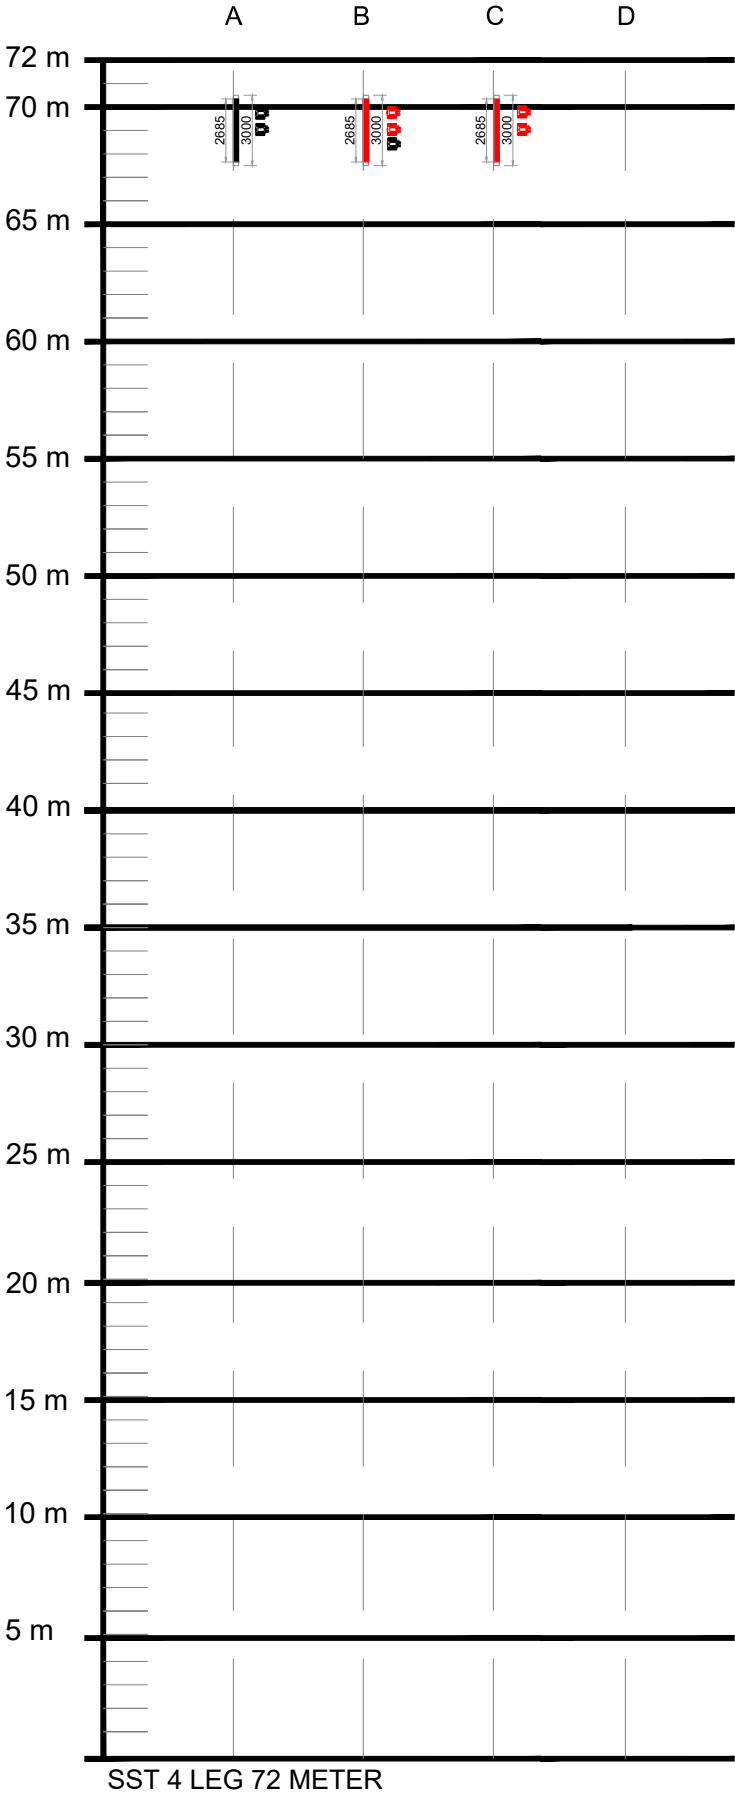

TOWER LEG ID
(CLOCKWISE FROM NORTH DIRECTION)

COLOR LEGENDS

2685

3000

PROPOSED RF ANTENNA IOH (ex-IO)

2685

3000

EXISTING RF ANTENNA IOH (ex-IO)

2685

3000

EXISTING RF ANTENNA TSEL & XL

EXISTING RRU IOH

PROPOSED RRU IOH

300

EXISTING MW ANTENNA IOH