



- PROPOSED POWER CABLE
- PROPOSED POWER CABLE
- PROPOSED GROUNDING C
- PROPOSED HYBRID CABLE
- PROPOSED OPTICAL CABL
- COAXIAL CABLE
- EXISTING FEEDER
- EXISTING JUMPER
- PROPOSED JUMPER
- PROPOSED CABINET
- DISMANTLE EQUIPMENT
- EXISTING EQUIPMENT

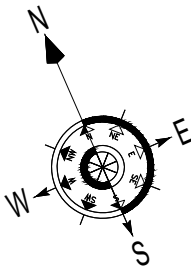

G900_(112)+2T2R L900_(10)+4T4R L1800_(30)+4T4R L2100_(25)

- Proposed 3pcs Antenna IOH APE4517R0v09
- Proposed 1pcs RRU5915 900
- Proposed 1pcs RRU5910 900
- Proposed 3pcs RRU5516 18000-2100
- Proposed 1pcs BTS
- Proposed 1pcs BBU5900
- Proposed 1pcs UMPTga2
- Proposed 1pcs UBBPh2

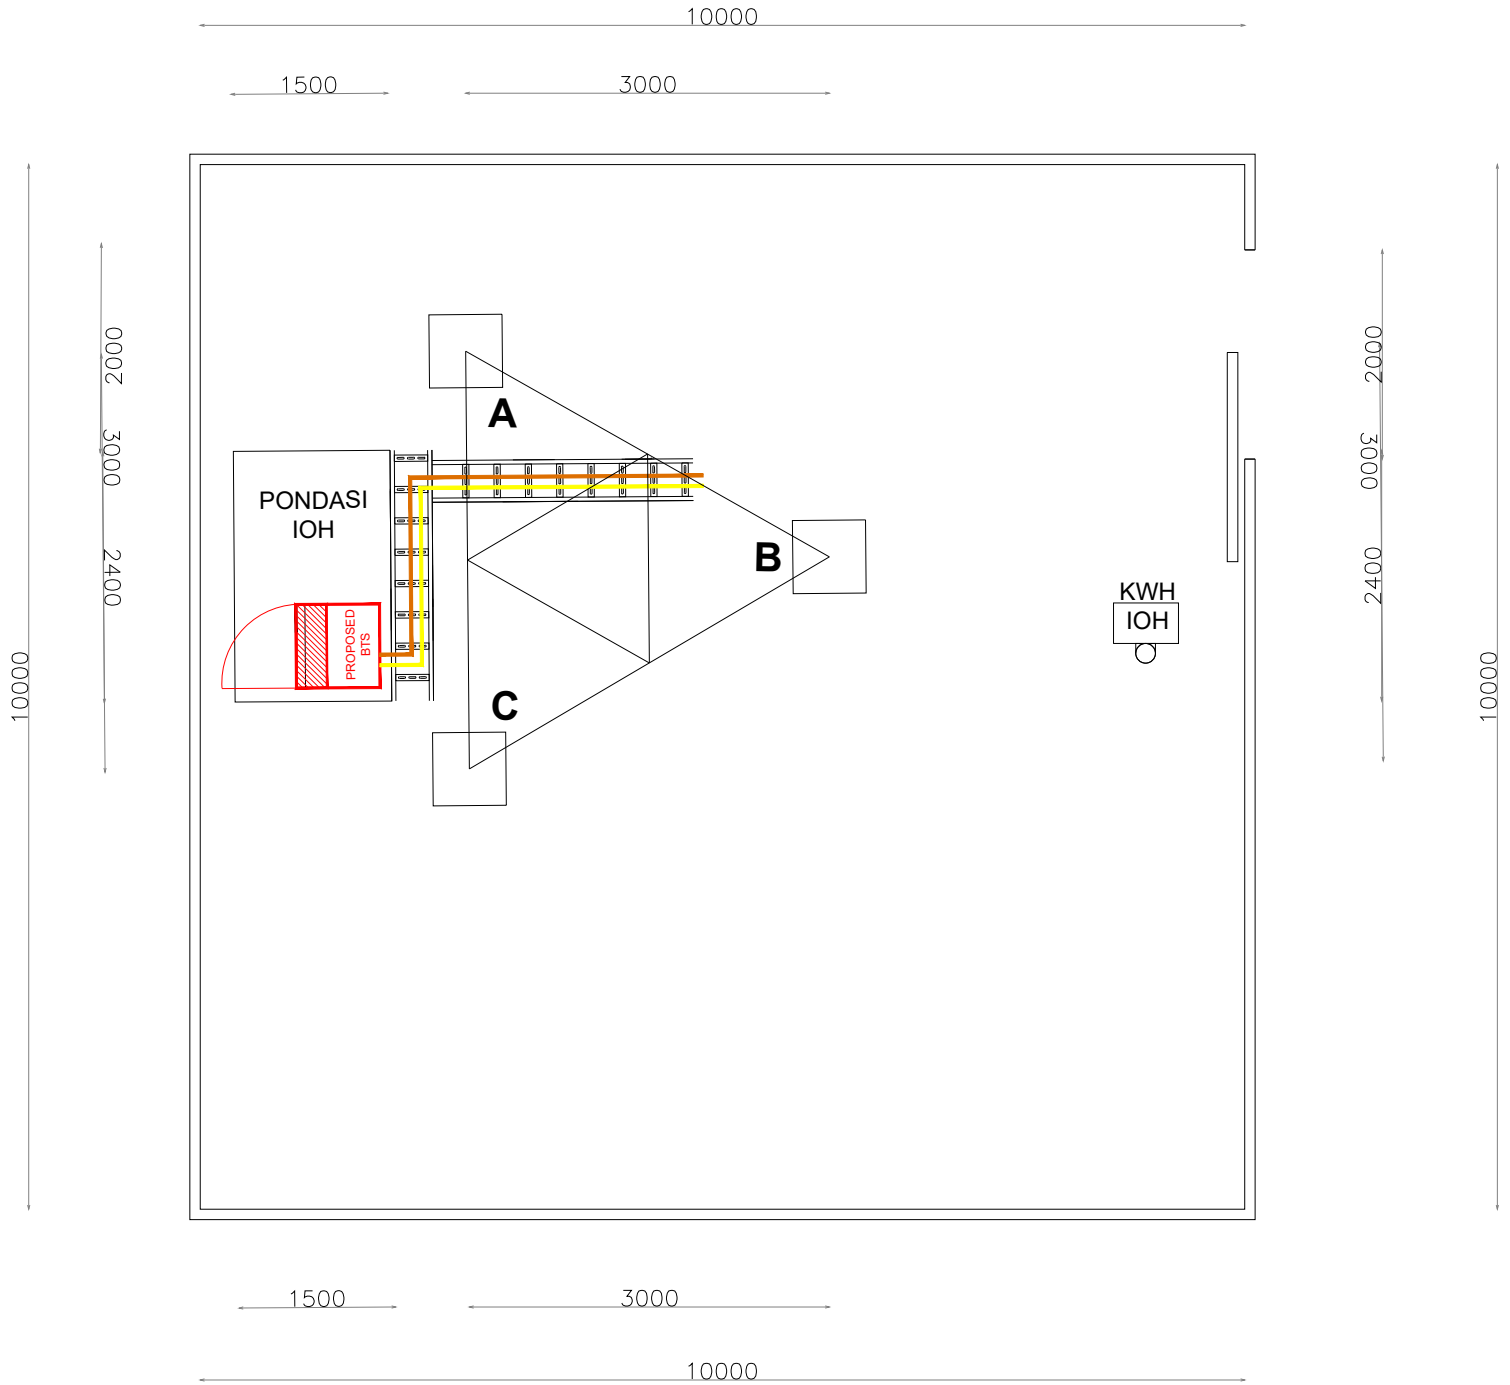

REMARKS

1. ALL DIMENSIONS ARE IN MILIMETER UNLESS NOTED ON THE DRAWING

2. ALL DIMENSIONS SHALL BE CONFIRMED ON SITES

APPROVED BY

PT. INDOSAT OOREDOO HUTCHISON

CHECKED BY

PT. HUAWEI TECH INVESTMENT

REGIONAL_PROJECT_MANAGER_AREA

CHECKED BY

DATE	REVISION	SIGN

THIS DOCUMENT AND ALL MATERIAL CONTAINED HEREIN IS PROTECTED BY COPYRIGHT, TRADEMARKS AND OTHER RIGHTS WHICH ARE OWNED AND/OR CONTROLLED BY PT INDOSAT AND/OR ITS AFFILIATES OR BY OTHER PARTIES THAT HAVE LICENSED THEIR MATERIAL TO ITS AFFILIATES

PROJECT NAME

DRAWING TITLE

SITE NAME	KALIASTANA_CM
SITE ID	13PLR0600_Q2PP_NEW
SCALE	
DRAWING BY	
CHECKED BY	
VERIFIED BY	
CONTRACT NO	
PROJECT NO	

DRAWING NUMBER

TOTAL DRAWING

PAGE NUMBER

TOTAL PAGE

PROPOSED POWER CABLE

PROPOSED POWER CABLE

PROPOSED GROUNDING C

PROPOSED HYBRID CABLE

PROPOSED OPTICAL CABL

COAXIAL CABLE

EXISTING FEEDER

EXISTING JUMPER

PROPOSED JUMPER

PROPOSED CABINET

DISMANTLE EQUIPMENT

EXISTING EQUIPMENT



REMARKS

1. ALL DIMENSIONS ARE IN MILIMETER UNLESS NOTED ON THE DRAWING

2. ALL DIMENSIONS SHALL BE CONFIRMED ON SITES

APPROVED BY

PT. INDOSAT OOREDOO HUTCHISON

CHECKED BY

 PT. HUAWEI TECH INVESTMENT

REGIONAL_PROJECT_MANAGER_AREA

CHECKED BY

DATE	REVISION	SIGN

THIS DOCUMENT AND ALL MATERIAL CONTAINED HEREIN IS PROTECTED BY COPYRIGHT, TRADEMARKS AND OTHER RIGHTS WHICH ARE OWNED AND/OR CONTROLLED BY PT INDOSAT AND/OR ITS AFFILIATES OR BY OTHER PARTIES THAT HAVE LICENSED THEIR MATERIAL TO ITS AFFILIATES

PROJECT NAME

DRAWING TITLE

SITE NAME	KALIASTANA_CM
SITE ID	13PLR0600_Q2PP_NEW
SCALE	
DRAWING BY	
CHECKED BY	
VERIFIED BY	
CONTRACT NO	
PROJECT NO	
DRAWING NUMBER	TOTAL DRAWING
PAGE NUMBER	TOTAL PAGE

PROPOSED POWER CABLE

PROPOSED POWER CABLE

PROPOSED GROUNDING C

PROPOSED HYBRID CABLE

PROPOSED OPTICAL CABL

COAXIAL CABLE

EXISTING FEEDER


EXISTING JUMPER

PROPOSED JUMPER

PROPOSED CABINET

DISMANTLE EQUIPMENT

EXISTING EQUIPMENT

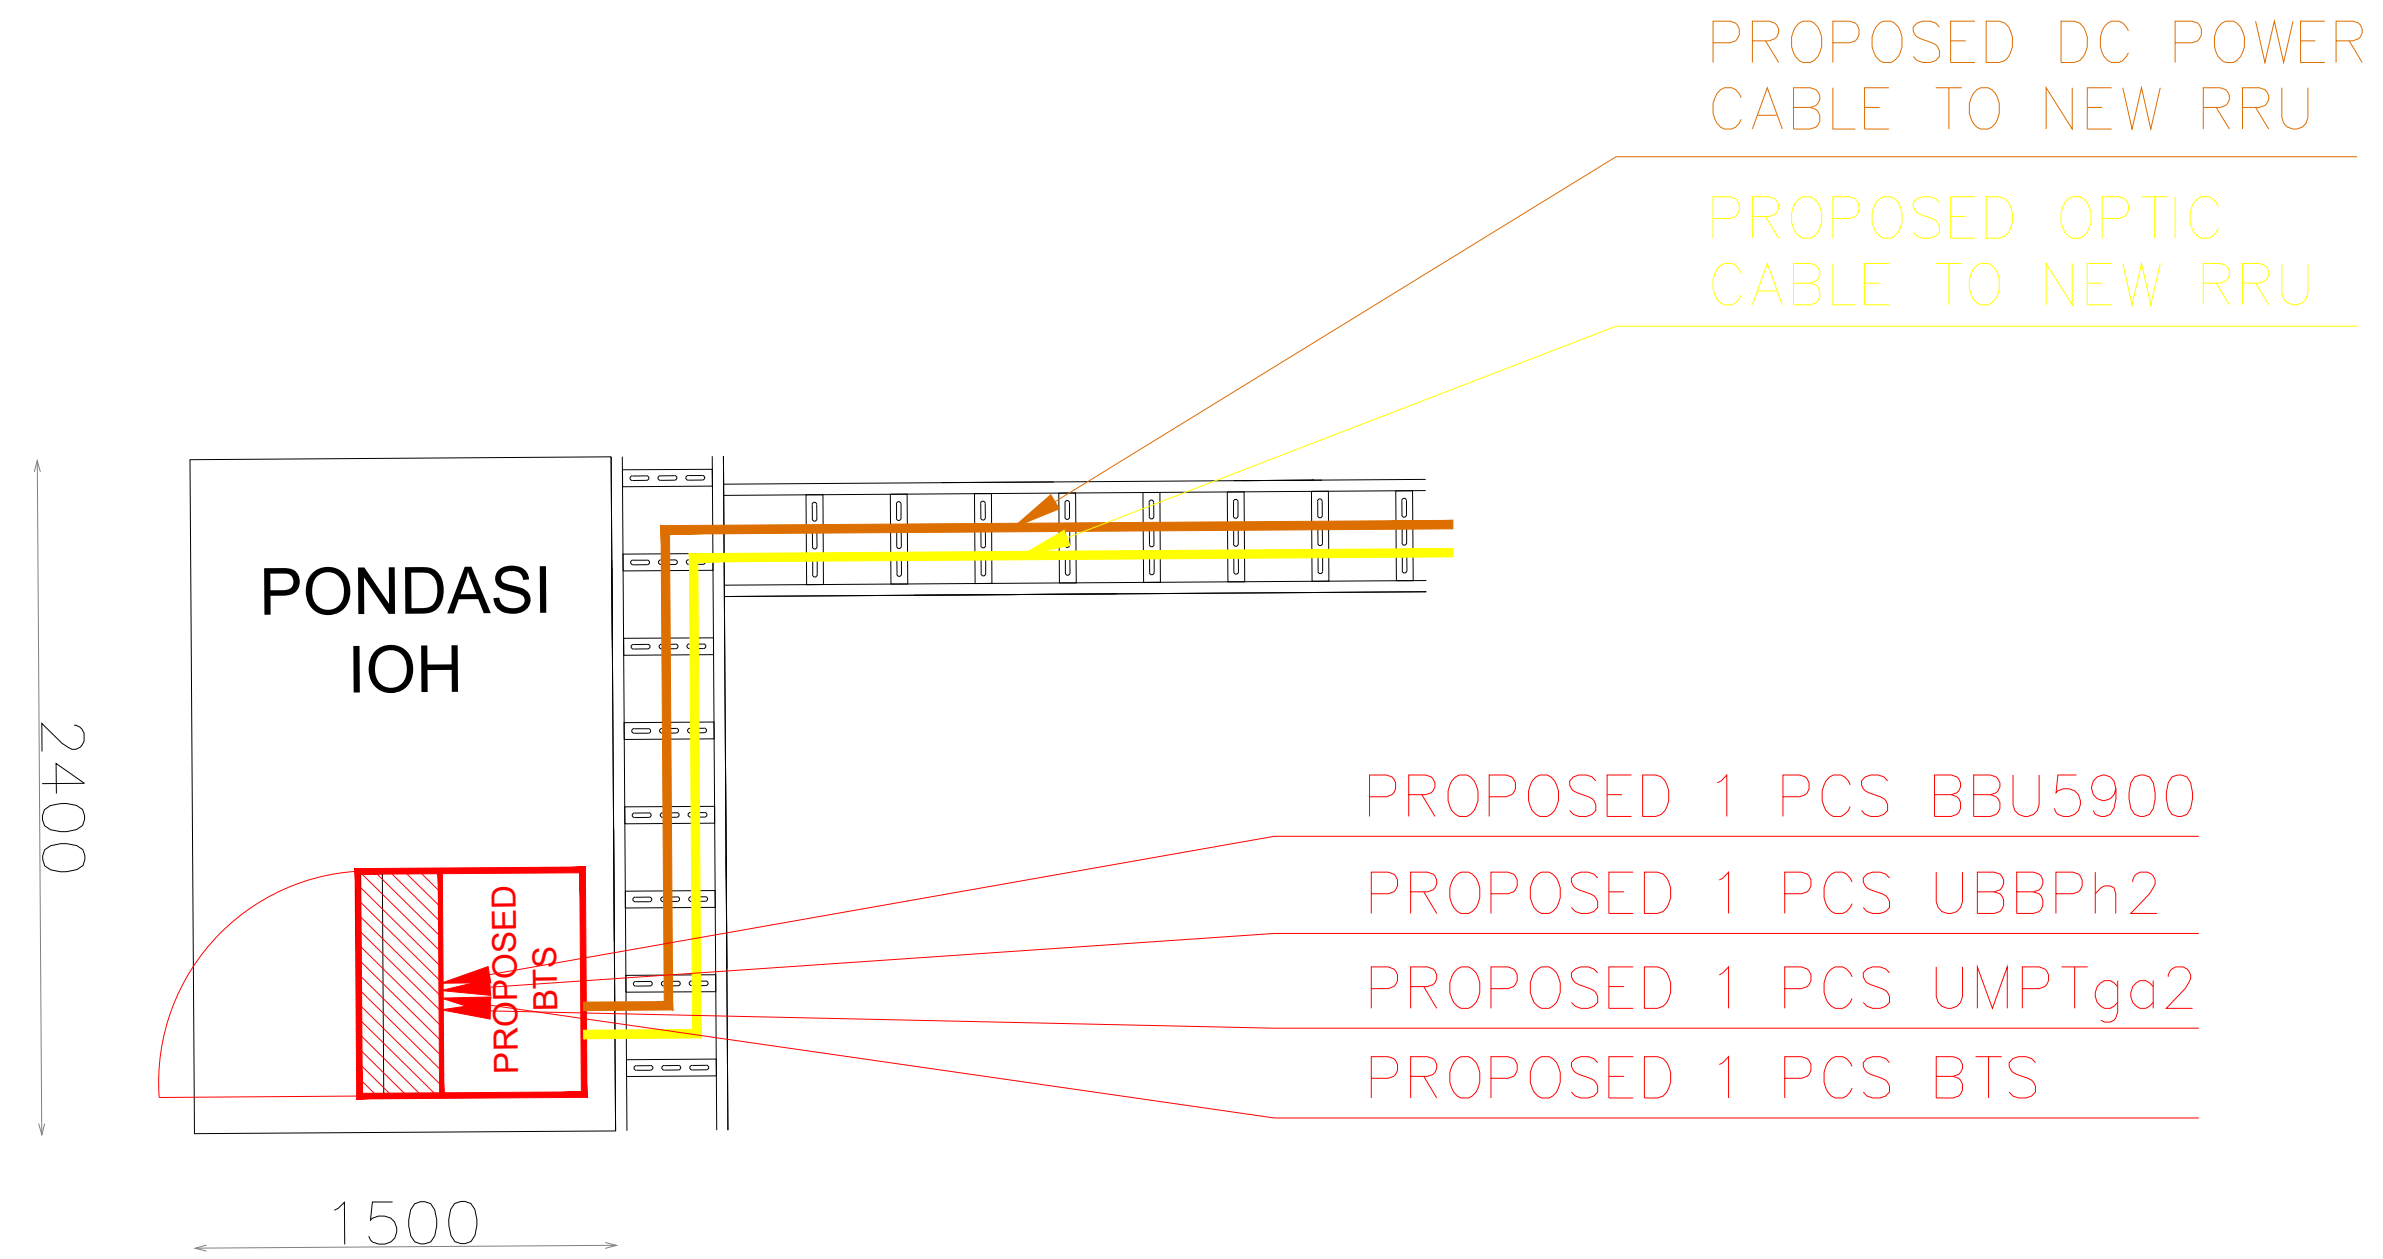

indosat

OOREDOO HUTCHISON

REMARKS

1. ALL DIMENSIONS ARE IN MILIMETER UNLESS NOTED ON THE DRAWING

2. ALL DIMENSIONS SHALL BE CONFIRMED ON SITES

APPROVED BY

PT. INDOSAT OOREDOO HUTCHISON

CHECKED BY

PT. HUAWEI TECH INVESTMENT

REGIONAL_PROJECT_MANAGER_AREA

CHECKED BY

DATE	REVISION	SIGN

THIS DOCUMENT AND ALL MATERIAL CONTAINED HEREIN IS PROTECTED BY COPYRIGHT, TRADEMARKS AND OTHER RIGHTS WHICH ARE OWNED AND/OR CONTROLLED BY PT INDOSAT AND/OR ITS AFFILIATES OR BY OTHER PARTIES THAT HAVE LICENSED THEIR MATERIAL TO ITS AFFILIATES


PROJECT NAME

DRAWING TITLE


SITE NAME	KALIASTANA_CM
SITE ID	13PLR0600_Q2PP_NEW
SCALE	
DRAWING BY	
CHECKED BY	
VERIFIED BY	
CONTRACT NO	
PROJECT NO	
DRAWING NUMBER	TOTAL DRAWING
PAGE NUMBER	TOTAL PAGE

PROP. EQUIPMENT LAYOUT

TOWER HEIGH 72 M

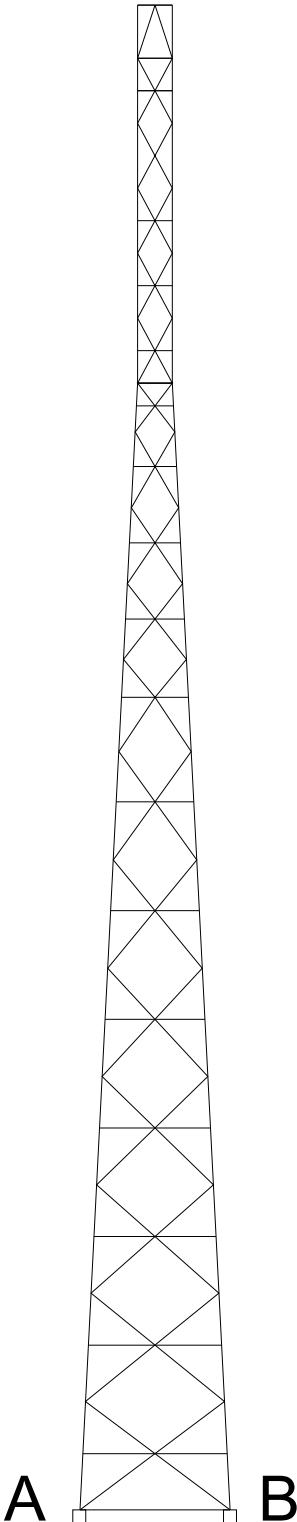

TOWER HEIGH 72 M

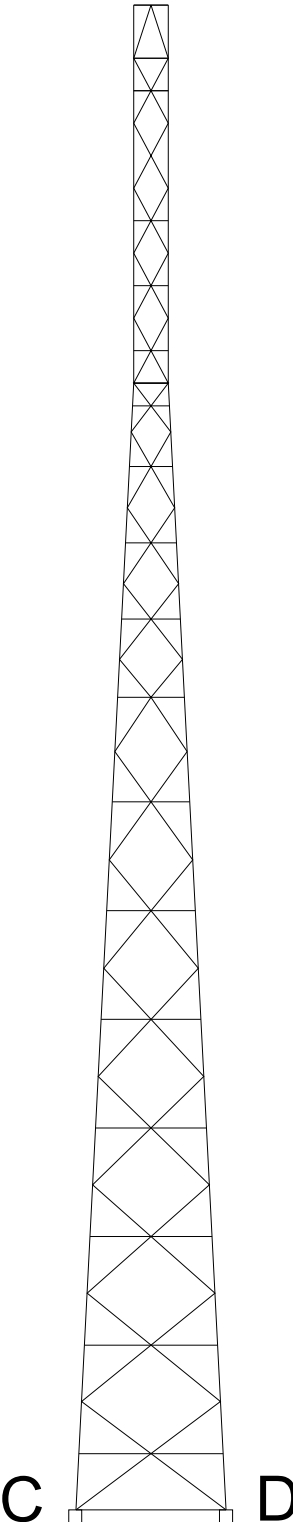

REMARKS

1. ALL DIMENSIONS ARE IN MILIMETER UNLESS NOTED ON THE DRAWING

2. ALL DIMENSIONS SHALL BE CONFIRMED ON SITES

APPROVED BY

PT. INDOSAT OOREDOO HUTCHISON

CHECKED BY

 PT. HUAWEI TECH INVESTMENT

REGIONAL_PROJECT_MANAGER_AREA

CHECKED BY

DATE	REVISION	SIGN

THIS DOCUMENT AND ALL MATERIAL CONTAINED HEREIN IS PROTECTED BY COPYRIGHT, TRADEMARKS AND OTHER RIGHTS WHICH ARE OWNED AND/OR CONTROLLED BY PT INDOSAT AND/OR ITS AFFILIATES OR BY OTHER PARTIES THAT HAVE LICENSED THEIR MATERIAL TO ITS AFFILIATES

PROJECT NAME

DRAWING TITLE

SITE NAME	KALIASTANA_CM
SITE ID	13PLR0600_Q2PP_NEW
SCALE	
DRAWING BY	
CHECKED BY	
VERIFIED BY	
CONTRACT NO	
PROJECT NO	

DRAWING NUMBER	TOTAL DRAWING
PAGE NUMBER	TOTAL PAGE

REMARKS

1. ALL DIMENSIONS ARE IN MILIMETER UNLESS NOTED ON THE DRAWING

2. ALL DIMENSIONS SHALL BE CONFIRMED ON SITES

APPROVED BY

PT. INDOSAT OOREDOO HUTCHISON

CHECKED BY

 PT. HUAWEI TECH INVESTMENT

REGIONAL_PROJECT_MANAGER_AREA

CHECKED BY

DATE	REVISION	SIGN

THIS DOCUMENT AND ALL MATERIAL CONTAINED HEREIN IS PROTECTED BY COPYRIGHT, TRADEMARKS AND OTHER RIGHTS WHICH ARE OWNED AND/OR CONTROLLED BY PT INDOSAT AND/OR ITS AFFILIATES OR BY OTHER PARTIES THAT HAVE LICENSED THEIR MATERIAL TO ITS AFFILIATES

PROJECT NAME

DRAWING TITLE

SITE NAME	KALIASTANA_CM
SITE ID	13PLR0600_Q2PP_NEW
SCALE	
DRAWING BY	
CHECKED BY	
VERIFIED BY	
CONTRACT NO	
PROJECT NO	

DRAWING NUMBER

TOTAL DRAWING

PAGE NUMBER

TOTAL PAGE

TOWER HEIGH 72 M

TOWER HEIGH 72 M

PROPOSED ANTENNA IOH APE4517R0V09
SECTOR 1
AZ :40° HEIGHT ±70M.agl

PROPOSED ANTENNA IOH APE4517R0V09
SECTOR 2
AZ :180° HEIGHT ±70M.agl

PROPOSED ANTENNA IOH APE4517R0V09
SECTOR 3
AZ :255° HEIGHT ±70M.agl

PROPOSED 1 PCS RRU 5910 (900)
PROPOSED 1 PCS RRU 5516 (1800&2100)

PROPOSED 1 PCS RRU 5516 (1800&2100)

PROPOSED 1 PCS RRU 5915 (900)
PROPOSED 1 PCS RRU 5516 (1800&2100)

EXISTING ANTENNA MW IOH 0.9ø
AZ :135° HEIGHT ±65M.agl



PROPOSED DC POWER
CABLE TO NEW RRU

PROPOSED OPTIC
CABLE TO NEW RRU

Site ID Final	Site Name	Program	TLP	Final Azimuth	Final M-Tilt	Final E-Tilt
13PLR0600	KALIASTANA_CM	Q2 2025 - New Sites (1,356 Sites)	CMI	40/180/255	2/2/2	2/2/2

N = NEW E = EXISTING R = REMOVE	EQUIPMENT								
	EQUIPMENT TYPE	NO	SEC	TYPE	SIZE	AZ	HEIGHT	POLE/LEG	FAR-END
N	RF ANTENNA (ISAT)	A01	1	APE4517R0v09		40°	70,00 m	A	
N	RF ANTENNA (ISAT)	A02	2	APE4517R0v09		180°	70,00 m	B	
N	RF ANTENNA (ISAT)	A03	3	APE4517R0v09		255°	70,00 m	C	
N	ANTENNA MW		2	A23S09MA C-3NX		135°	65,00 m	B	
N	RRU		1	RRU 5910 (900Mhz)			70,00 m	A	
N	RRU		1	RRU 5516 (1800-2100Mhz)			70,00 m	A	
N	RRU		2	RRU 5516 (1800-2100Mhz)			70,00 m	B	
N	RRU		3	RRU 5910 (900Mhz)			70,00 m	C	
N	RRU		3	RRU 5516 (1800-2100Mhz)			70,00 m	C	
N	BOARD			UMPTga2			GROUND		
N	BOARD			UBBPb2			GROUND		
N	BBU			BBU5900			GROUND		
N	BTS			BTS			GROUND		

PROP. TOWER INFORMATION

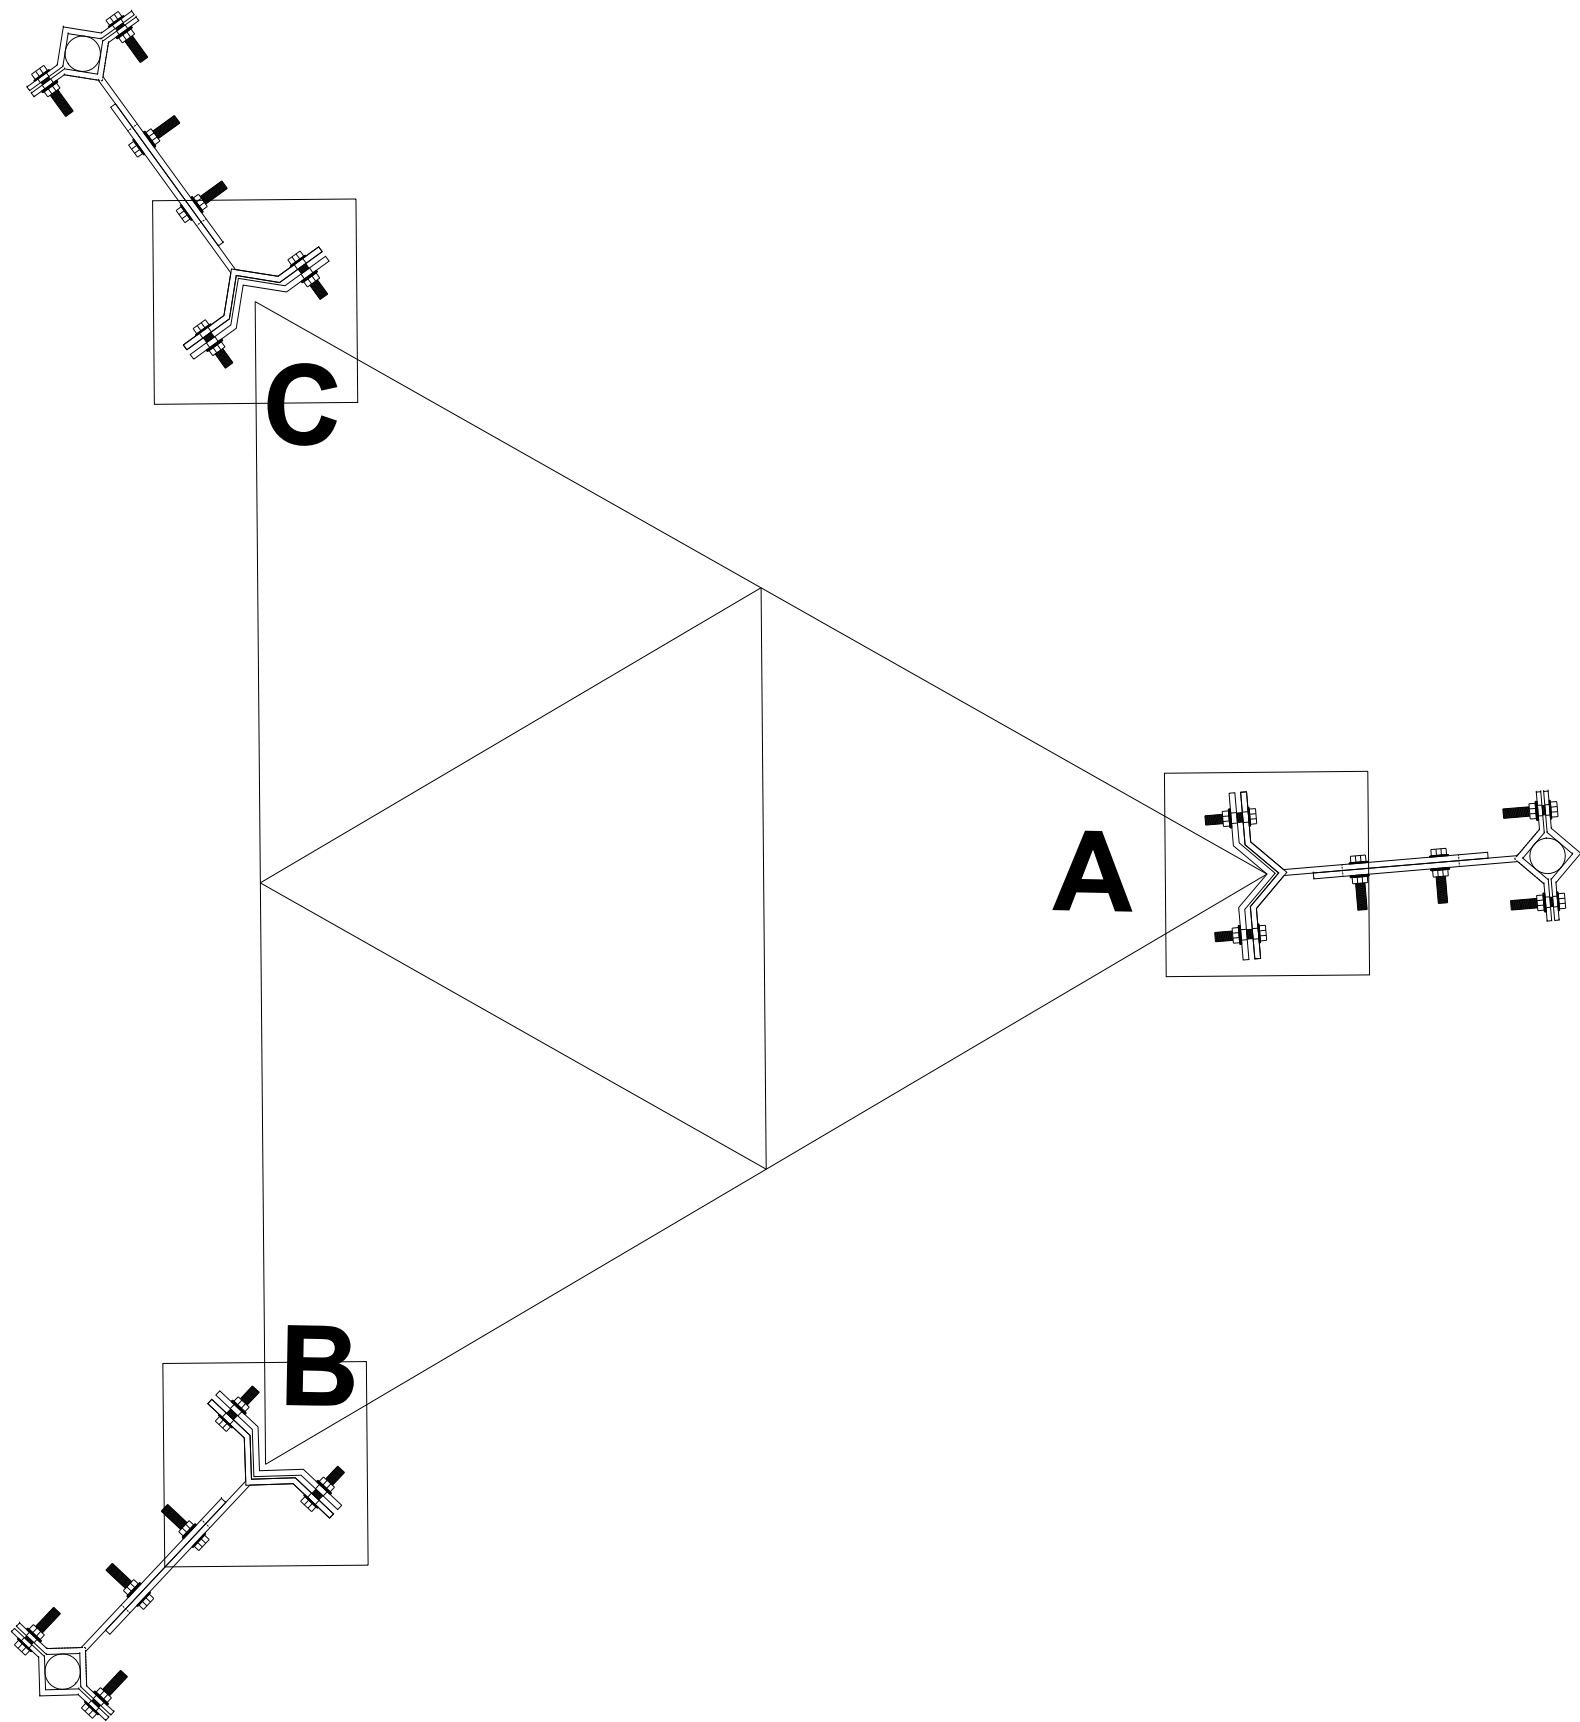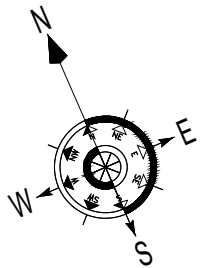

REMARKS

1. ALL DIMENSIONS ARE IN MILIMETER UNLESS NOTED ON THE DRAWING

2. ALL DIMENSIONS SHALL BE CONFIRMED ON SITES

APPROVED BY

PT. INDOSAT OOREDOO HUTCHISON

CHECKED BY

 PT. HUAWEI TECH INVESTMENT

REGIONAL_PROJECT_MANAGER_AREA

CHECKED BY

DATE	REVISION	SIGN


THIS DOCUMENT AND ALL MATERIAL CONTAINED HEREIN IS PROTECTED BY COPYRIGHT, TRADEMARKS AND OTHER RIGHTS WHICH ARE OWNED AND/OR CONTROLLED BY PT INDOSAT AND/OR ITS AFFILIATES OR BY OTHER PARTIES THAT HAVE LICENSED THEIR MATERIAL TO ITS AFFILIATES

PROJECT NAME

DRAWING TITLE

SITE NAME	KALIASTANA_CM
SITE ID	13PLR0600_Q2PP_NEW
SCALE	
DRAWING BY	
CHECKED BY	
VERIFIED BY	
CONTRACT NO	
PROJECT NO	

DRAWING NUMBER	TOTAL DRAWING
PAGE NUMBER	TOTAL PAGE

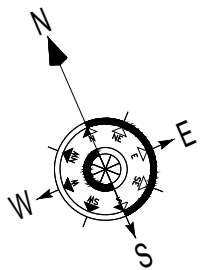


PROPOSED ANTENNA IOH APE4517ROV09
SECTOR 3
AZ : 255° HEIGHT ±70M.agl

PROPOSED 1 PCS RRU 5915 (900)
PROPOSED 1 PCS RRU 5516 (1800&2100)

PROPOSED ANTENNA IOH APE4517ROV09
SECTOR 2
AZ : 180° HEIGHT ±70M.agl

PROPOSED 1 PCS RRU 5516 (1800&2100)

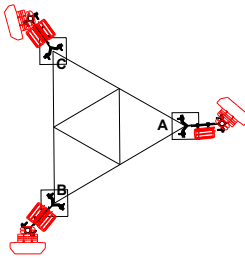

PROPOSED ANTENNA IOH APE4517ROV09
SECTOR 1
AZ : 40° HEIGHT ±70M.agl

PROPOSED 1 PCS RRU 5910 (900)
PROPOSED 1 PCS RRU 5516 (1800&2100)

REMARKS

1. ALL DIMENSIONS ARE IN MILIMETER UNLESS NOTED ON THE DRAWING

2. ALL DIMENSIONS SHALL BE CONFIRMED ON SITES

APPROVED BY

PT. INDOSAT OOREDOO HUTCHISON

CHECKED BY

PT. HUAWEI TECH INVESTMENT

REGIONAL_PROJECT_MANAGER_AREA

CHECKED BY

DATE	REVISION	SIGN

THIS DOCUMENT AND ALL MATERIAL CONTAINED HEREIN IS PROTECTED BY COPYRIGHT, TRADEMARKS AND OTHER RIGHTS WHICH ARE OWNED AND/OR CONTROLLED BY PT INDOSAT AND/OR ITS AFFILIATES OR BY OTHER PARTIES THAT HAVE LICENSED THEIR MATERIAL TO ITS AFFILIATES

PROJECT NAME

DRAWING TITLE

SITE NAME	KALIASTANA_CM
SITE ID	13PLR0600_Q2PP_NEW
SCALE	
DRAWING BY	
CHECKED BY	
VERIFIED BY	
CONTRACT NO	
PROJECT NO	

DRAWING NUMBER

TOTAL DRAWING

PAGE NUMBER

TOTAL PAGE

REMARKS

1. ALL DIMENSIONS ARE IN MILIMETER UNLESS NOTED ON THE DRAWING

2. ALL DIMENSIONS SHALL BE CONFIRMED ON SITES

APPROVED BY

PT. INDOSAT OOREDOO HUTCHISON

CHECKED BY

 PT. HUAWEI TECH INVESTMENT

REGIONAL_PROJECT_MANAGER_AREA

CHECKED BY

DATE	REVISION	SIGN


THIS DOCUMENT AND ALL MATERIAL CONTAINED HEREIN IS PROTECTED BY COPYRIGHT, TRADEMARKS AND OTHER RIGHTS WHICH ARE OWNED AND/OR CONTROLLED BY PT INDOSAT AND/OR ITS AFFILIATES OR BY OTHER PARTIES THAT HAVE LICENSED THEIR MATERIAL TO ITS AFFILIATES

PROJECT NAME

DRAWING TITLE

SITE NAME	KALIASTANA_CM
SITE ID	13PLR0600_Q2PP_NEW
SCALE	
DRAWING BY	
CHECKED BY	
VERIFIED BY	
CONTRACT NO	
PROJECT NO	

DRAWING NUMBER	TOTAL DRAWING
PAGE NUMBER	TOTAL PAGE

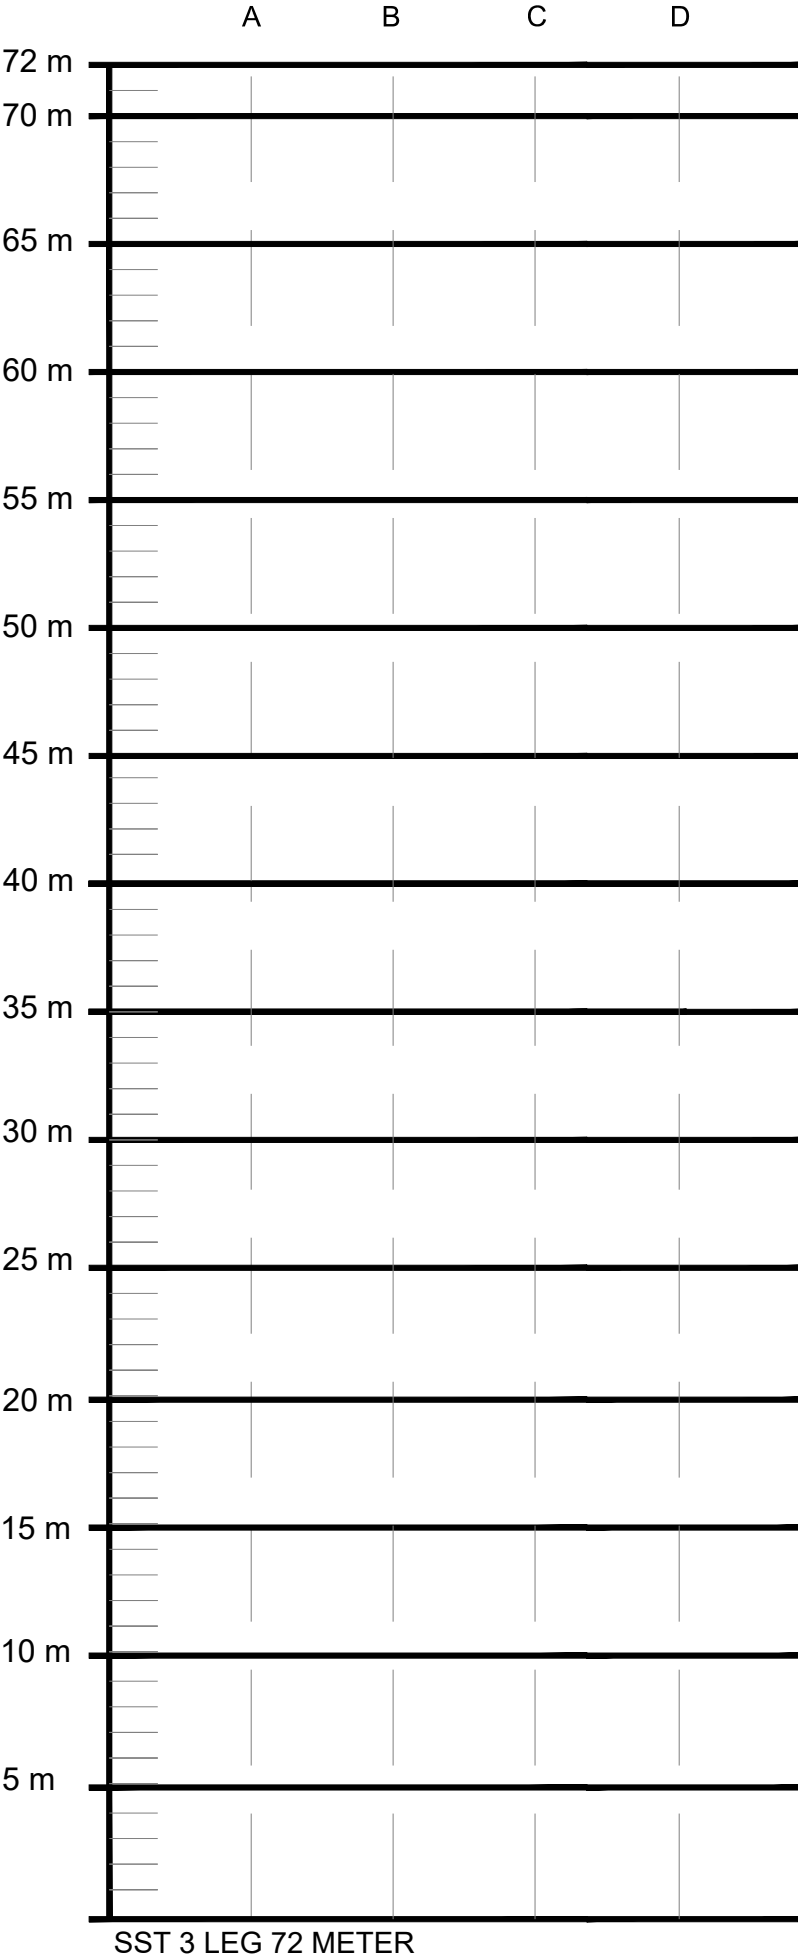

TOWER LEG ID
(CLOCKWISE FROM NORTH DIRECTION)

2685

3000

2685

3000

2685

3000

DISMANTLE RF ANTENNA IOH (ex-IO)

EXISTING RF ANTENNA IOH (ex-IO)

EXISTING RF ANTENNA TSEL & XL

EXISTING RRU IOH


DISMANTLE RRU IOH

300

EXISTING MW ANTENNA IOH



EXT. TOWER LEG DIAGRAM

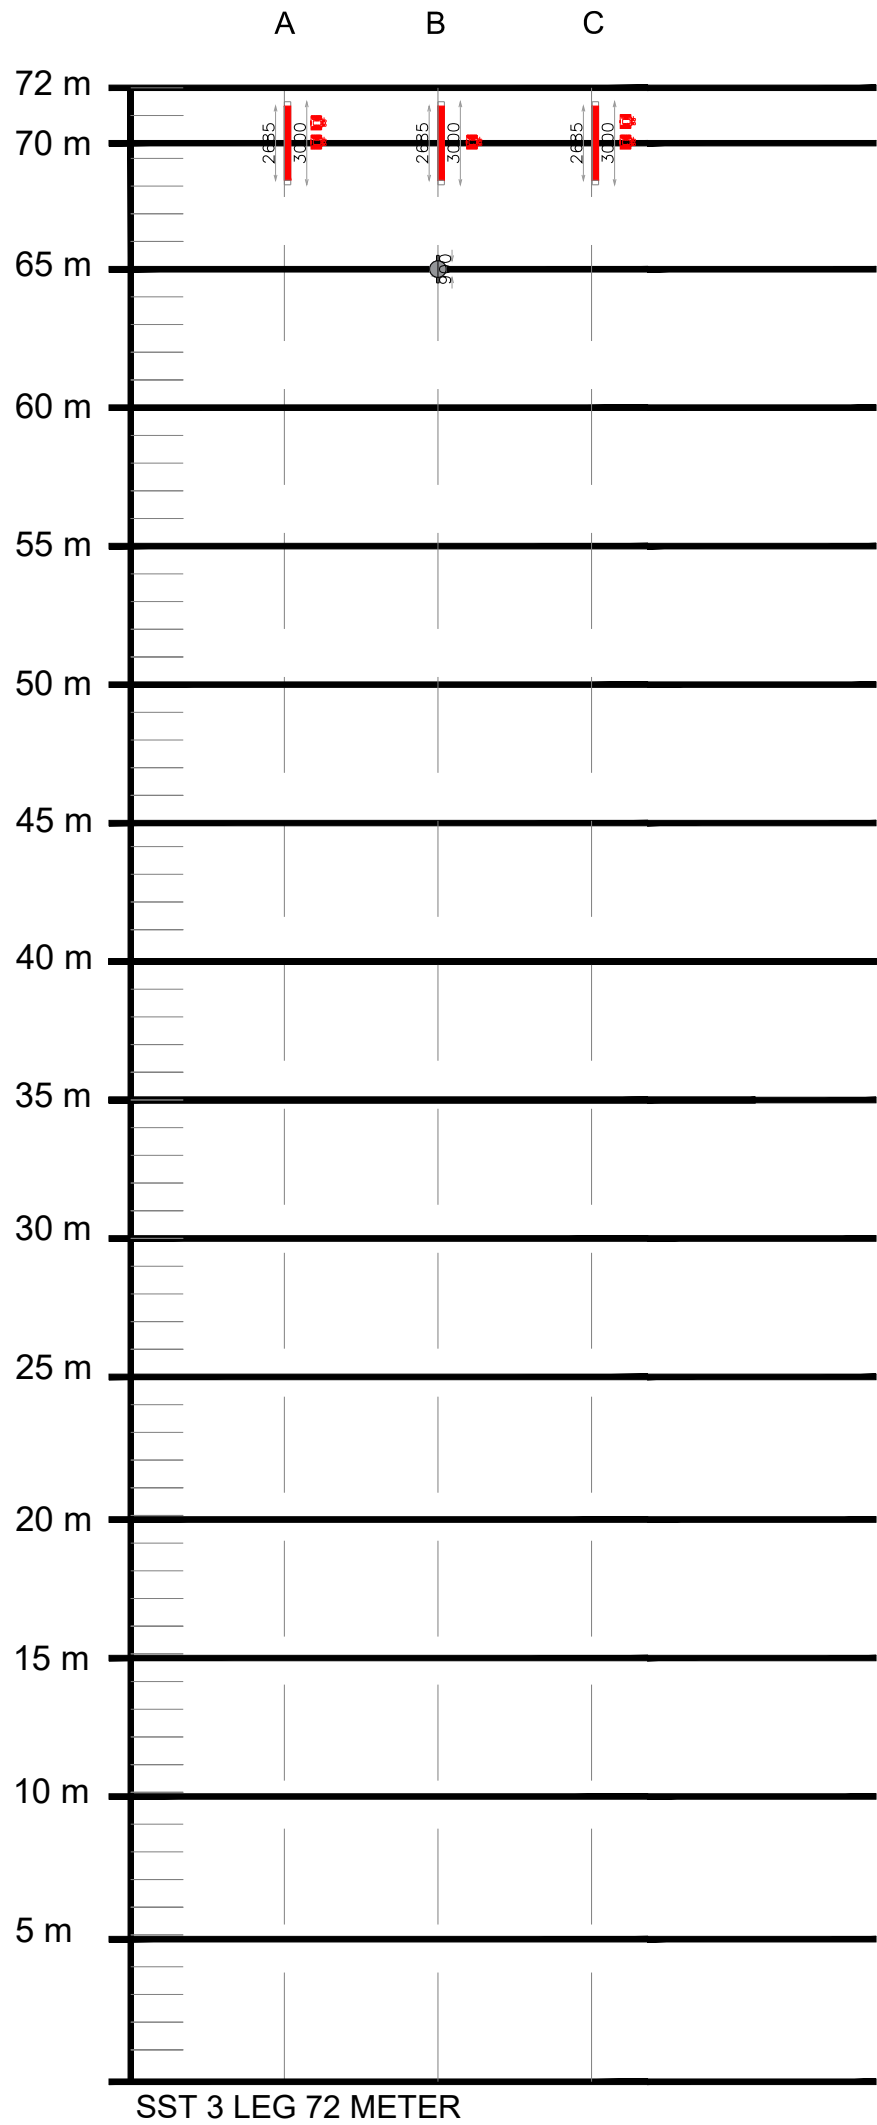

TOWER LEG ID
(CLOCKWISE FROM NORTH DIRECTION)

COLOR LEGENDS



PROPOSED RF ANTENNA IOH (ex-IO)



EXISTING RF ANTENNA IOH (ex-IO)



EXISTING RF ANTENNA TSEL & XL



EXISTING RRU IOH



PROPOSED RRU IOH



PROPOSED MW ANTENNA IOH

REMARKS

- ALL DIMENSIONS ARE IN MILIMETER UNLESS NOTED ON THE DRAWING
- ALL DIMENSIONS SHALL BE CONFIRMED ON SITES

APPROVED BY

PT. INDOSAT OOREDOO HUTCHISON

CHECKED BY



REGIONAL_PROJECT_MANAGER_AREA

CHECKED BY

DATE	REVISION	SIGN

THIS DOCUMENT AND ALL MATERIAL CONTAINED HEREIN IS PROTECTED BY COPYRIGHT, TRADEMARKS AND OTHER RIGHTS WHICH ARE OWNED AND/OR CONTROLLED BY PT INDOSAT AND/OR ITS AFFILIATES OR BY OTHER PARTIES THAT HAVE LICENSED THEIR MATERIAL TO ITS AFFILIATES

PROJECT NAME

DRAWING TITLE

SITE NAME	KALIASTANA_CM
SITE ID	13PLR0600_Q2PP_NEW
SCALE	
DRAWING BY	
CHECKED BY	
VERIFIED BY	
CONTRACT NO	
PROJECT NO	

DRAWING NUMBER	TOTAL DRAWING
PAGE NUMBER	TOTAL PAGE