
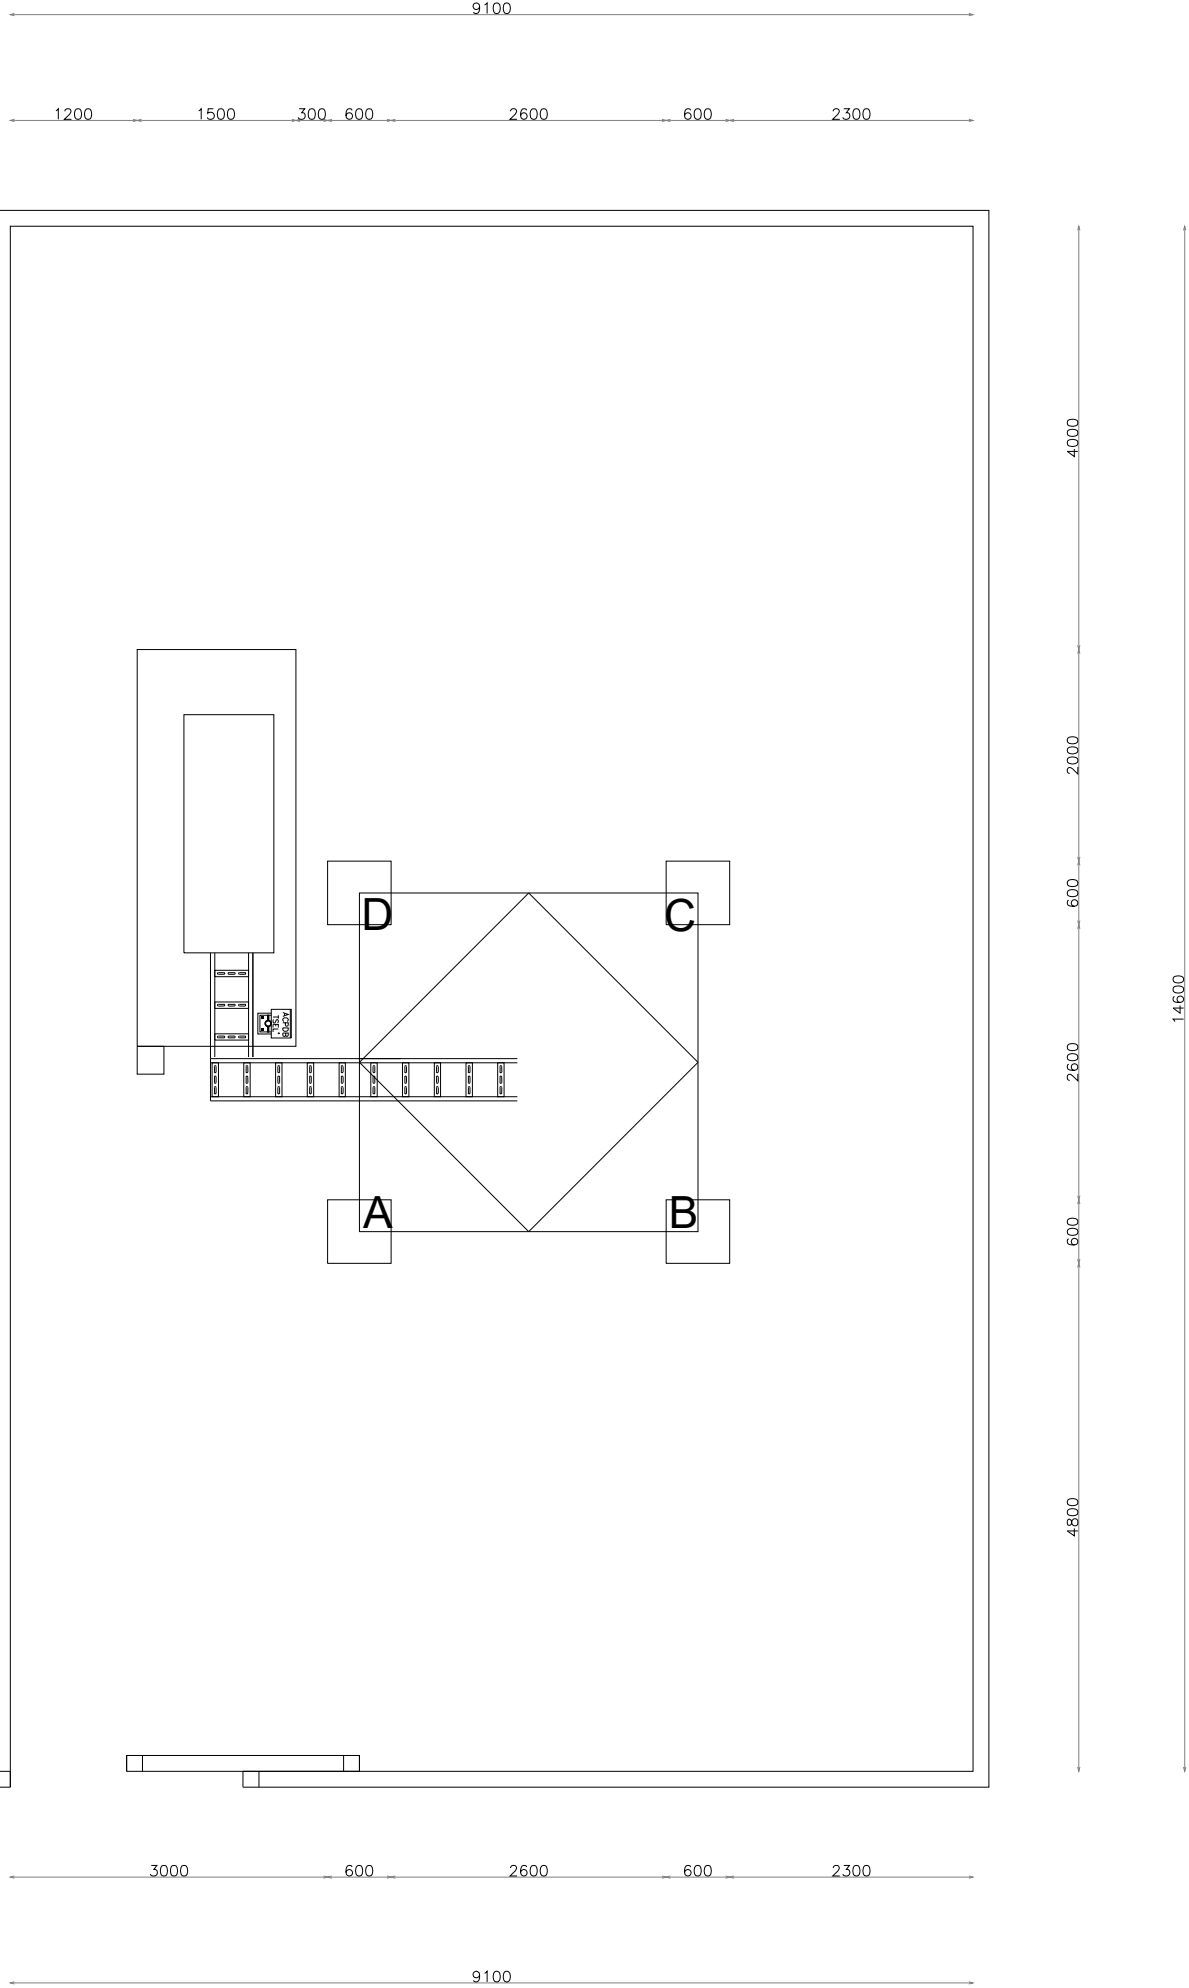


- PROPOSED POWER CABLE
- PROPOSED POWER CABLE
- PROPOSED GROUNDING C
- PROPOSED HYBRID CABLE
- PROPOSED OPTICAL CABL
- COAXIAL CABLE
- EXISTING FEEDER
- EXISTING JUMPER
- PROPOSED JUMPER
- PROPOSED CABINET
- DISMANTLE EQUIPMENT
- EXISTING EQUIPMENT

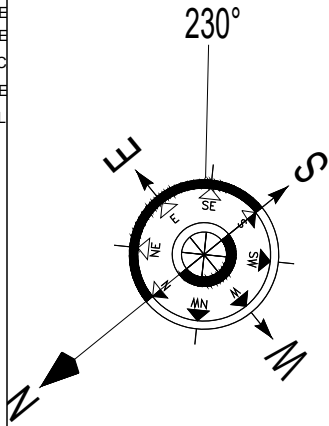

REMARKS

1. ALL DIMENSIONS ARE IN MILIMETER UNLESS NOTED ON THE DRAWING

2. ALL DIMENSIONS SHALL BE CONFIRMED ON SITES

APPROVED BY

CHECKED BY

PT. HUAWEI TECH INVESTMENT

REGIONAL_PROJECT_MANAGER_AREA

CHECKED BY

DATE	REVISION	SIGN

THIS DOCUMENT AND ALL MATERIAL CONTAINED HEREIN IS PROTECTED BY COPYRIGHT, TRADEMARKS AND OTHER RIGHTS WHICH ARE OWNED AND/OR CONTROLLED BY PT INDOSAT AND/OR ITS AFFILIATES OR BY OTHER PARTIES THAT HAVE LICENSED THEIR MATERIAL TO ITS AFFILIATES

PROJECT NAME

DRAWING TITLE

SITE NAME	CIPARAY_MAJALAYA
SITE ID	ZBDG_4722
SCALE	
DRAWING BY	
CHECKED BY	
VERIFIED BY	
CONTRACT NO	
PROJECT NO	
DRAWING NUMBER	TOTAL DRAWING
PAGE NUMBER	TOTAL PAGE

PROPOSED POWER CABLE

PROPOSED POWER CABLE

PROPOSED GROUNDING C

PROPOSED HYBRID CABLE

PROPOSED OPTICAL CABL

COAXIAL CABLE

EXISTING FEEDER


EXISTING JUMPER

PROPOSED JUMPER

PROPOSED CABINET

DISMANTLE EQUIPMENT

EXISTING EQUIPMENT

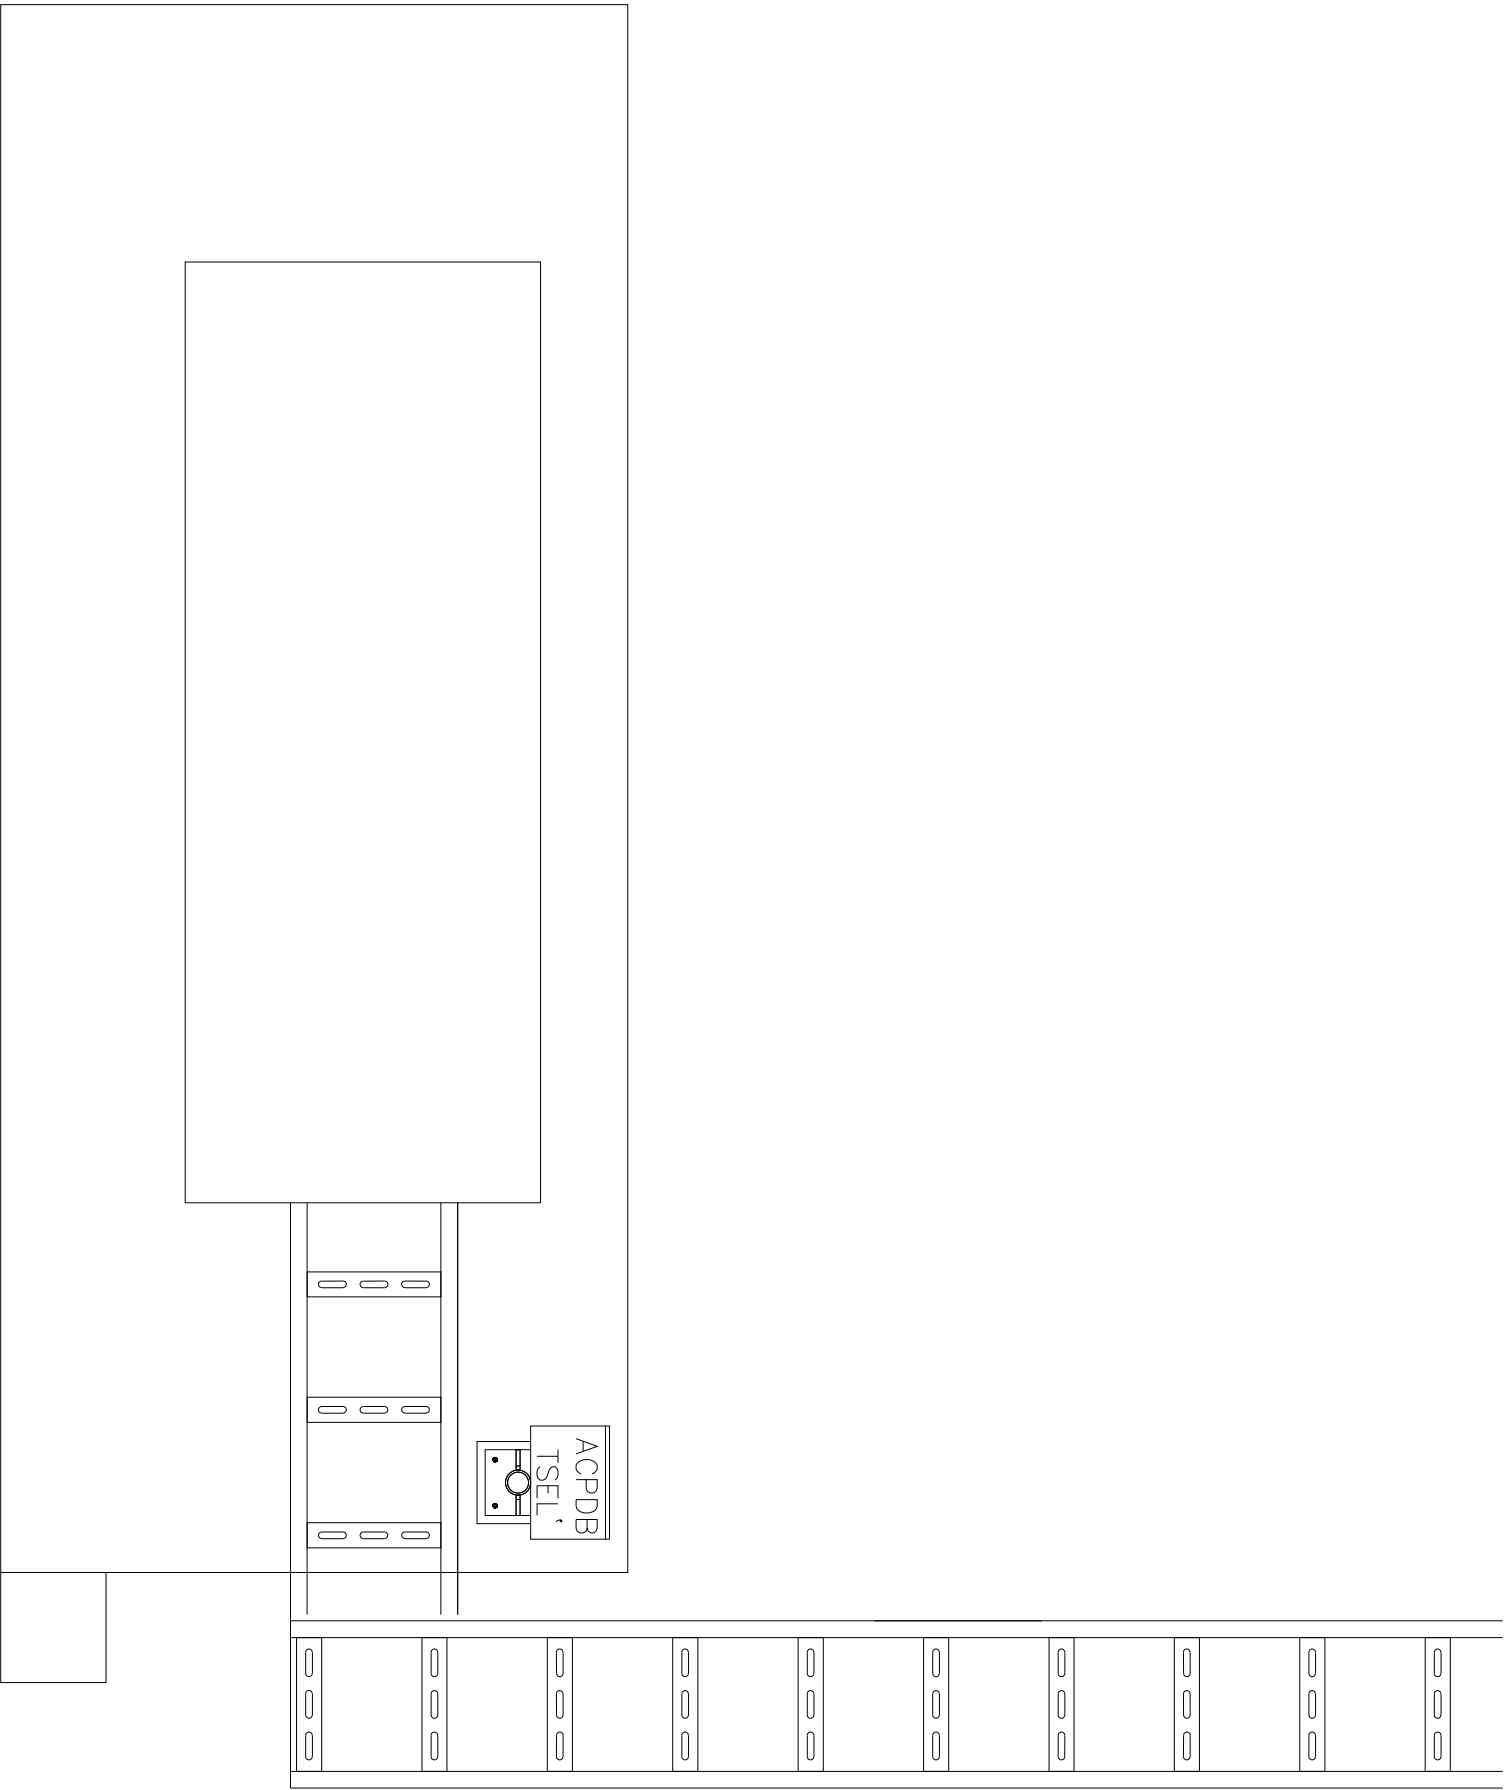

REMARKS

1.

ALL DIMENSIONS ARE IN MILIMETER UNLESS NOTED ON THE DRAWING

2.

ALL DIMENSIONS SHALL BE CONFIRMED ON SITES

APPROVED BY

CHECKED BY

PT. HUAWEI TECH INVESTMENT

REGIONAL_PROJECT_MANAGER_AREA

CHECKED BY

DATE	REVISION	SIGN

THIS DOCUMENT AND ALL MATERIAL CONTAINED HEREIN IS PROTECTED BY COPYRIGHT, TRADEMARKS AND OTHER RIGHTS WHICH ARE OWNED AND/OR CONTROLLED BY PT INDOSAT AND/OR ITS AFFILIATES OR BY OTHER PARTIES THAT HAVE LICENSED THEIR MATERIAL TO ITS AFFILIATES

PROJECT NAME

DRAWING TITLE

SITE NAME	CIPARAY_MAJALAYA
SITE ID	ZBDG_4722
SCALE	
DRAWING BY	
CHECKED BY	
VERIFIED BY	
CONTRACT NO	
PROJECT NO	
DRAWING NUMBER	TOTAL DRAWING
PAGE NUMBER	TOTAL PAGE

PROPOSED POWER CABLE

PROPOSED POWER CABLE

PROPOSED GROUNDING C

PROPOSED HYBRID CABLE

PROPOSED OPTICAL CABL

COAXIAL CABLE

EXISTING FEEDER


EXISTING JUMPER

PROPOSED JUMPER

PROPOSED CABINET

DISMANTLE EQUIPMENT

EXISTING EQUIPMENT

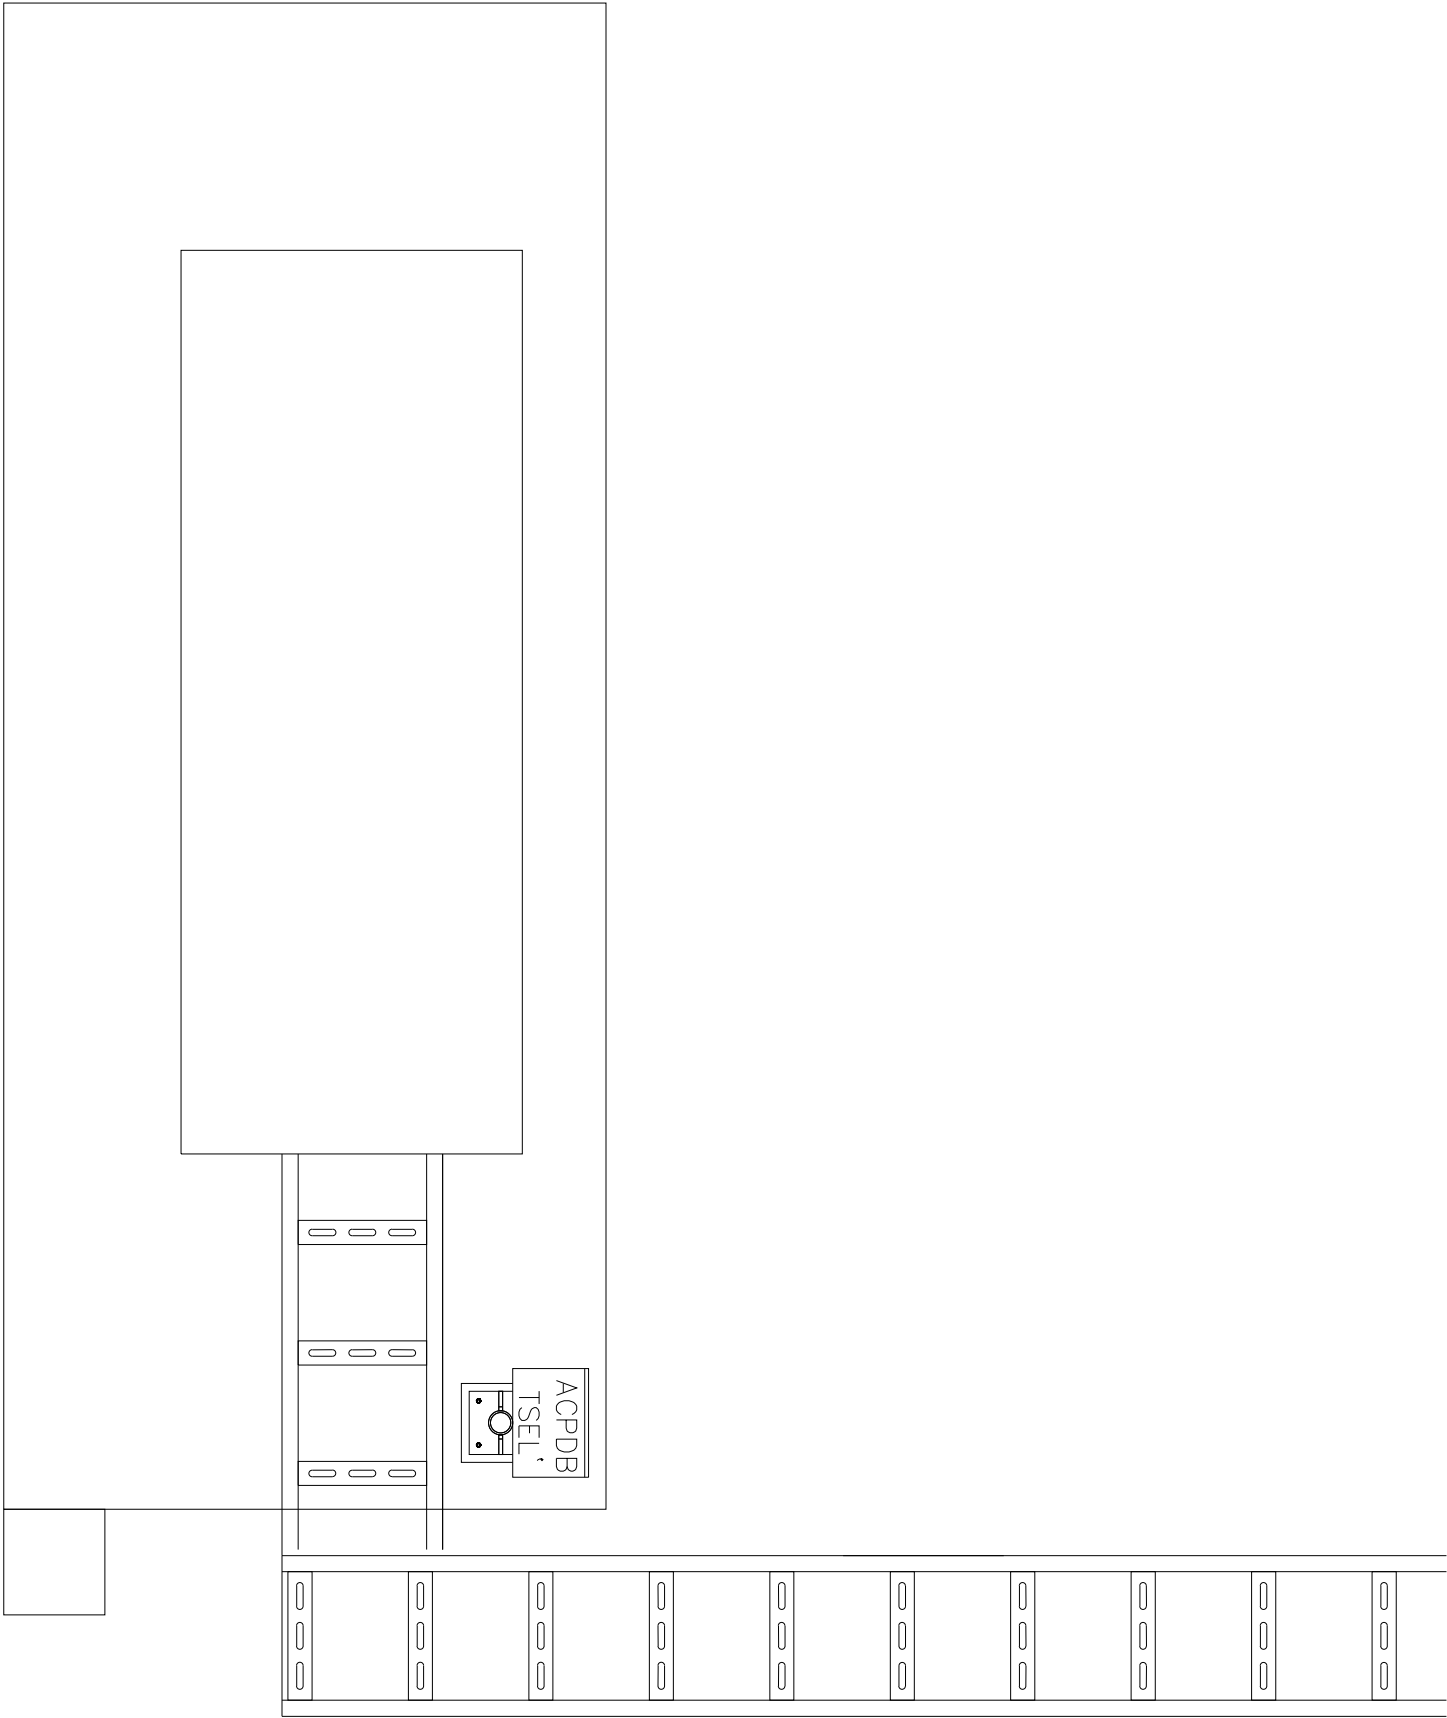

REMARKS

1. ALL DIMENSIONS ARE IN MILIMETER UNLESS NOTED ON THE DRAWING

2. ALL DIMENSIONS SHALL BE CONFIRMED ON SITES

APPROVED BY

CHECKED BY

PT. HUAWEI TECH INVESTMENT

REGIONAL_PROJECT_MANAGER_AREA

CHECKED BY

DATE	REVISION	SIGN


THIS DOCUMENT AND ALL MATERIAL CONTAINED HEREIN IS PROTECTED BY COPYRIGHT, TRADEMARKS AND OTHER RIGHTS WHICH ARE OWNED AND/OR CONTROLLED BY PT INDOSAT AND/OR ITS AFFILIATES OR BY OTHER PARTIES THAT HAVE LICENSED THEIR MATERIAL TO ITS AFFILIATES

PROJECT NAME

DRAWING TITLE

SITE NAME	CIPARAY_MAJALAYA
SITE ID	ZBDG_4722
SCALE	
DRAWING BY	
CHECKED BY	
VERIFIED BY	
CONTRACT NO	
PROJECT NO	

DRAWING NUMBER	TOTAL DRAWING
PAGE NUMBER	TOTAL PAGE

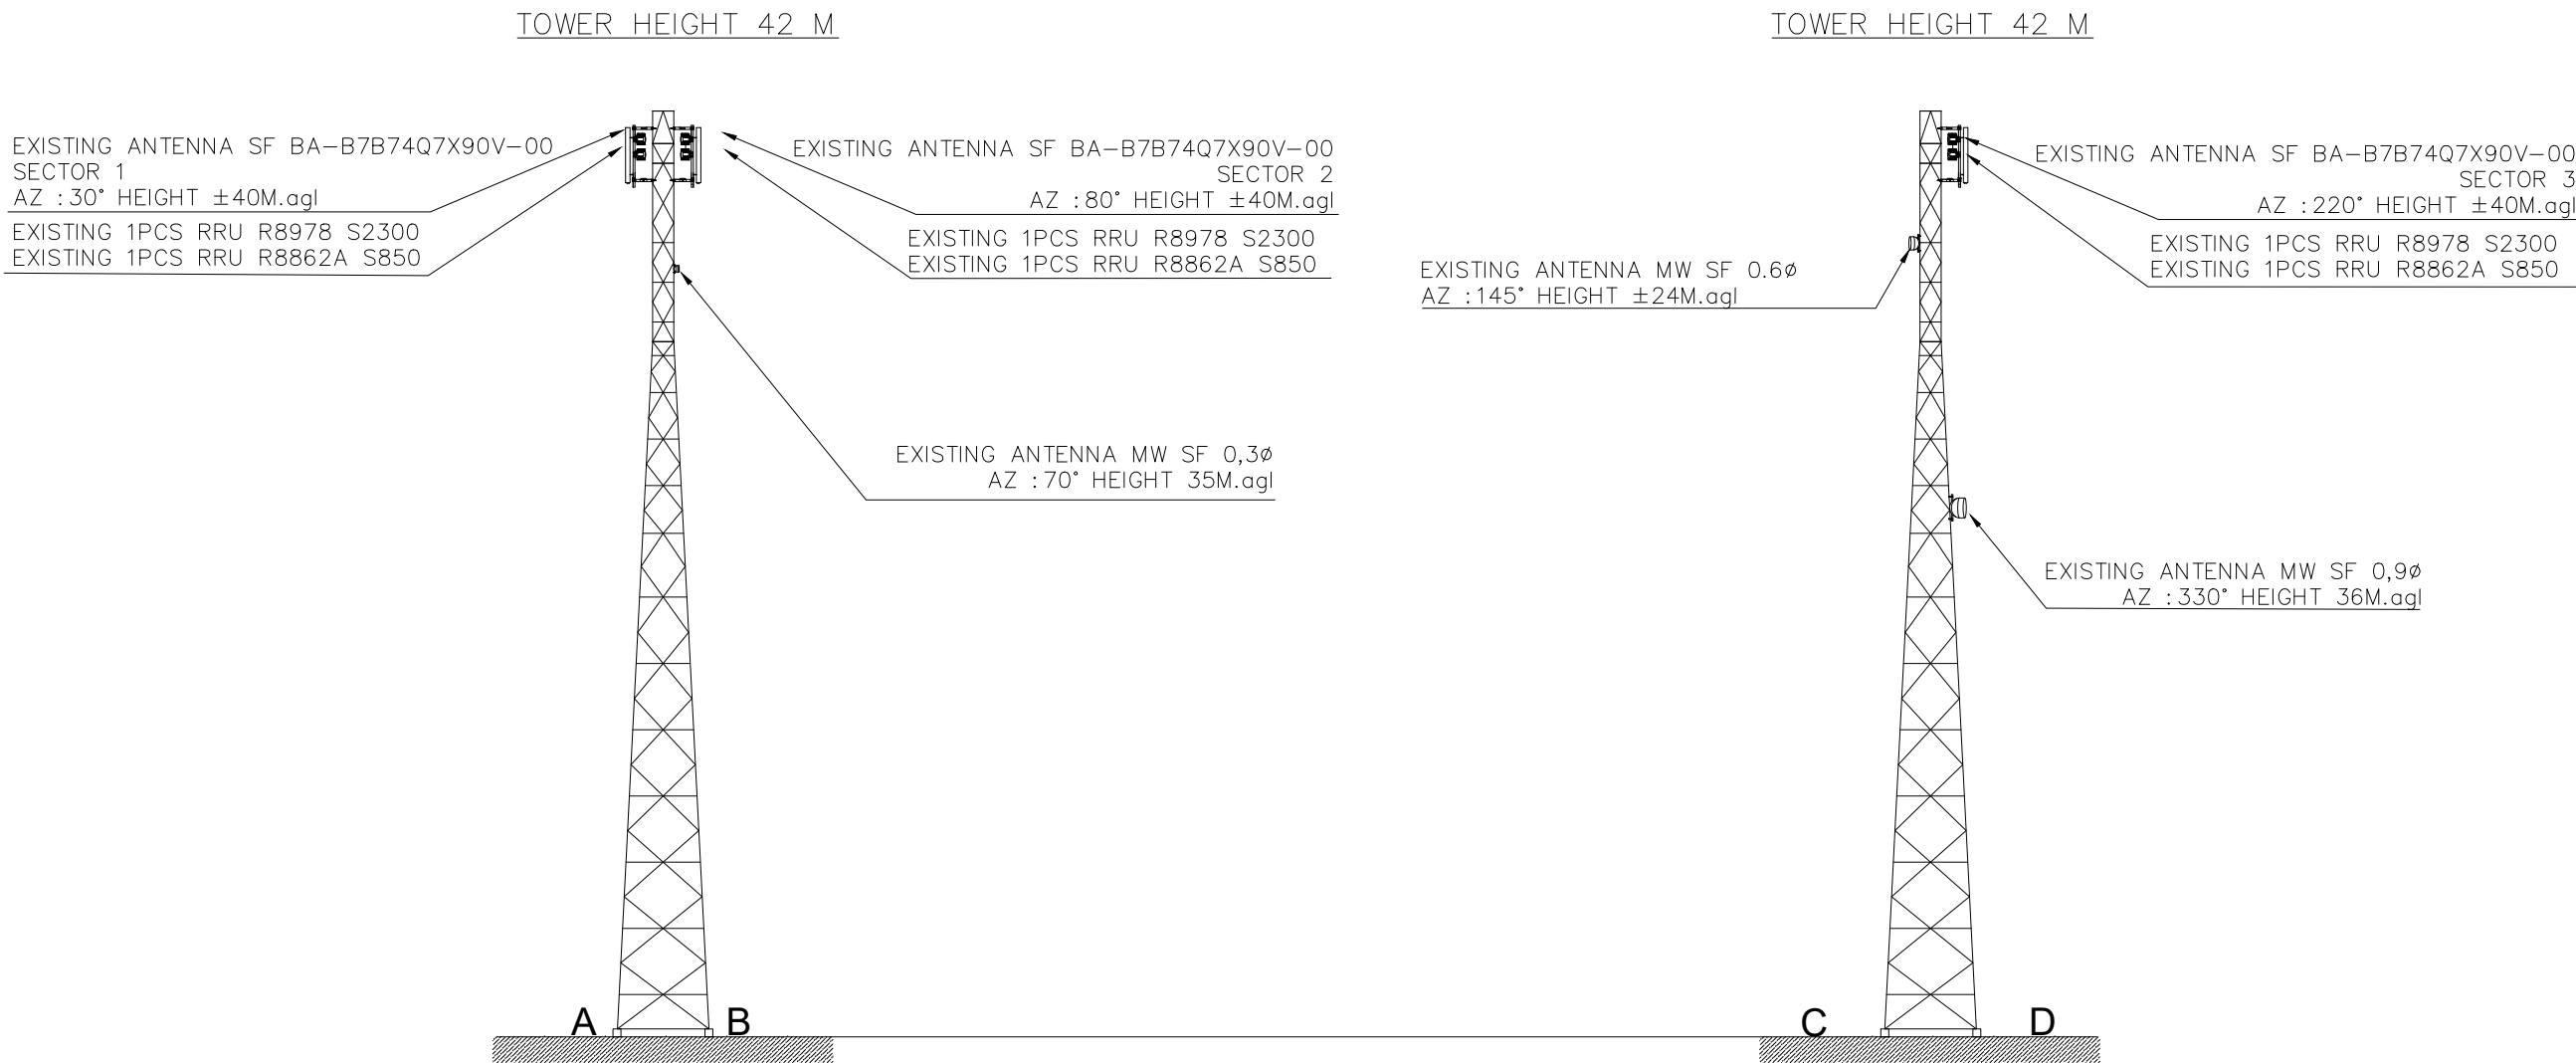

REMARKS

1. ALL DIMENSIONS ARE IN MILIMETER UNLESS NOTED ON THE DRAWING

2. ALL DIMENSIONS SHALL BE CONFIRMED ON SITES

APPROVED BY

CHECKED BY

 PT. HUAWEI TECH INVESTMENT

REGIONAL_PROJECT_MANAGER_AREA

CHECKED BY

DATE	REVISION	SIGN

THIS DOCUMENT AND ALL MATERIAL CONTAINED HEREIN IS PROTECTED BY COPYRIGHT, TRADEMARKS AND OTHER RIGHTS WHICH ARE OWNED AND/OR CONTROLLED BY PT INDOSAT AND/OR ITS AFFILIATES OR BY OTHER PARTIES THAT HAVE LICENSED THEIR MATERIAL TO ITS AFFILIATES

PROJECT NAME



DRAWING TITLE

SITE NAME	CIPARAY_MAJALAYA
SITE ID	ZBDG_4722
SCALE	
DRAWING BY	
CHECKED BY	
VERIFIED BY	
CONTRACT NO	
PROJECT NO	

DRAWING NUMBER	TOTAL DRAWING
PAGE NUMBER	TOTAL PAGE

E = EXISTING	EQUIPMENT								
	EQUIPMENT TYPE	NO	SEC	TYPE	SIZE	AZ	HEIGHT	POLE/LEG	FAR-END
E	RF ANTENNA (SF)	A01	1	BA-B7B74Q7X90V-00	-	30°	40,00 m	A	
E	RF ANTENNA (SF)	A02	2	BA-B7B74Q7X90V-00	-	80°	40,00 m	B	
E	RF ANTENNA (SF)	A03	3	BA-B7B74Q7X90V-00	-	220°	40,00 m	D	
E	RRU	A04	1	R8978 S2300	-		40,00 m	A	
E	RRU	A05	2	R8978 S2301	-		40,00 m	B	
E	RRU	A06	3	R8978 S2302	-		40,00 m	D	
E	RRU	A04	1	R8862A S850	-		40,00 m	A	
E	RRU	A05	2	R8862A S850	-		40,00 m	B	
E	RRU	A06	3	R8862A S850	-		40,00 m	D	
E	ANTENNA MW		1				35,00 m	B	
E	ANTENNA MW		2				24,00 m	C	
E	ANTENNA MW		3				36,00 m	D	

EXT. TOWER INFORMATION

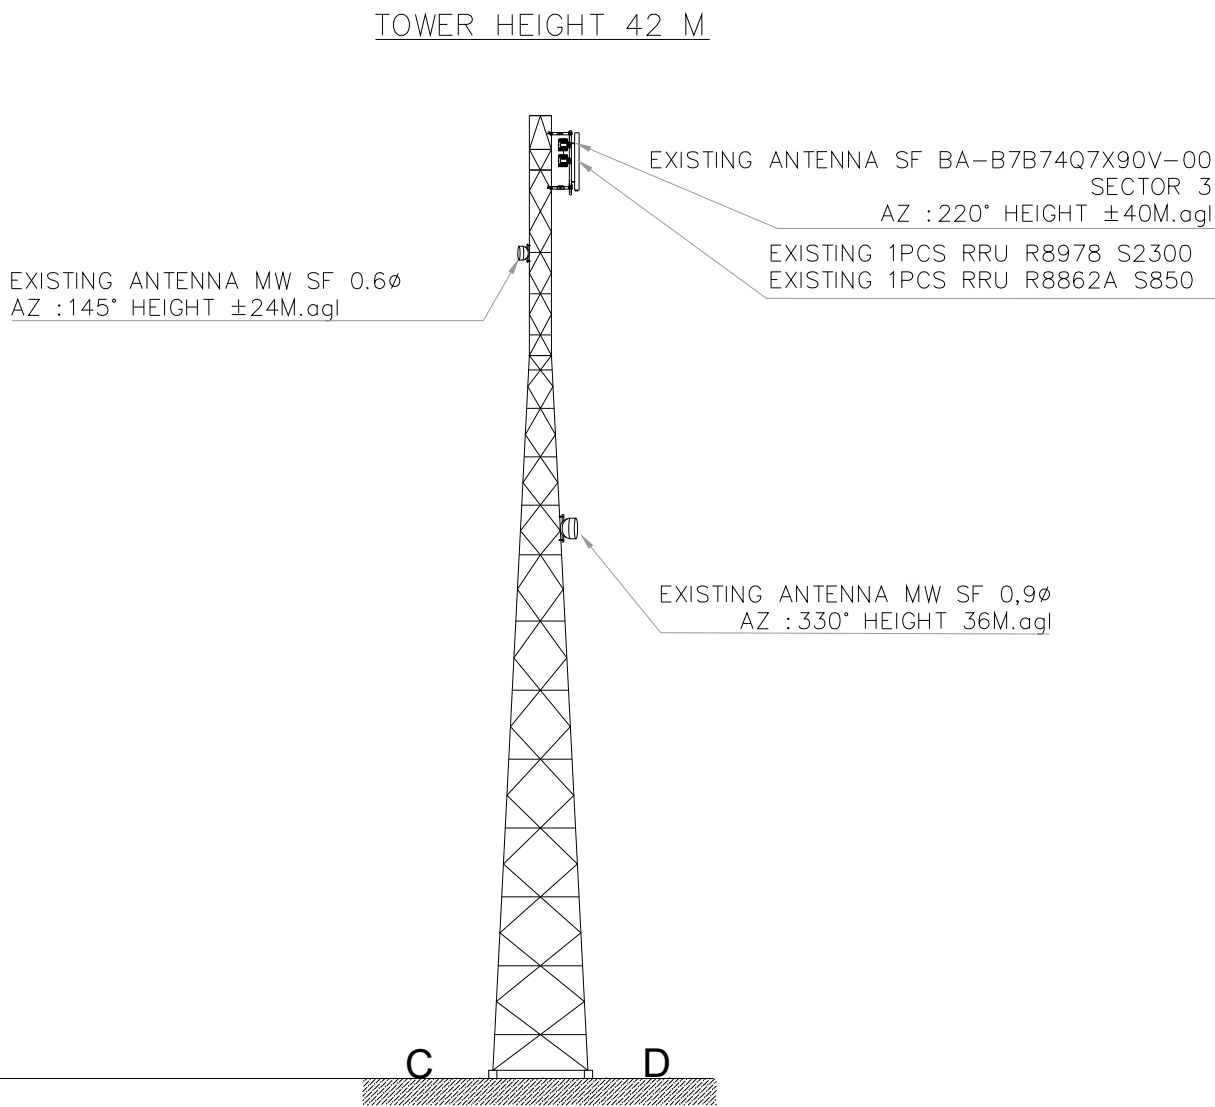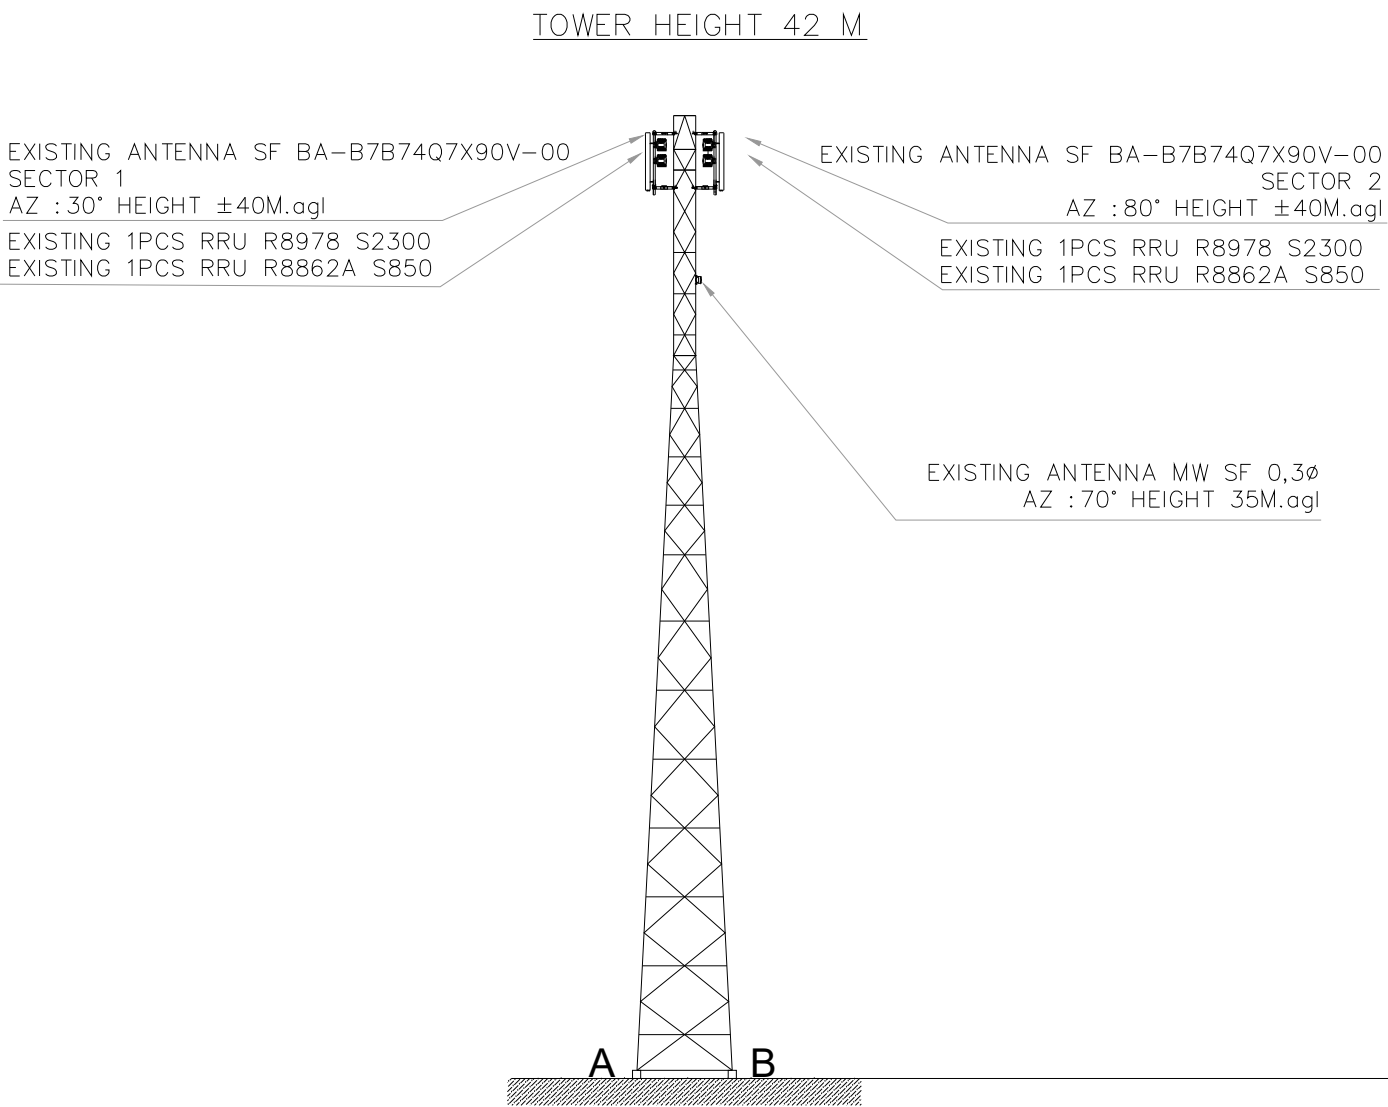

E = EXISTING	EQUIPMENT								
	EQUIPMENT TYPE	NO	SEC	TYPE	SIZE	AZ	HEIGHT	POLE/LEG	FAR-END
E	RF ANTENNA (SF)	A01	1	BA-B7B74Q7X90V-00	-	30°	40,00 m	A	
E	RF ANTENNA (SF)	A02	2	BA-B7B74Q7X90V-00	-	80°	40,00 m	B	
E	RF ANTENNA (SF)	A03	3	BA-B7B74Q7X90V-00	-	220°	40,00 m	D	
E	RRU	A04	1	R8978 S2300	-		40,00 m	A	
E	RRU	A05	2	R8978 S2301	-		40,00 m	B	
E	RRU	A06	3	R8978 S2302	-		40,00 m	D	
E	RRU	A04	1	R8862A S850	-		40,00 m	A	
E	RRU	A05	2	R8862A S850	-		40,00 m	B	
E	RRU	A06	3	R8862A S850	-		40,00 m	D	
E	ANTENNA MW		1				35,00 m	B	
E	ANTENNA MW		2				24,00 m	C	
E	ANTENNA MW		3				36,00 m	D	



PROP. TOWER INFORMATION

REMARKS

- ALL DIMENSIONS ARE IN MILIMETER UNLESS NOTED ON THE DRAWING
- ALL DIMENSIONS SHALL BE CONFIRMED ON SITES

APPROVED BY

CHECKED BY

PT. HUAWEI TECH INVESTMENT

REGIONAL_PROJECT_MANAGER_AREA

CHECKED BY


DATE	REVISION	SIGN

THIS DOCUMENT AND ALL MATERIAL CONTAINED HEREIN IS PROTECTED BY COPYRIGHT, TRADEMARKS AND OTHER RIGHTS WHICH ARE OWNED AND/OR CONTROLLED BY PT INDOSAT AND/OR ITS AFFILIATES OR BY OTHER PARTIES THAT HAVE LICENSED THEIR MATERIAL TO ITS AFFILIATES

PROJECT NAME

DRAWING TITLE

SITE NAME	CIPARAY_MAJALAYA
SITE ID	ZBDG_4722
SCALE	
DRAWING BY	
CHECKED BY	
VERIFIED BY	
CONTRACT NO	
PROJECT NO	
DRAWING NUMBER	TOTAL DRAWING
PAGE NUMBER	TOTAL PAGE

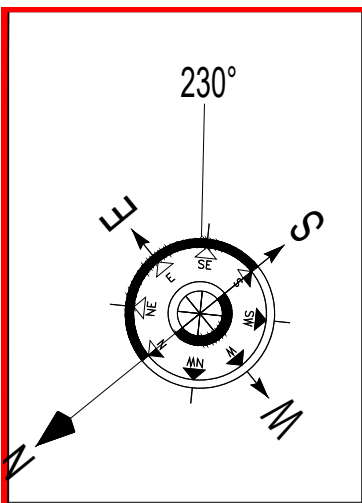


EXISTING ANTENNA SF BA-B7B74Q7X90V-00
SECTOR 3
AZ : 220° HEIGHT ±40M.agl

EXISTING 1PCS RRU R8978 S2300
EXISTING 1PCS RRU R8862A S850

EXISTING ANTENNA SF BA-B7B74Q7X90V-00
SECTOR 1
AZ : 30° HEIGHT ±40M.agl

EXISTING 1PCS RRU R8978 S2300
EXISTING 1PCS RRU R8862A S850

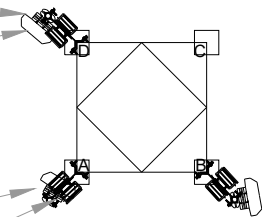

EXISTING ANTENNA SF BA-B7B74Q7X90V-00
SECTOR 2
AZ : 80° HEIGHT ±40M.agl

EXISTING 1PCS RRU R8978 S2300
EXISTING 1PCS RRU R8862A S850

REMARKS

- 1. ALL DIMENSIONS ARE IN MILIMETER UNLESS NOTED ON THE DRAWING
- 2. ALL DIMENSIONS SHALL BE CONFIRMED ON SITES

APPROVED BY

CHECKED BY



REGIONAL_PROJECT_MANAGER_AREA

CHECKED BY

DATE	REVISION	SIGN


THIS DOCUMENT AND ALL MATERIAL CONTAINED HEREIN IS PROTECTED BY COPYRIGHT, TRADEMARKS AND OTHER RIGHTS WHICH ARE OWNED AND/OR CONTROLLED BY PT INDOSAT AND/OR ITS AFFILIATES OR BY OTHER PARTIES THAT HAVE LICENSED THEIR MATERIAL TO ITS AFFILIATES

PROJECT NAME

DRAWING TITLE

SITE NAME	CIPARAY_MAJALAYA
SITE ID	ZBDG_4722
SCALE	
DRAWING BY	
CHECKED BY	
VERIFIED BY	
CONTRACT NO	
PROJECT NO	

DRAWING NUMBER	TOTAL DRAWING
PAGE NUMBER	TOTAL PAGE

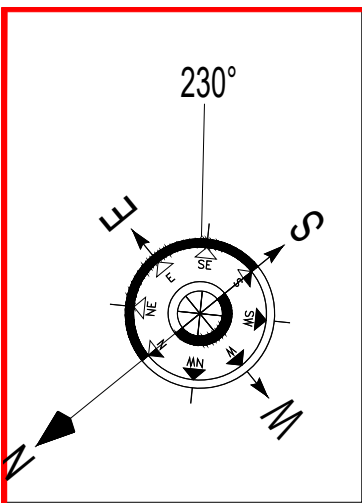


EXISTING ANTENNA SF BA-B7B74Q7X90V-00
SECTOR 3
AZ : 220° HEIGHT ±40M.agl

EXISTING 1PCS RRU R8978 S2300
EXISTING 1PCS RRU R8862A S850

EXISTING ANTENNA SF BA-B7B74Q7X90V-00
SECTOR 1
AZ : 30° HEIGHT ±40M.agl

EXISTING 1PCS RRU R8978 S2300
EXISTING 1PCS RRU R8862A S850

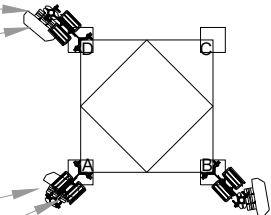

EXISTING ANTENNA SF BA-B7B74Q7X90V-00
SECTOR 2
AZ : 80° HEIGHT ±40M.agl


EXISTING 1PCS RRU R8978 S2300
EXISTING 1PCS RRU R8862A S850

REMARKS

- 1. ALL DIMENSIONS ARE IN MILIMETER UNLESS NOTED ON THE DRAWING
- 2. ALL DIMENSIONS SHALL BE CONFIRMED ON SITES

APPROVED BY

CHECKED BY

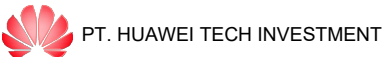

REGIONAL_PROJECT_MANAGER_AREA

CHECKED BY

DATE	REVISION	SIGN


THIS DOCUMENT AND ALL MATERIAL CONTAINED HEREIN IS PROTECTED BY COPYRIGHT, TRADEMARKS AND OTHER RIGHTS WHICH ARE OWNED AND/OR CONTROLLED BY PT INDOSAT AND/OR ITS AFFILIATES OR BY OTHER PARTIES THAT HAVE LICENSED THEIR MATERIAL TO ITS AFFILIATES

PROJECT NAME

DRAWING TITLE

SITE NAME	CIPARAY_MAJALAYA
SITE ID	ZBDG_4722
SCALE	
DRAWING BY	
CHECKED BY	
VERIFIED BY	
CONTRACT NO	
PROJECT NO	


DRAWING NUMBER	TOTAL DRAWING
PAGE NUMBER	TOTAL PAGE

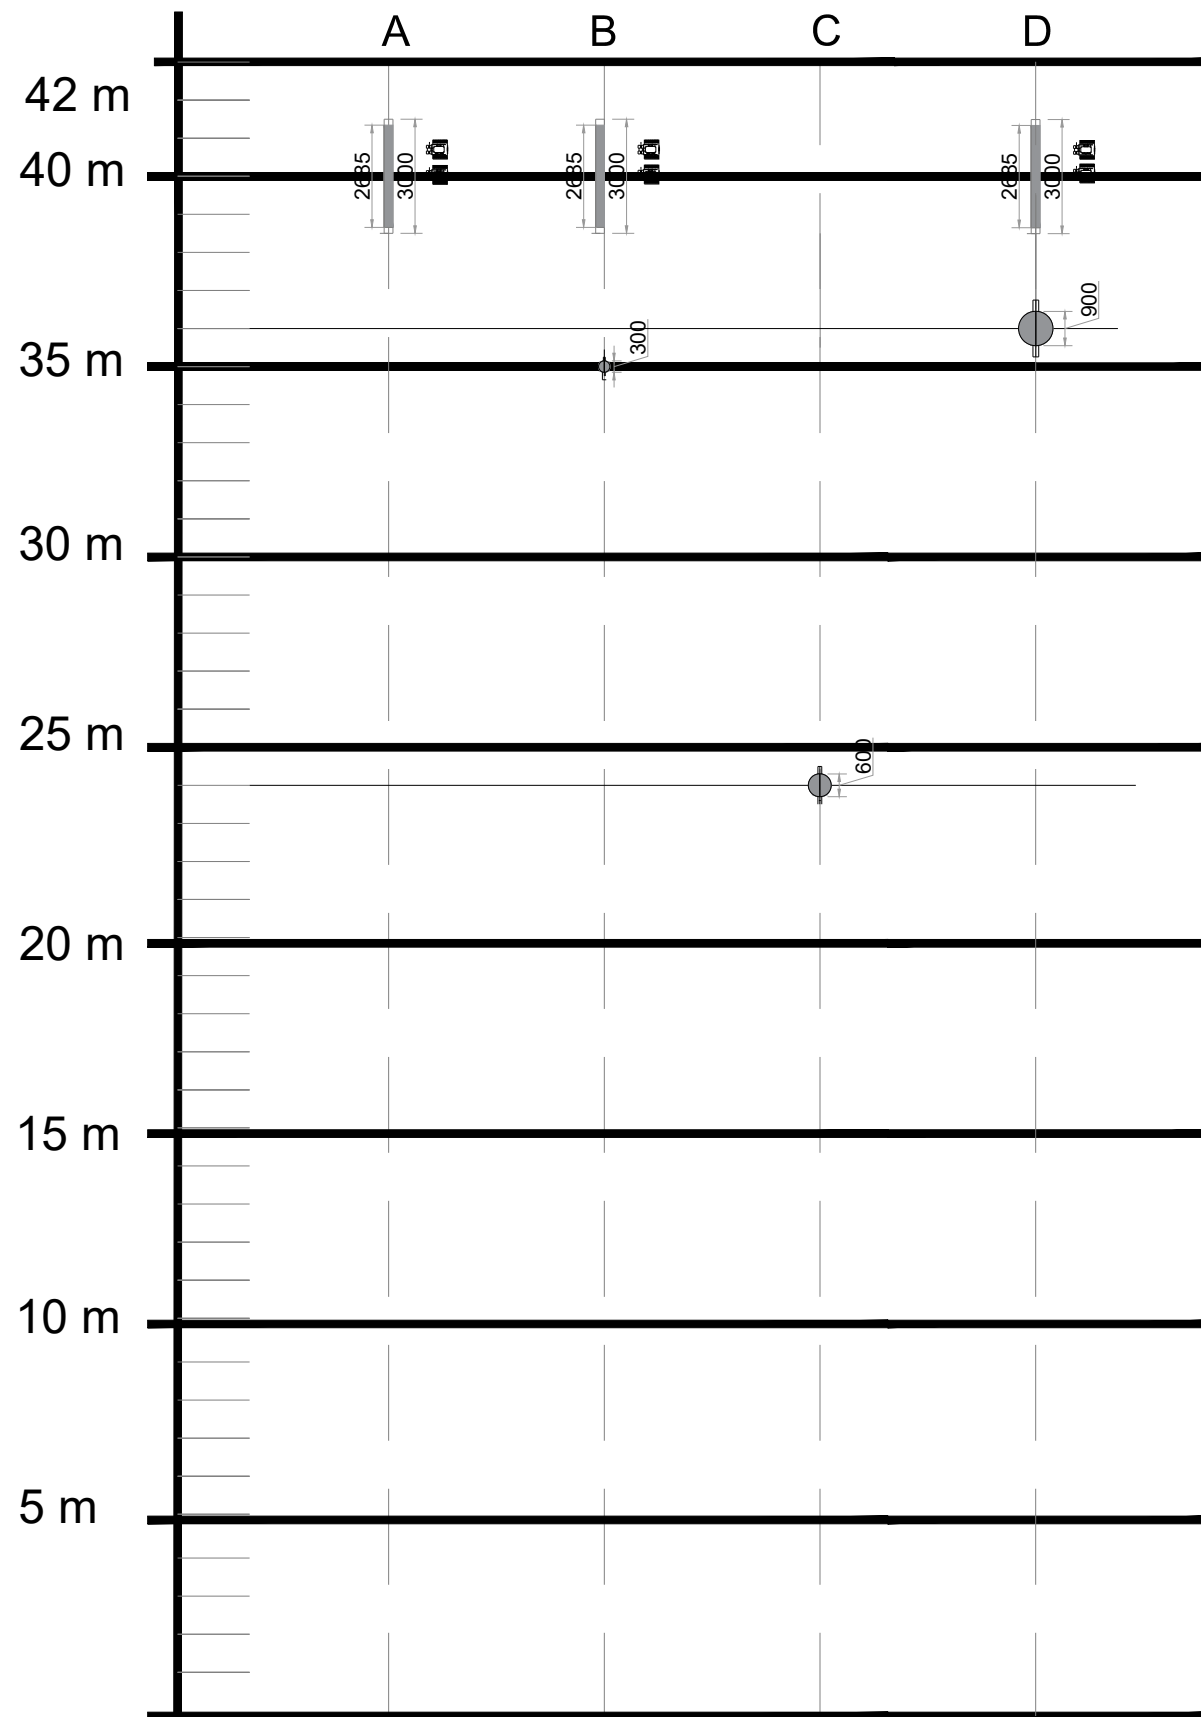

SST 4 LEG 42 METER

TOWER LEG ID
(CLOCKWISE FROM NORTH DIRECTION)

COLOR LEGENDS

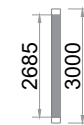

EXISTING RF ANTENNA SF (ex-IO)



EXISTING RRU SF



EXISTING MW ANTENNA SF 0.3Ø (ex-IO)



EXISTING MW ANTENNA SF 0.6Ø (ex-IO)



EXISTING MW ANTENNA SF 0.9Ø (ex-IO)

REMARKS

- ALL DIMENSIONS ARE IN MILIMETER UNLESS NOTED ON THE DRAWING
- ALL DIMENSIONS SHALL BE CONFIRMED ON SITES

APPROVED BY

CHECKED BY



PT. HUAWEI TECH INVESTMENT

REGIONAL_PROJECT_MANAGER_AREA

CHECKED BY


DATE	REVISION	SIGN

THIS DOCUMENT AND ALL MATERIAL CONTAINED HEREIN IS PROTECTED BY COPYRIGHT, TRADEMARKS AND OTHER RIGHTS WHICH ARE OWNED AND/OR CONTROLLED BY PT INDOSAT AND/OR ITS AFFILIATES OR BY OTHER PARTIES THAT HAVE LICENSED THEIR MATERIAL TO ITS AFFILIATES

PROJECT NAME

DRAWING TITLE


SITE NAME	CIPARAY_MAJALAYA
SITE ID	ZBDG_4722
SCALE	
DRAWING BY	
CHECKED BY	
VERIFIED BY	
CONTRACT NO	
PROJECT NO	
DRAWING NUMBER	TOTAL DRAWING
PAGE NUMBER	TOTAL PAGE

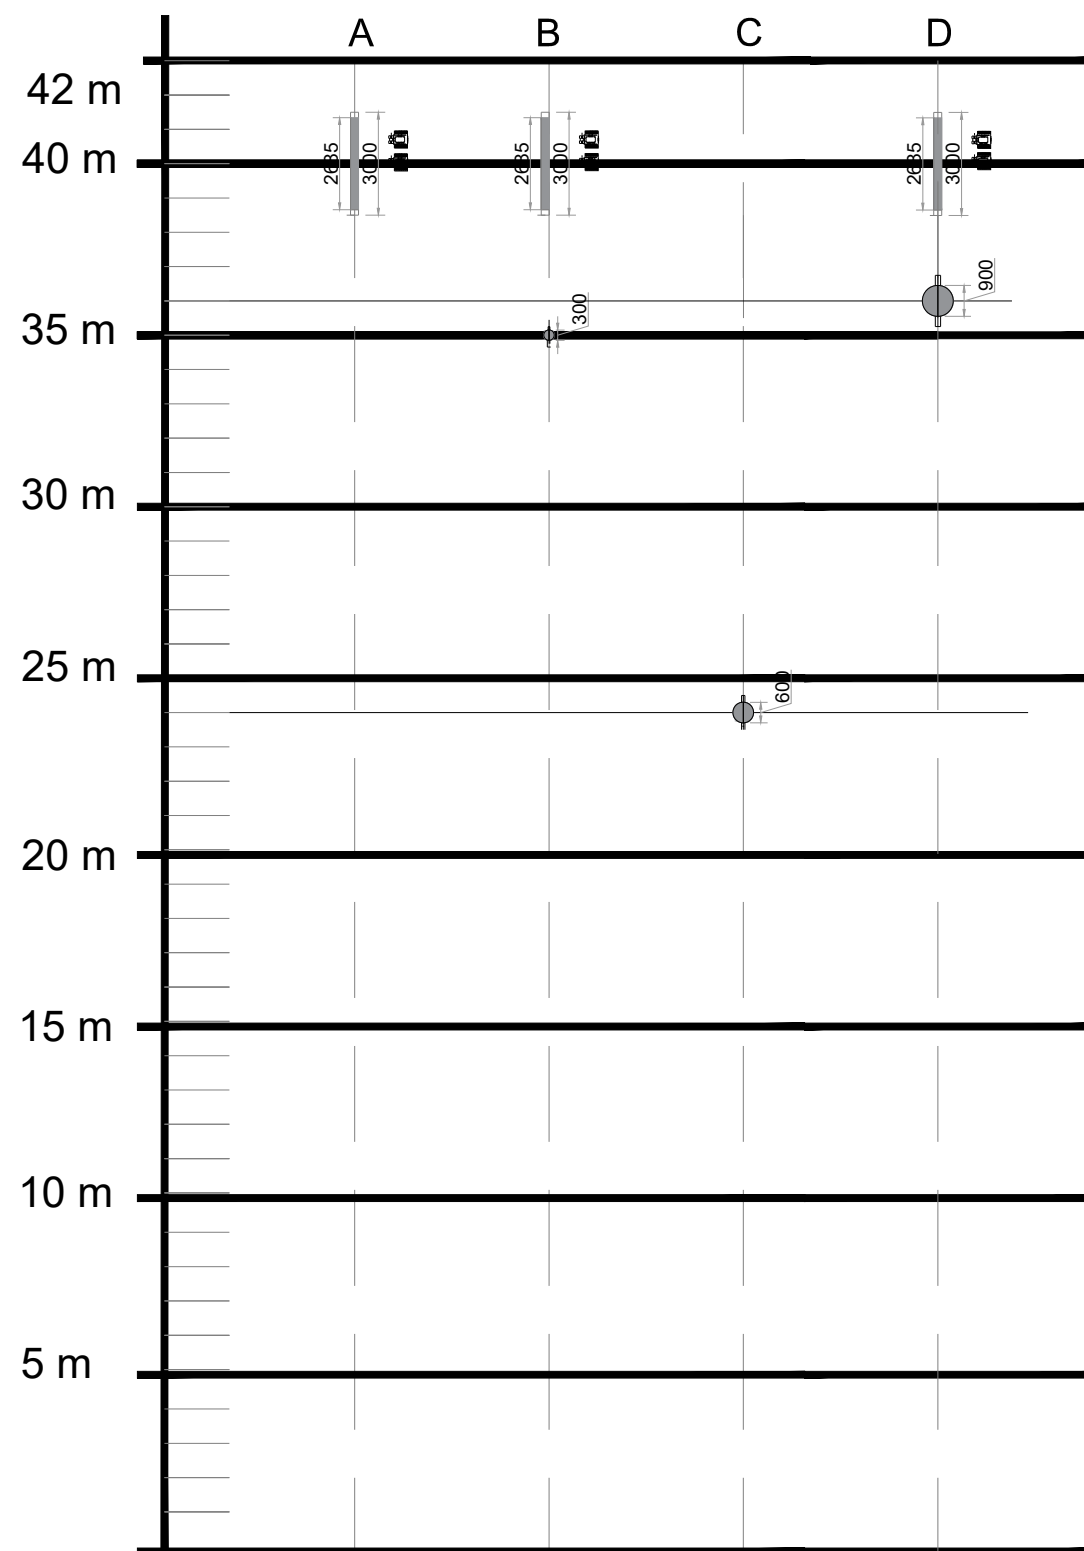

SST 4 LEG 42 METER

TOWER LEG ID
(CLOCKWISE FROM NORTH DIRECTION)

COLOR LEGENDS

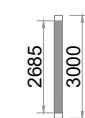

EXISTING RF ANTENNA SF (ex-IO)



EXISTING RRU SF



EXISTING MW ANTENNA SF 0.3Ø (ex-IO)



EXISTING MW ANTENNA SF 0.6Ø (ex-IO)



EXISTING MW ANTENNA SF 0.9Ø (ex-IO)

REMARKS

1. ALL DIMENSIONS ARE IN MILIMETER UNLESS NOTED ON THE DRAWING
2. ALL DIMENSIONS SHALL BE CONFIRMED ON SITES

APPROVED BY

CHECKED BY



PT. HUAWEI TECH INVESTMENT

REGIONAL_PROJECT_MANAGER_AREA

CHECKED BY

DATE	REVISION	SIGN

THIS DOCUMENT AND ALL MATERIAL CONTAINED HEREIN IS PROTECTED BY COPYRIGHT, TRADEMARKS AND OTHER RIGHTS WHICH ARE OWNED AND/OR CONTROLLED BY PT INDOSAT AND/OR ITS AFFILIATES OR BY OTHER PARTIES THAT HAVE LICENSED THEIR MATERIAL TO ITS AFFILIATES

PROJECT NAME

DRAWING TITLE

SITE NAME	CIPARAY_MAJALAYA
SITE ID	ZBDG_4722
SCALE	
DRAWING BY	
CHECKED BY	
VERIFIED BY	
CONTRACT NO	
PROJECT NO	

DRAWING NUMBER	TOTAL DRAWING
----------------	---------------

--	--

PAGE NUMBER	TOTAL PAGE
-------------	------------

--	--