
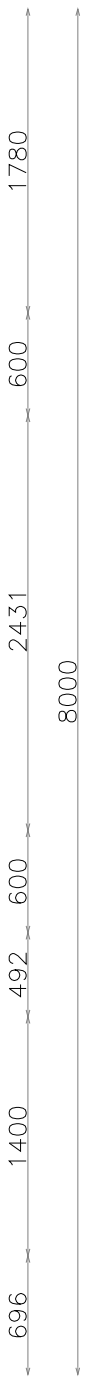
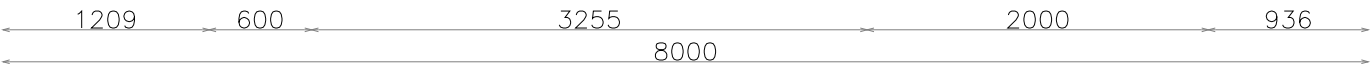
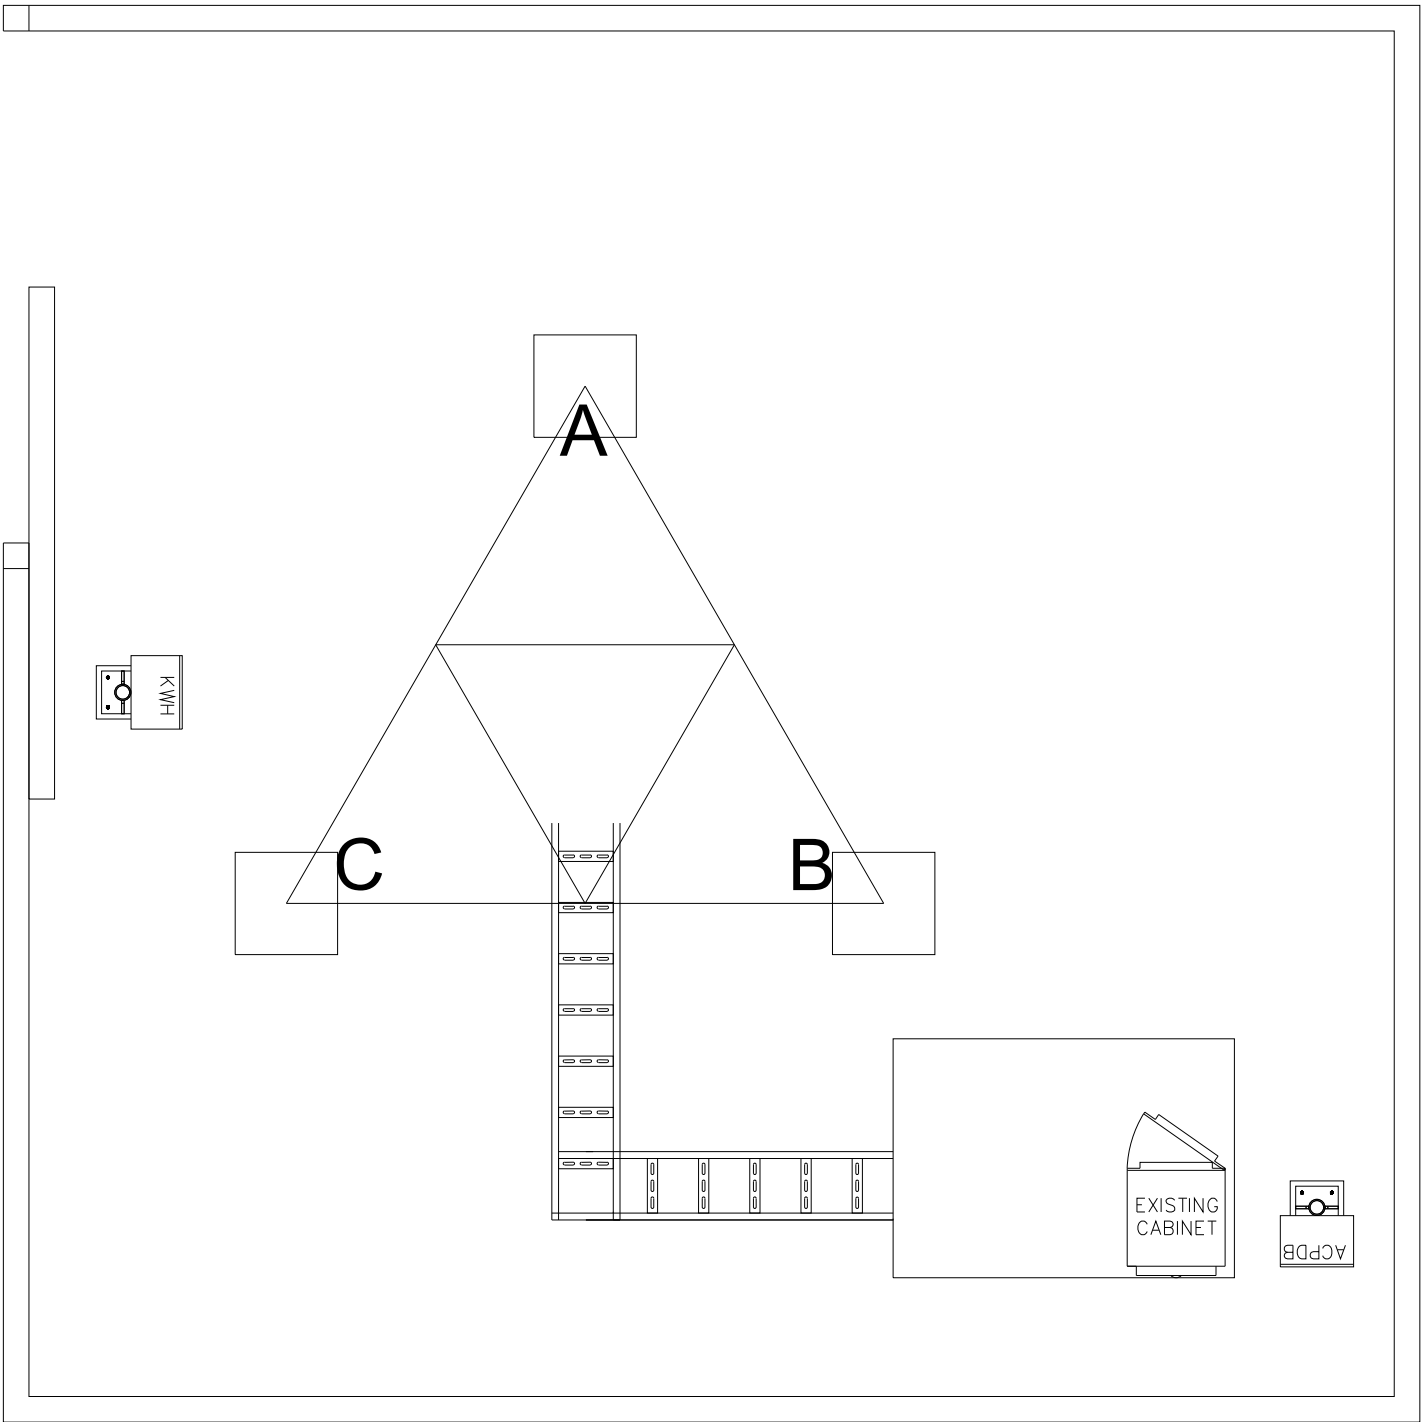
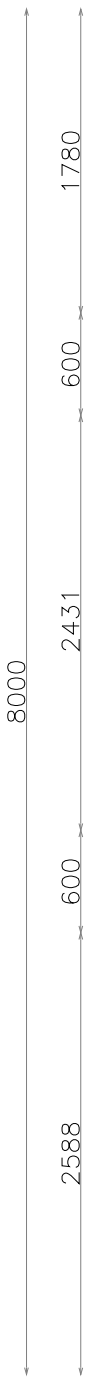
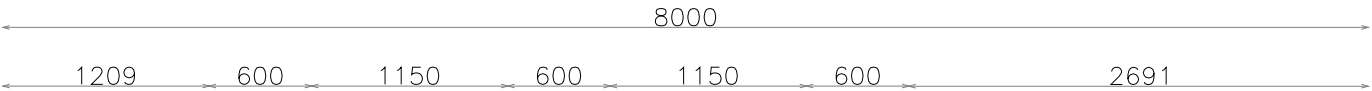


- PROPOSED POWER CABLE
- PROPOSED POWER CABLE
- PROPOSED GROUNDING C
- PROPOSED HYBRID CABLE
- PROPOSED OPTICAL CABL
- COAXIAL CABLE
- EXISTING FEEDER
- EXISTING JUMPER
- PROPOSED JUMPER
- PROPOSED CABINET
- DISMANTLE EQUIPMENT
- EXISTING EQUIPMENT

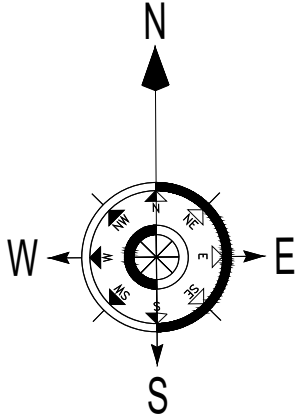

REMARKS

1. ALL DIMENSIONS ARE IN MILIMETER UNLESS NOTED ON THE DRAWING
2. ALL DIMENSIONS SHALL BE CONFIRMED ON SITES

APPROVED BY

CHECKED BY



REGIONAL_PROJECT_MANAGER_AREA

CHECKED BY

DATE	REVISION	SIGN

THIS DOCUMENT AND ALL MATERIAL CONTAINED HEREIN IS PROTECTED BY COPYRIGHT, TRADEMARKS AND OTHER RIGHTS WHICH ARE OWNED AND/OR CONTROLLED BY PT INDOSAT AND/OR ITS AFFILIATES OR BY OTHER PARTIES THAT HAVE LICENSED THEIR MATERIAL TO ITS AFFILIATES

PROJECT NAME

DRAWING TITLE

SITE NAME	CIKASUNGKA_CIKANCUNG
SITE ID	ZBDG_6379
SCALE	
DRAWING BY	
CHECKED BY	
VERIFIED BY	
CONTRACT NO	
PROJECT NO	

DRAWING NUMBER	TOTAL DRAWING
PAGE NUMBER	TOTAL PAGE

PROPOSED POWER CABLE

PROPOSED POWER CABLE

PROPOSED GROUNDING C

PROPOSED HYBRID CABLE

PROPOSED OPTICAL CABL

COAXIAL CABLE

EXISTING FEEDER


EXISTING JUMPER

PROPOSED JUMPER

PROPOSED CABINET

DISMANTLE EQUIPMENT

EXISTING EQUIPMENT

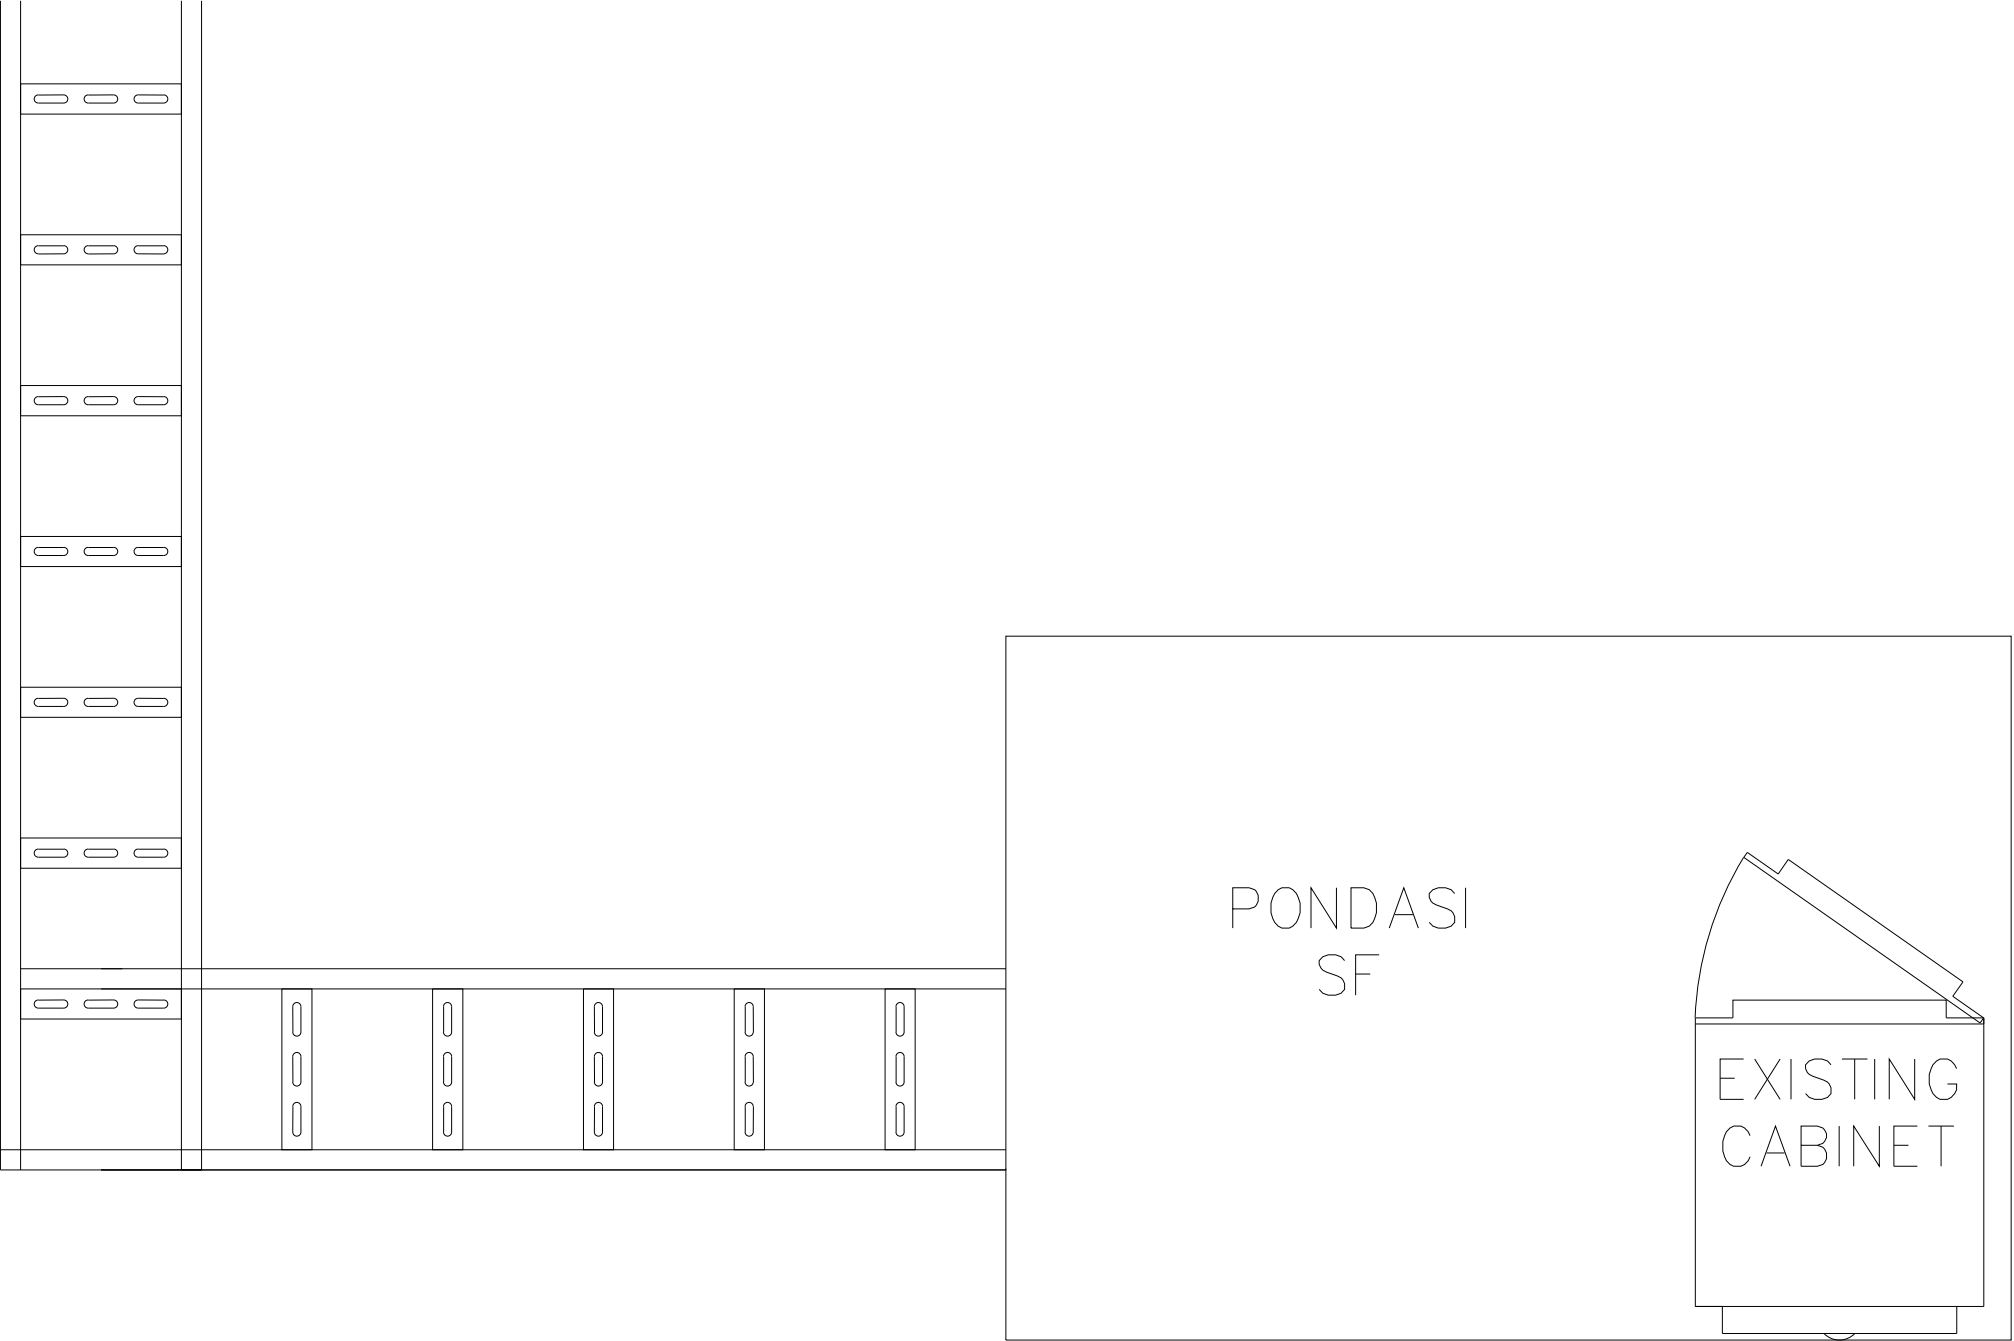

REMARKS

1. ALL DIMENSIONS ARE IN MILIMETER UNLESS NOTED ON THE DRAWING

2. ALL DIMENSIONS SHALL BE CONFIRMED ON SITES

APPROVED BY

CHECKED BY

 PT. HUAWEI TECH INVESTMENT

REGIONAL_PROJECT_MANAGER_AREA

CHECKED BY

DATE	REVISION	SIGN

THIS DOCUMENT AND ALL MATERIAL CONTAINED HEREIN IS PROTECTED BY COPYRIGHT, TRADEMARKS AND OTHER RIGHTS WHICH ARE OWNED AND/OR CONTROLLED BY PT INDOSAT AND/OR ITS AFFILIATES OR BY OTHER PARTIES THAT HAVE LICENSED THEIR MATERIAL TO ITS AFFILIATES

PROJECT NAME

DRAWING TITLE

SITE NAME	CIKASUNGKA_CIKANCUNG
SITE ID	ZBDG_6379
SCALE	
DRAWING BY	
CHECKED BY	
VERIFIED BY	
CONTRACT NO	
PROJECT NO	

DRAWING NUMBER	TOTAL DRAWING
PAGE NUMBER	TOTAL PAGE

PROPOSED POWER CABLE

PROPOSED POWER CABLE

PROPOSED GROUNDING C

PROPOSED HYBRID CABLE

PROPOSED OPTICAL CABL

COAXIAL CABLE

EXISTING FEEDER



EXISTING JUMPER

PROPOSED JUMPER

PROPOSED CABINET

DISMANTLE EQUIPMENT

EXISTING EQUIPMENT

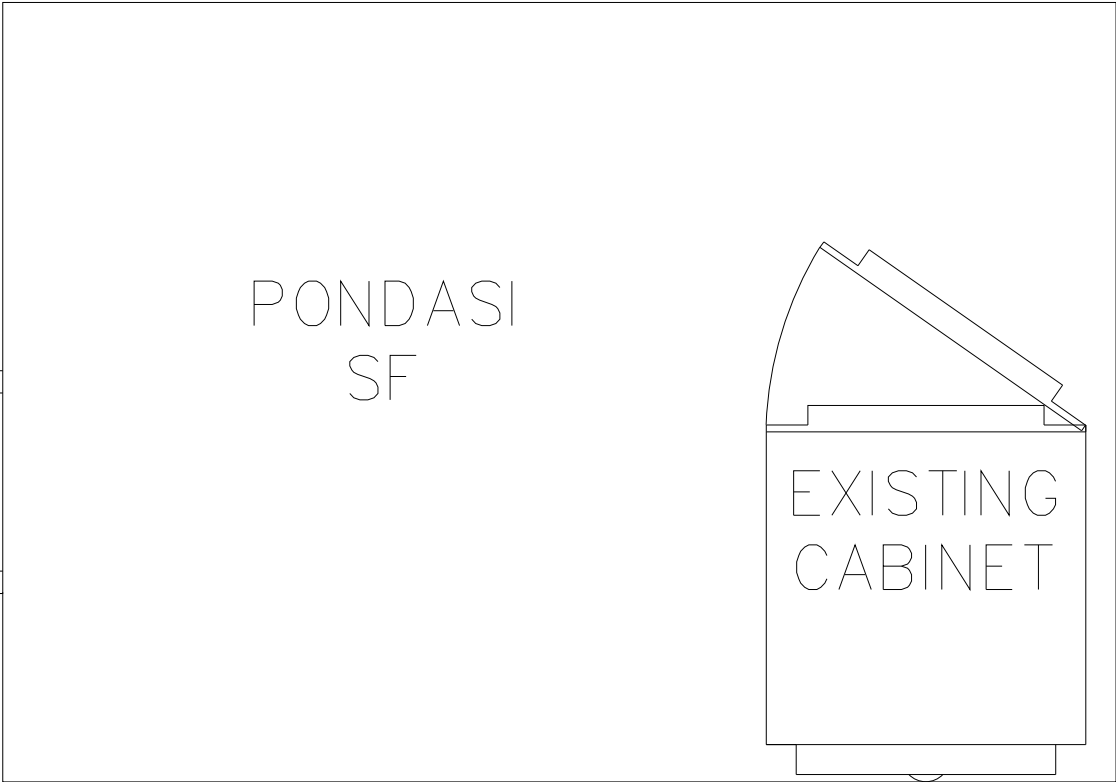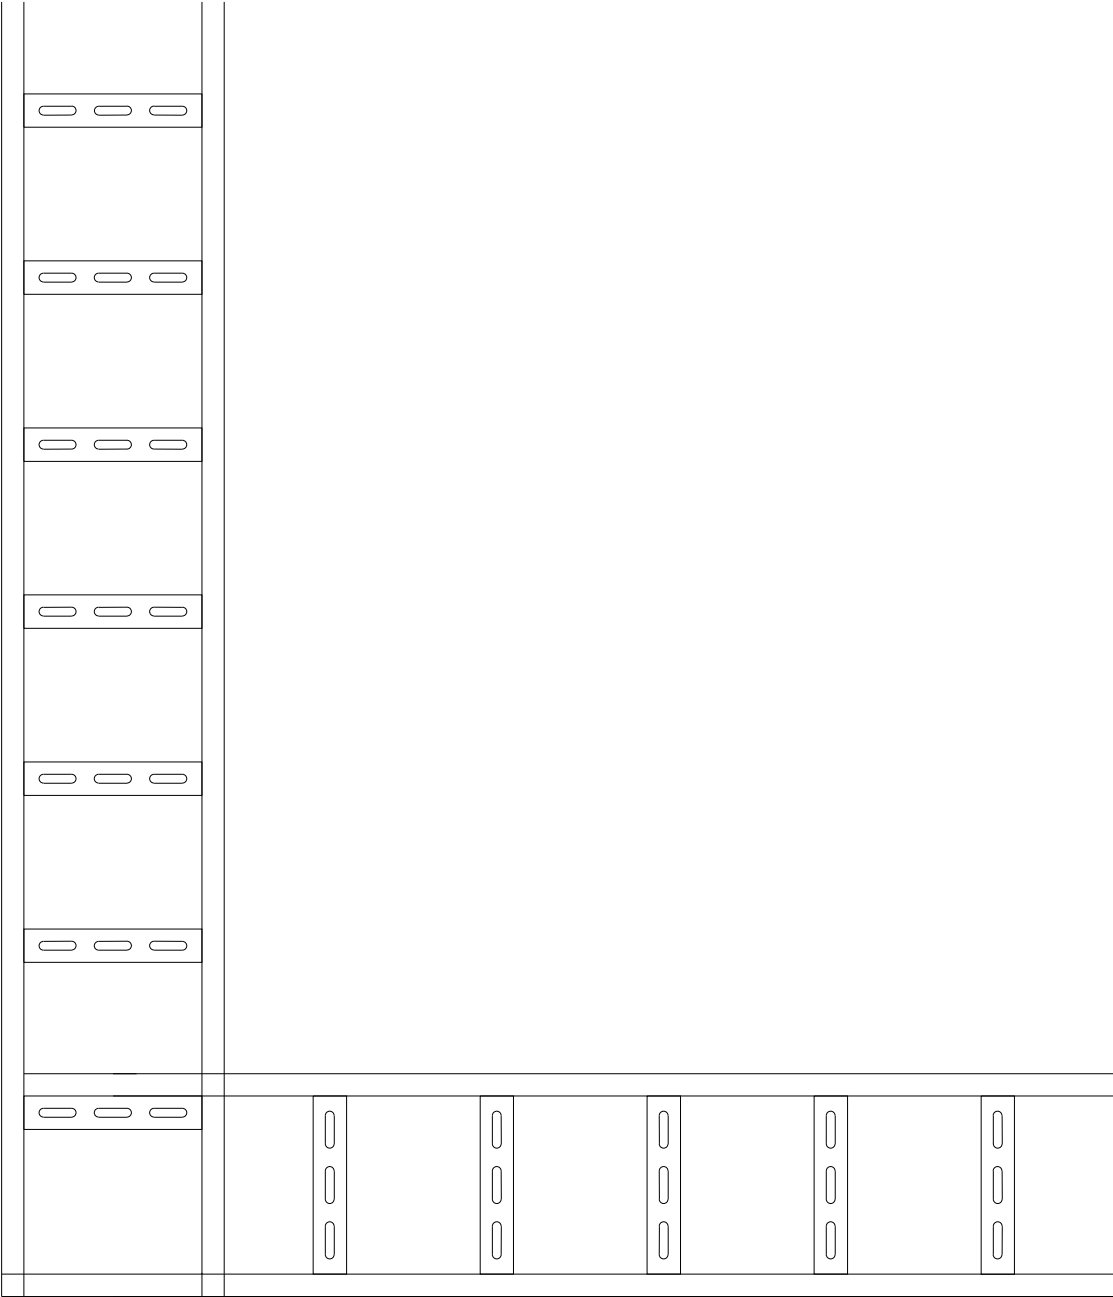

REMARKS

1. ALL DIMENSIONS ARE IN MILIMETER UNLESS NOTED ON THE DRAWING
2. ALL DIMENSIONS SHALL BE CONFIRMED ON SITES

APPROVED BY

CHECKED BY



REGIONAL_PROJECT_MANAGER_AREA

CHECKED BY

DATE	REVISION	SIGN

THIS DOCUMENT AND ALL MATERIAL CONTAINED HEREIN IS PROTECTED BY COPYRIGHT, TRADEMARKS AND OTHER RIGHTS WHICH ARE OWNED AND/OR CONTROLLED BY PT INDOSAT AND/OR ITS AFFILIATES OR BY OTHER PARTIES THAT HAVE LICENSED THEIR MATERIAL TO ITS AFFILIATES

PROJECT NAME


DRAWING TITLE

SITE NAME	CIKASUNGKA_CIKANCUNG
SITE ID	ZBDG_6379
SCALE	
DRAWING BY	
CHECKED BY	
VERIFIED BY	
CONTRACT NO	
PROJECT NO	

DRAWING NUMBER	TOTAL DRAWING
PAGE NUMBER	TOTAL PAGE

TOWER HEIGHT 45 M

TOWER HEIGHT 45 M

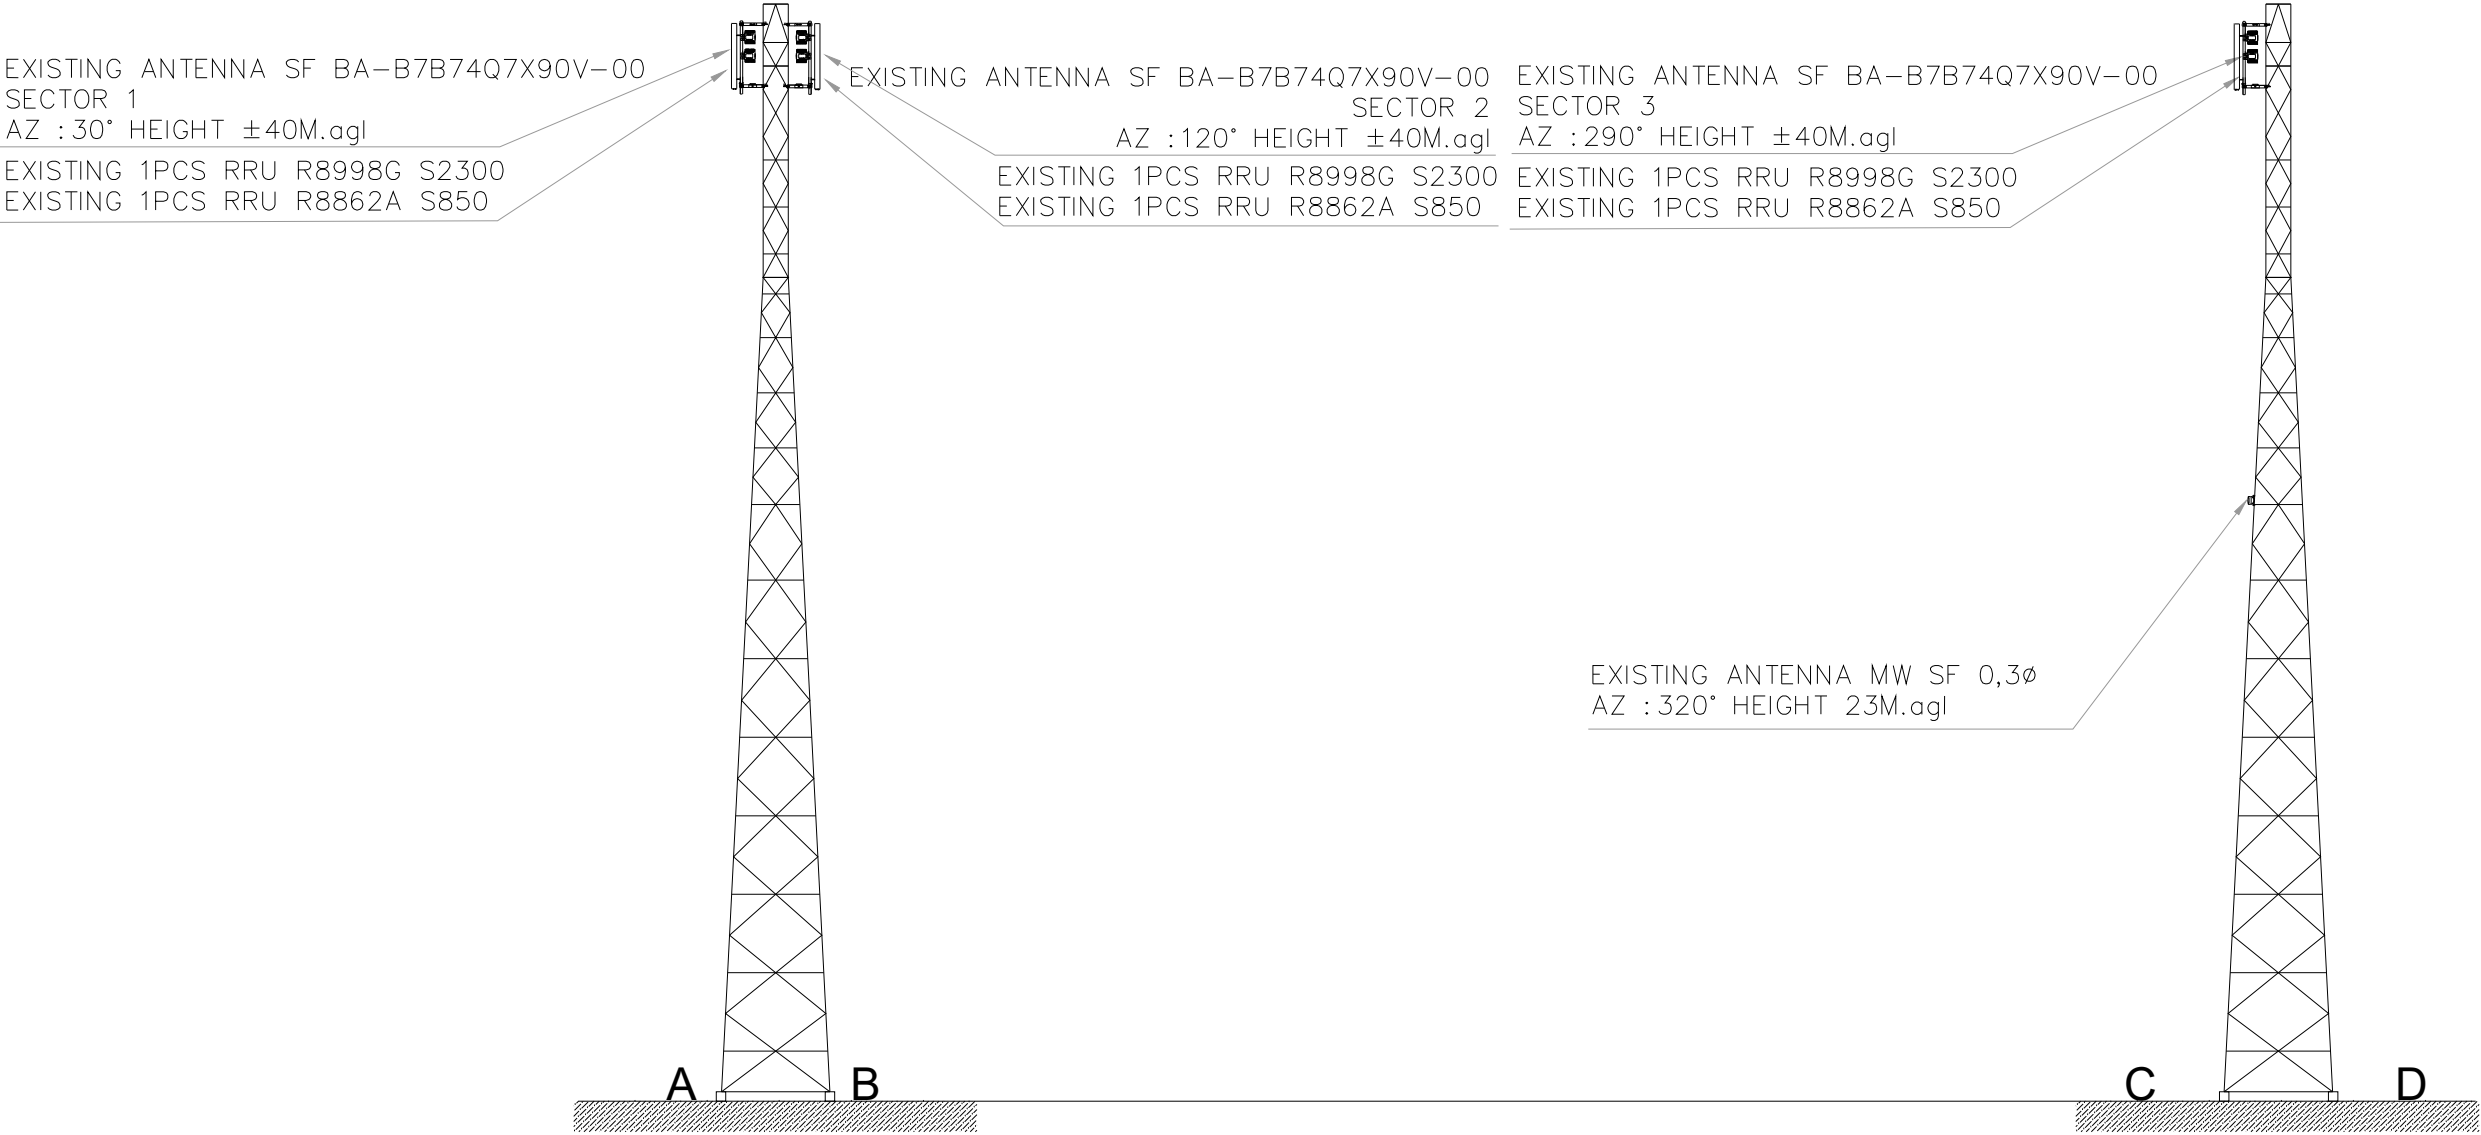

REMARKS

1. ALL DIMENSIONS ARE IN MILIMETER UNLESS NOTED ON THE DRAWING
2. ALL DIMENSIONS SHALL BE CONFIRMED ON SITES

APPROVED BY

CHECKED BY



PT. HUAWEI TECH INVESTMENT

REGIONAL_PROJECT_MANAGER_AREA

CHECKED BY

DATE	REVISION	SIGN

THIS DOCUMENT AND ALL MATERIAL CONTAINED HEREIN IS PROTECTED BY COPYRIGHT, TRADEMARKS AND OTHER RIGHTS WHICH ARE OWNED AND/OR CONTROLLED BY PT INDOSAT AND/OR ITS AFFILIATES OR BY OTHER PARTIES THAT HAVE LICENSED THEIR MATERIAL TO ITS AFFILIATES


PROJECT NAME

DRAWING TITLE

SITE NAME	CIKASUNGKA_CIKANCUNG
SITE ID	ZBDG_6379
SCALE	
DRAWING BY	
CHECKED BY	
VERIFIED BY	
CONTRACT NO	
PROJECT NO	
DRAWING NUMBER	TOTAL DRAWING
PAGE NUMBER	TOTAL PAGE

E = EXISTING	EQUIPMENT								
	EQUIPMENT TYPE	NO	SEC	TYPE	SIZE	AZ	HEIGHT	POLE/LEG	FAR-END
E	RF ANTENNA (SF)	A01	1	BA-B7B74Q7X90V-00	-	30°	40,00 m	A	
E	RF ANTENNA (SF)	A02	2	BA-B7B74Q7X90V-00	-	120°	40,00 m	B	
E	RF ANTENNA (SF)	A03	3	BA-B7B74Q7X90V-00	-	290°	40,00 m	C	
E	RRU		1	RRU R8862A S850			40,00 m	A	
E	RRU		2	RRU R8862A S850			40,00 m	B	
E	RRU		3	RRU R8862A S850			40,00 m	C	
E	RRU		1	RRU R8998G S2300			40,00 m	A	
E	RRU		2	RRU R8998G S2300			40,00 m	B	
E	RRU		3	RRU R8998G S2300			40,00 m	C	
E	ANTENNA MW		1	TYA03U023D 0,3			23,00 m	C	



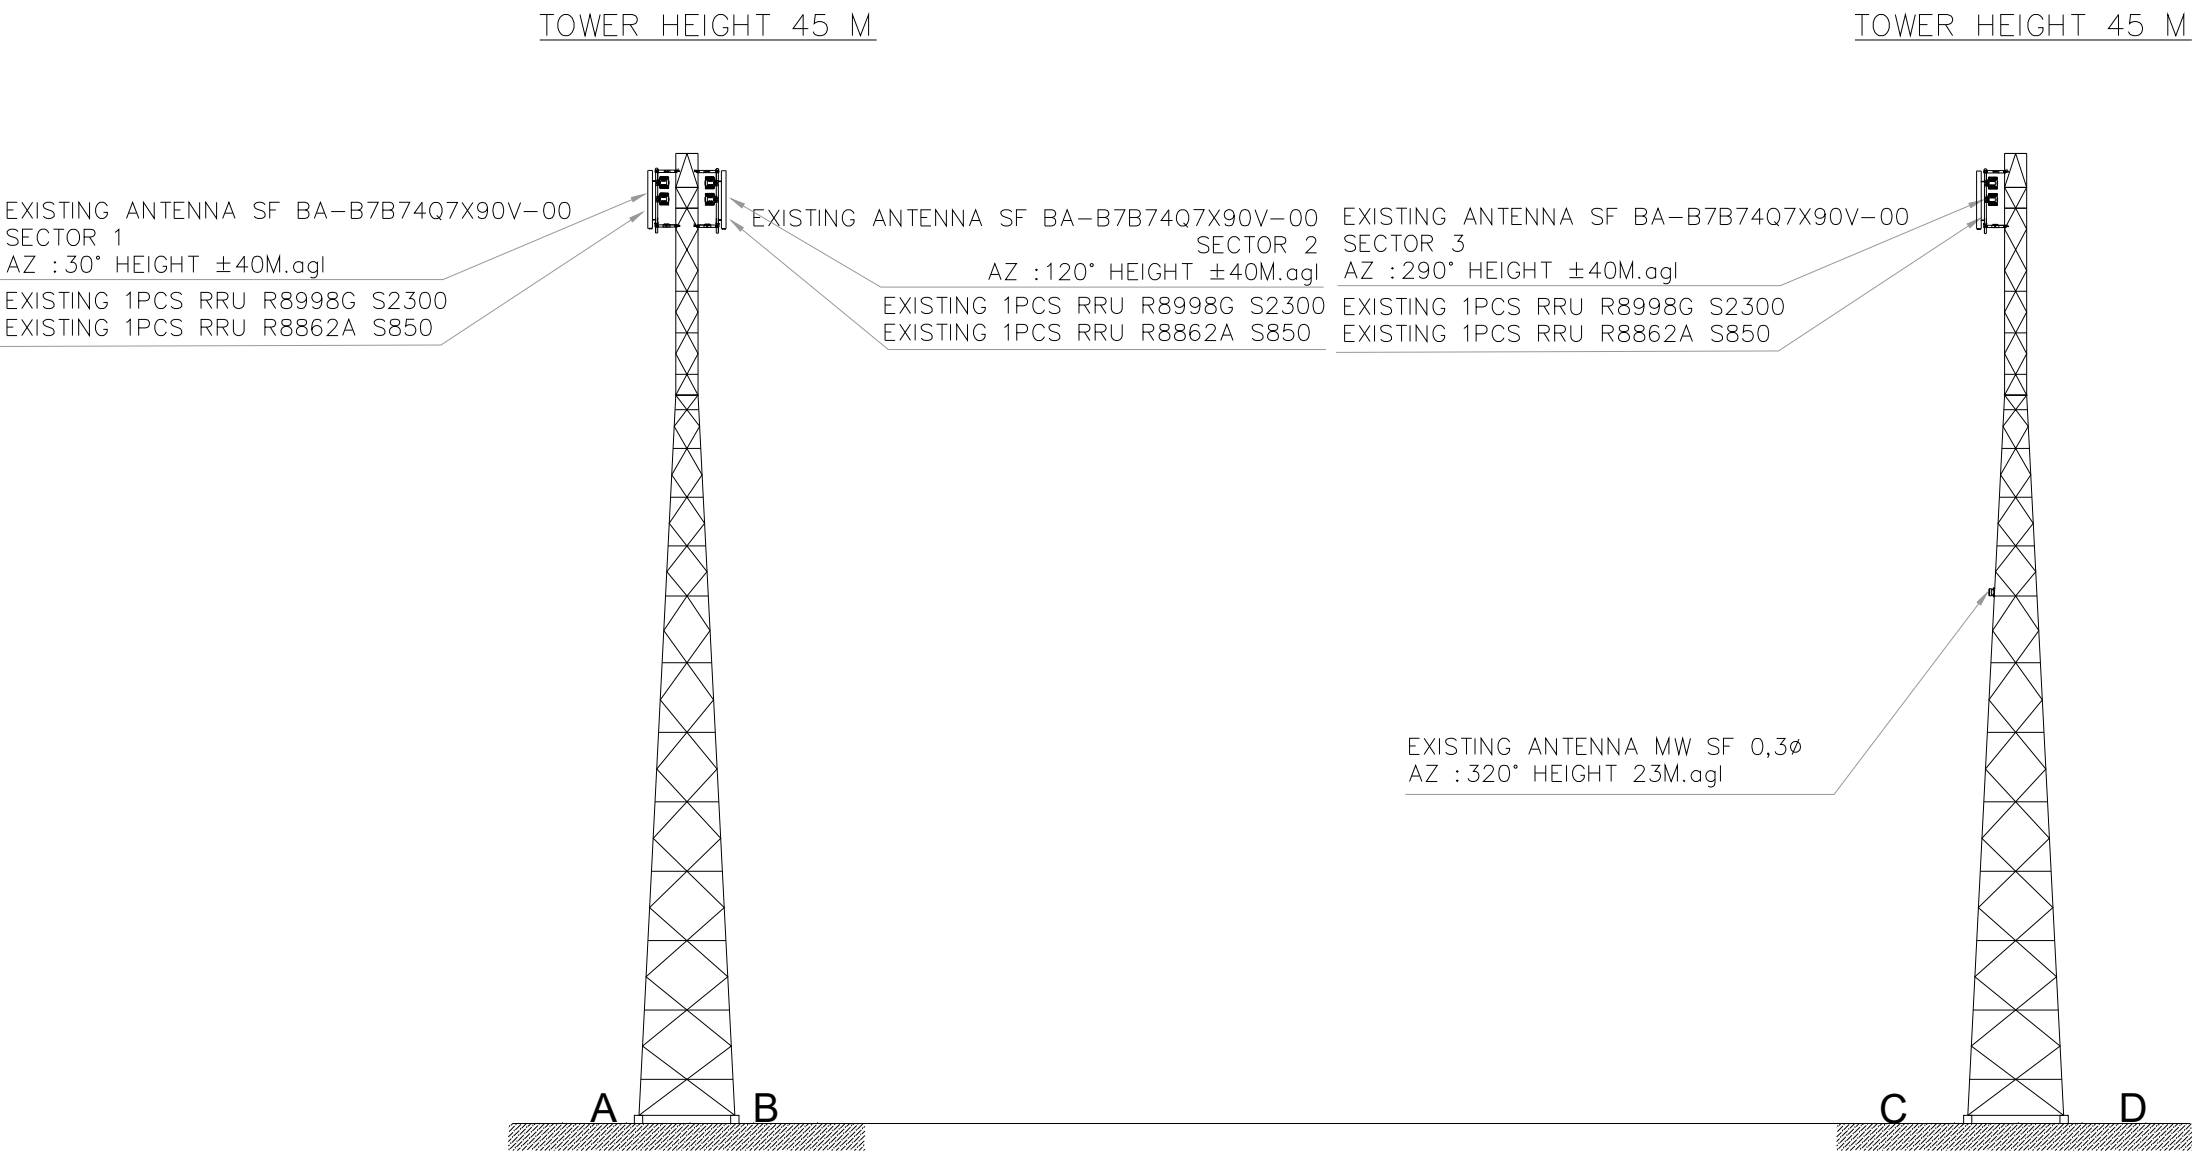

E = EXISTING	EQUIPMENT								
	EQUIPMENT TYPE	NO	SEC	TYPE	SIZE	AZ	HEIGHT	POLE/LEG	FAR-END
E	RF ANTENNA (SF)	A01	1	BA-B7B74Q7X90V-00	-	30°	40,00 m	A	
E	RF ANTENNA (SF)	A02	2	BA-B7B74Q7X90V-00	-	120°	40,00 m	B	
E	RF ANTENNA (SF)	A03	3	BA-B7B74Q7X90V-00	-	290°	40,00 m	C	
E	RRU		1	RRU R8862A S850			40,00 m	A	
E	RRU		2	RRU R8862A S850			40,00 m	B	
E	RRU		3	RRU R8862A S850			40,00 m	C	
E	RRU		1	RRU R8998G S2300			40,00 m	A	
E	RRU		2	RRU R8998G S2300			40,00 m	B	
E	RRU		3	RRU R8998G S2300			40,00 m	C	
E	ANTENNA MW		1	TYA03U023D 0,3			23,00 m	C	

OP. TOWER INFORMATION

REMARKS

- ALL DIMENSIONS ARE IN MILIMETER UNLESS NOTED ON THE DRAWING
- ALL DIMENSIONS SHALL BE CONFIRMED ON SITES

APPROVED BY

CHECKED BY



REGIONAL_PROJECT_MANAGER_AREA

CHECKED BY



DATE	REVISION	SIGN

THIS DOCUMENT AND ALL MATERIAL CONTAINED HEREIN IS PROTECTED BY COPYRIGHT, TRADEMARKS AND OTHER RIGHTS WHICH ARE OWNED AND/OR CONTROLLED BY PT INDOSAT AND/OR ITS AFFILIATES OR BY OTHER PARTIES THAT HAVE LICENSED THEIR MATERIAL TO ITS AFFILIATES

PROJECT NAME

DRAWING TITLE

SITE NAME	CIKASUNGKA_CIKANCUNG
SITE ID	ZBDG_6379
SCALE	
DRAWING BY	
CHECKED BY	
VERIFIED BY	
CONTRACT NO	
PROJECT NO	
DRAWING NUMBER	TOTAL DRAWING
PAGE NUMBER	TOTAL PAGE

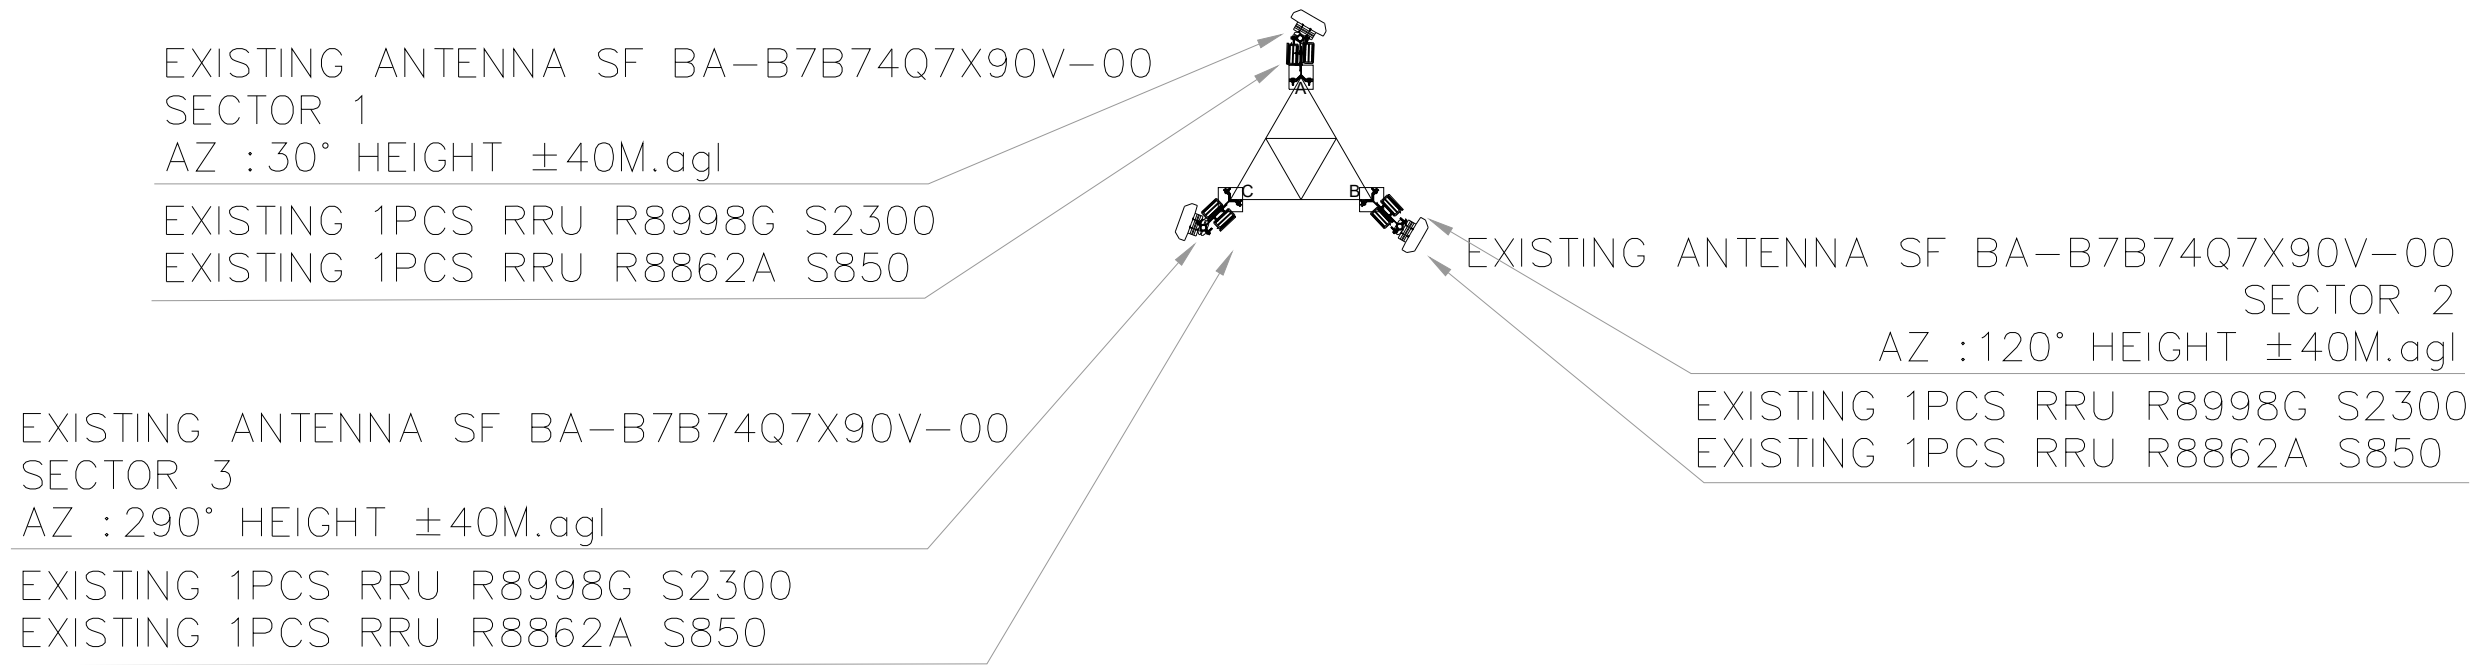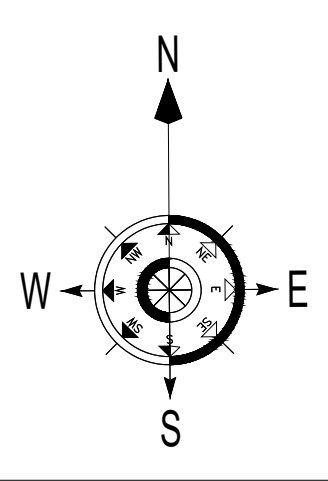

REMARKS

1. ALL DIMENSIONS ARE IN MILIMETER UNLESS NOTED ON THE DRAWING
2. ALL DIMENSIONS SHALL BE CONFIRMED ON SITES

APPROVED BY

CHECKED BY

 PT. HUAWEI TECH INVESTMENT


REGIONAL_PROJECT_MANAGER_AREA

CHECKED BY

DATE	REVISION	SIGN

THIS DOCUMENT AND ALL MATERIAL CONTAINED HEREIN IS PROTECTED BY COPYRIGHT, TRADEMARKS AND OTHER RIGHTS WHICH ARE OWNED AND/OR CONTROLLED BY PT INDOSAT AND/OR ITS AFFILIATES OR BY OTHER PARTIES THAT HAVE LICENSED THEIR MATERIAL TO ITS AFFILIATES

PROJECT NAME	
DRAWING TITLE	
SITE NAME	CIKASUNGKA_CIKANCUNG
SITE ID	ZBDG_6379
SCALE	
DRAWING BY	
CHECKED BY	
VERIFIED BY	
CONTRACT NO	
PROJECT NO	
DRAWING NUMBER	TOTAL DRAWING
PAGE NUMBER	TOTAL PAGE

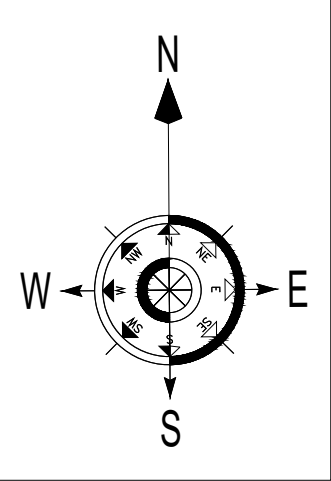


EXISTING ANTENNA SF BA-B7B74Q7X90V-00
SECTOR 1
AZ : 30° HEIGHT ±40M.agl

EXISTING 1PCS RRU R8998G S2300
EXISTING 1PCS RRU R8862A S850

EXISTING ANTENNA SF BA-B7B74Q7X90V-00
SECTOR 3
AZ : 290° HEIGHT ±40M.agl

EXISTING 1PCS RRU R8998G S2300
EXISTING 1PCS RRU R8862A S850

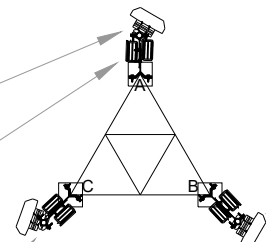

EXISTING ANTENNA SF BA-B7B74Q7X90V-00
SECTOR 2
AZ : 120° HEIGHT ±40M.agl

EXISTING 1PCS RRU R8998G S2300
EXISTING 1PCS RRU R8862A S850

REMARKS

1. ALL DIMENSIONS ARE IN MILIMETER UNLESS NOTED ON THE DRAWING
2. ALL DIMENSIONS SHALL BE CONFIRMED ON SITES

APPROVED BY

CHECKED BY



PT. HUAWEI TECH INVESTMENT

REGIONAL_PROJECT_MANAGER_AREA

CHECKED BY

DATE	REVISION	SIGN

THIS DOCUMENT AND ALL MATERIAL CONTAINED HEREIN IS PROTECTED BY COPYRIGHT, TRADEMARKS AND OTHER RIGHTS WHICH ARE OWNED AND/OR CONTROLLED BY PT INDOSAT AND/OR ITS AFFILIATES OR BY OTHER PARTIES THAT HAVE LICENSED THEIR MATERIAL TO ITS AFFILIATES

PROJECT NAME

DRAWING TITLE


SITE NAME	CIKASUNGKA_CIKANCUNG
SITE ID	ZBDG_6379
SCALE	
DRAWING BY	
CHECKED BY	
VERIFIED BY	
CONTRACT NO	
PROJECT NO	

DRAWING NUMBER	TOTAL DRAWING
----------------	---------------

--	--


PAGE NUMBER	TOTAL PAGE
-------------	------------

--	--

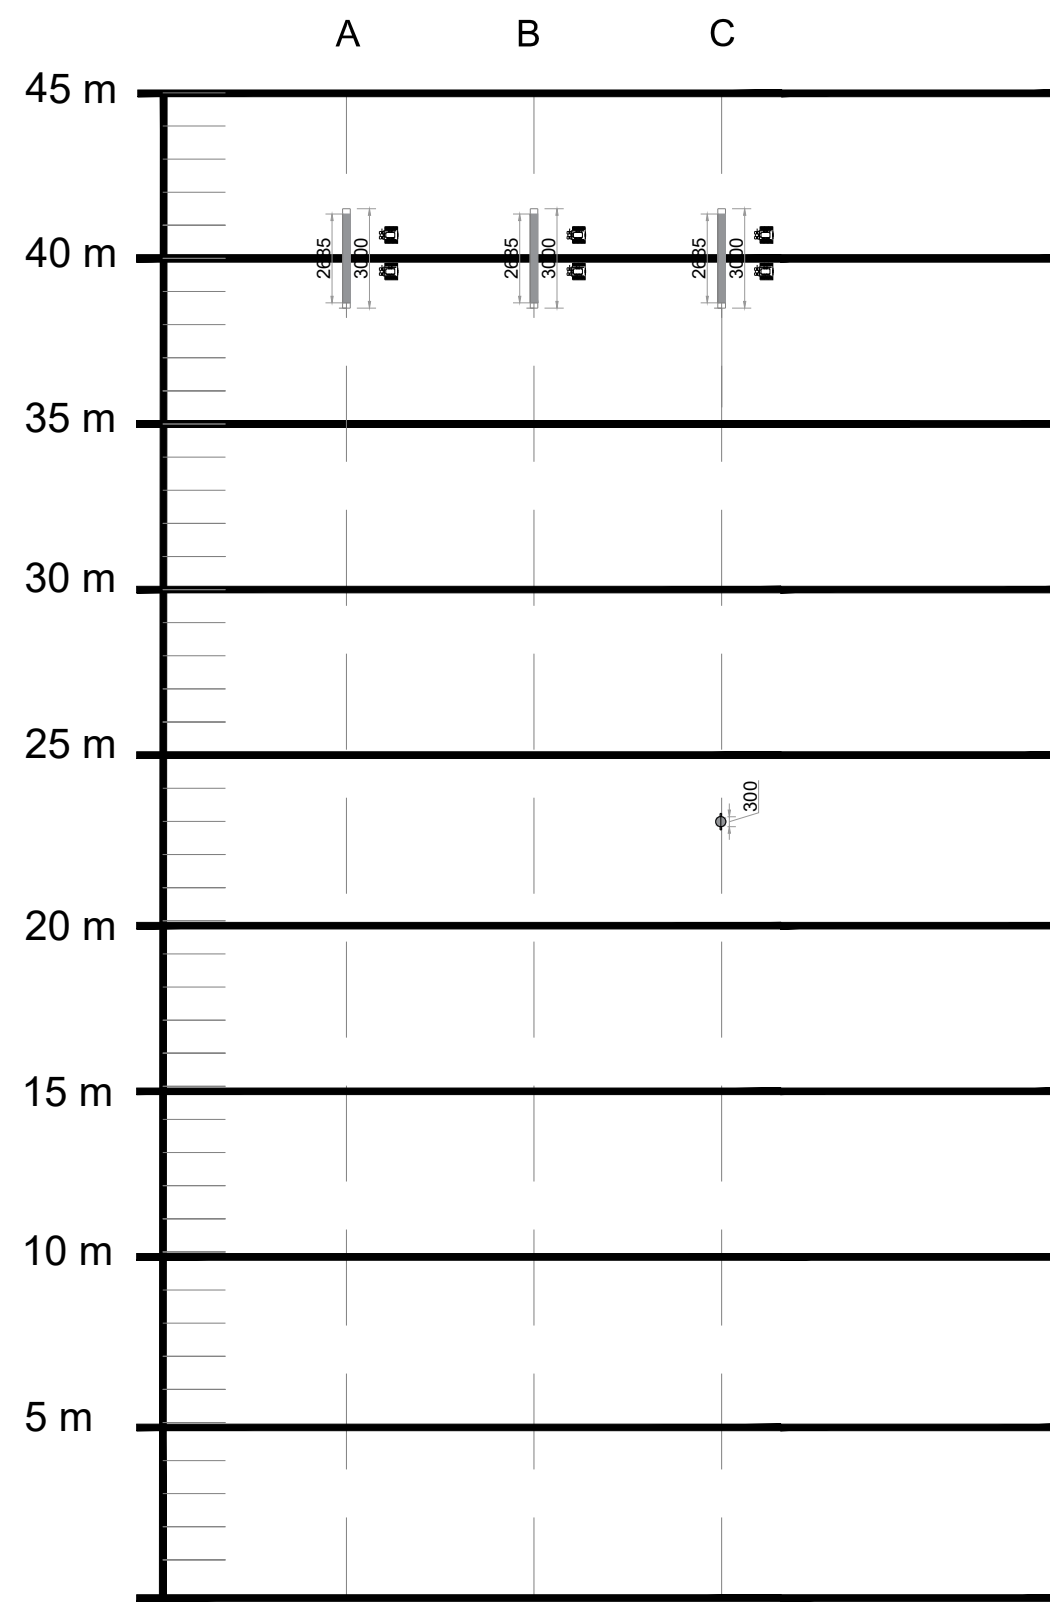

TOWER LEG ID
(CLOCKWISE FROM NORTH DIRECTION)

COLOR LEGENDS

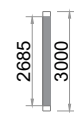

EXISTING RF ANTENNA SF (ex-IO)




EXISTING RRU SF



EXISTING MW ANTENNA SF 0.3Ø (ex-IO)

SST 3 LEG 42 METER

REMARKS		
1. ALL DIMENSIONS ARE IN MILIMETER UNLESS NOTED ON THE DRAWING 2. ALL DIMENSIONS SHALL BE CONFIRMED ON SITES		
APPROVED BY		
CHECKED BY		
PT. HUAWEI TECH INVESTMENT		
REGIONAL_PROJECT_MANAGER_AREA		
CHECKED BY		
DATE	REVISION	SIGN
THIS DOCUMENT AND ALL MATERIAL CONTAINED HEREIN IS PROTECTED BY COPYRIGHT, TRADEMARKS AND OTHER RIGHTS WHICH ARE OWNED AND/OR CONTROLLED BY PT INDOSAT AND/OR ITS AFFILIATES OR BY OTHER PARTIES THAT HAVE LICENSED THEIR MATERIAL TO ITS AFFILIATES		
PROJECT NAME		
DRAWING TITLE		
SITE NAME	CIKASUNGKA_CIKANCUNG	
SITE ID	ZBDG_6379	
SCALE		
DRAWING BY		
CHECKED BY		
VERIFIED BY		
CONTRACT NO		
PROJECT NO		
DRAWING NUMBER	TOTAL DRAWING	
PAGE NUMBER	TOTAL PAGE	

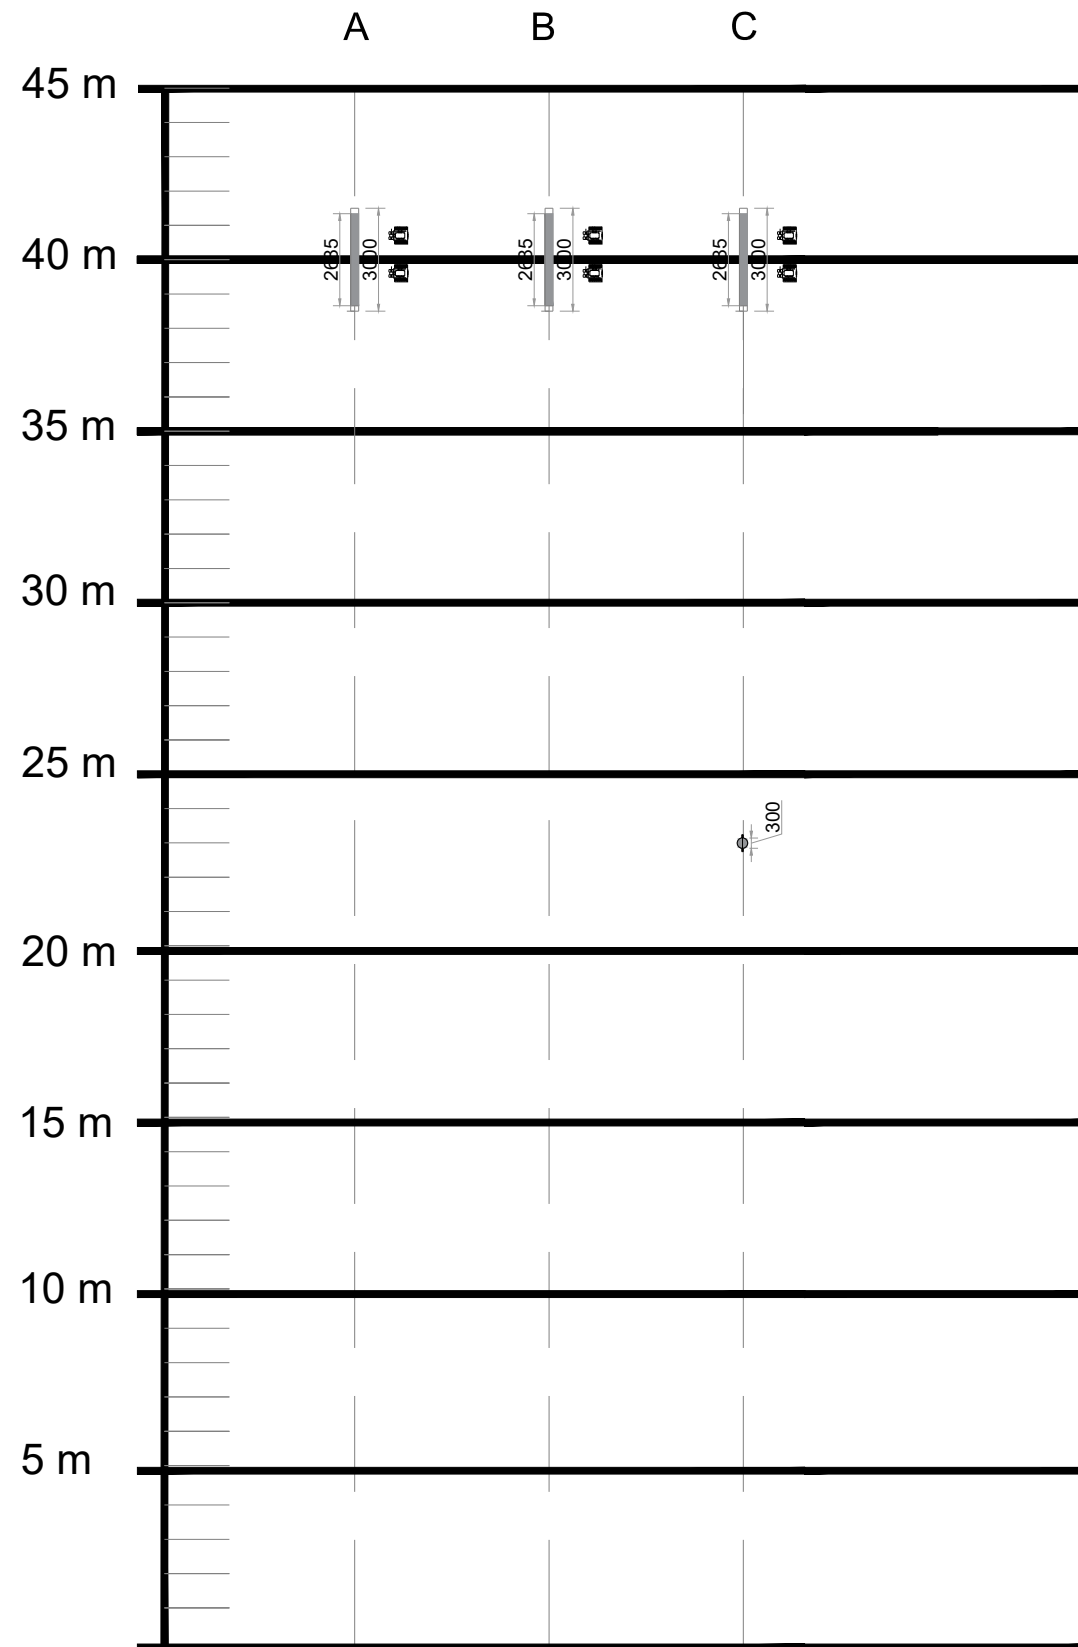

SST 3 LEG 42 METER

TOWER LEG ID
(CLOCKWISE FROM NORTH DIRECTION)

COLOR LEGENDS



EXISTING RF ANTENNA SF (ex-IO)



EXISTING RRU SF




EXISTING MW ANTENNA SF 0.3Ø (ex-IO)

REMARKS

1. ALL DIMENSIONS ARE IN MILIMETER UNLESS NOTED ON THE DRAWING
2. ALL DIMENSIONS SHALL BE CONFIRMED ON SITES

APPROVED BY

CHECKED BY

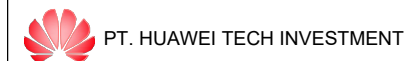

REGIONAL_PROJECT_MANAGER_AREA

CHECKED BY

DATE	REVISION	SIGN

THIS DOCUMENT AND ALL MATERIAL CONTAINED HEREIN IS PROTECTED BY COPYRIGHT, TRADEMARKS AND OTHER RIGHTS WHICH ARE OWNED AND/OR CONTROLLED BY PT INDOSAT AND/OR ITS AFFILIATES OR BY OTHER PARTIES THAT HAVE LICENSED THEIR MATERIAL TO ITS AFFILIATES

PROJECT NAME

DRAWING TITLE

SITE NAME	CIKASUNGKA_CIKANCUNG
SITE ID	ZBDG_6379
SCALE	
DRAWING BY	
CHECKED BY	
VERIFIED BY	
CONTRACT NO	
PROJECT NO	

DRAWING NUMBER	TOTAL DRAWING
----------------	---------------

--	--

PAGE NUMBER	TOTAL PAGE
-------------	------------

--	--