
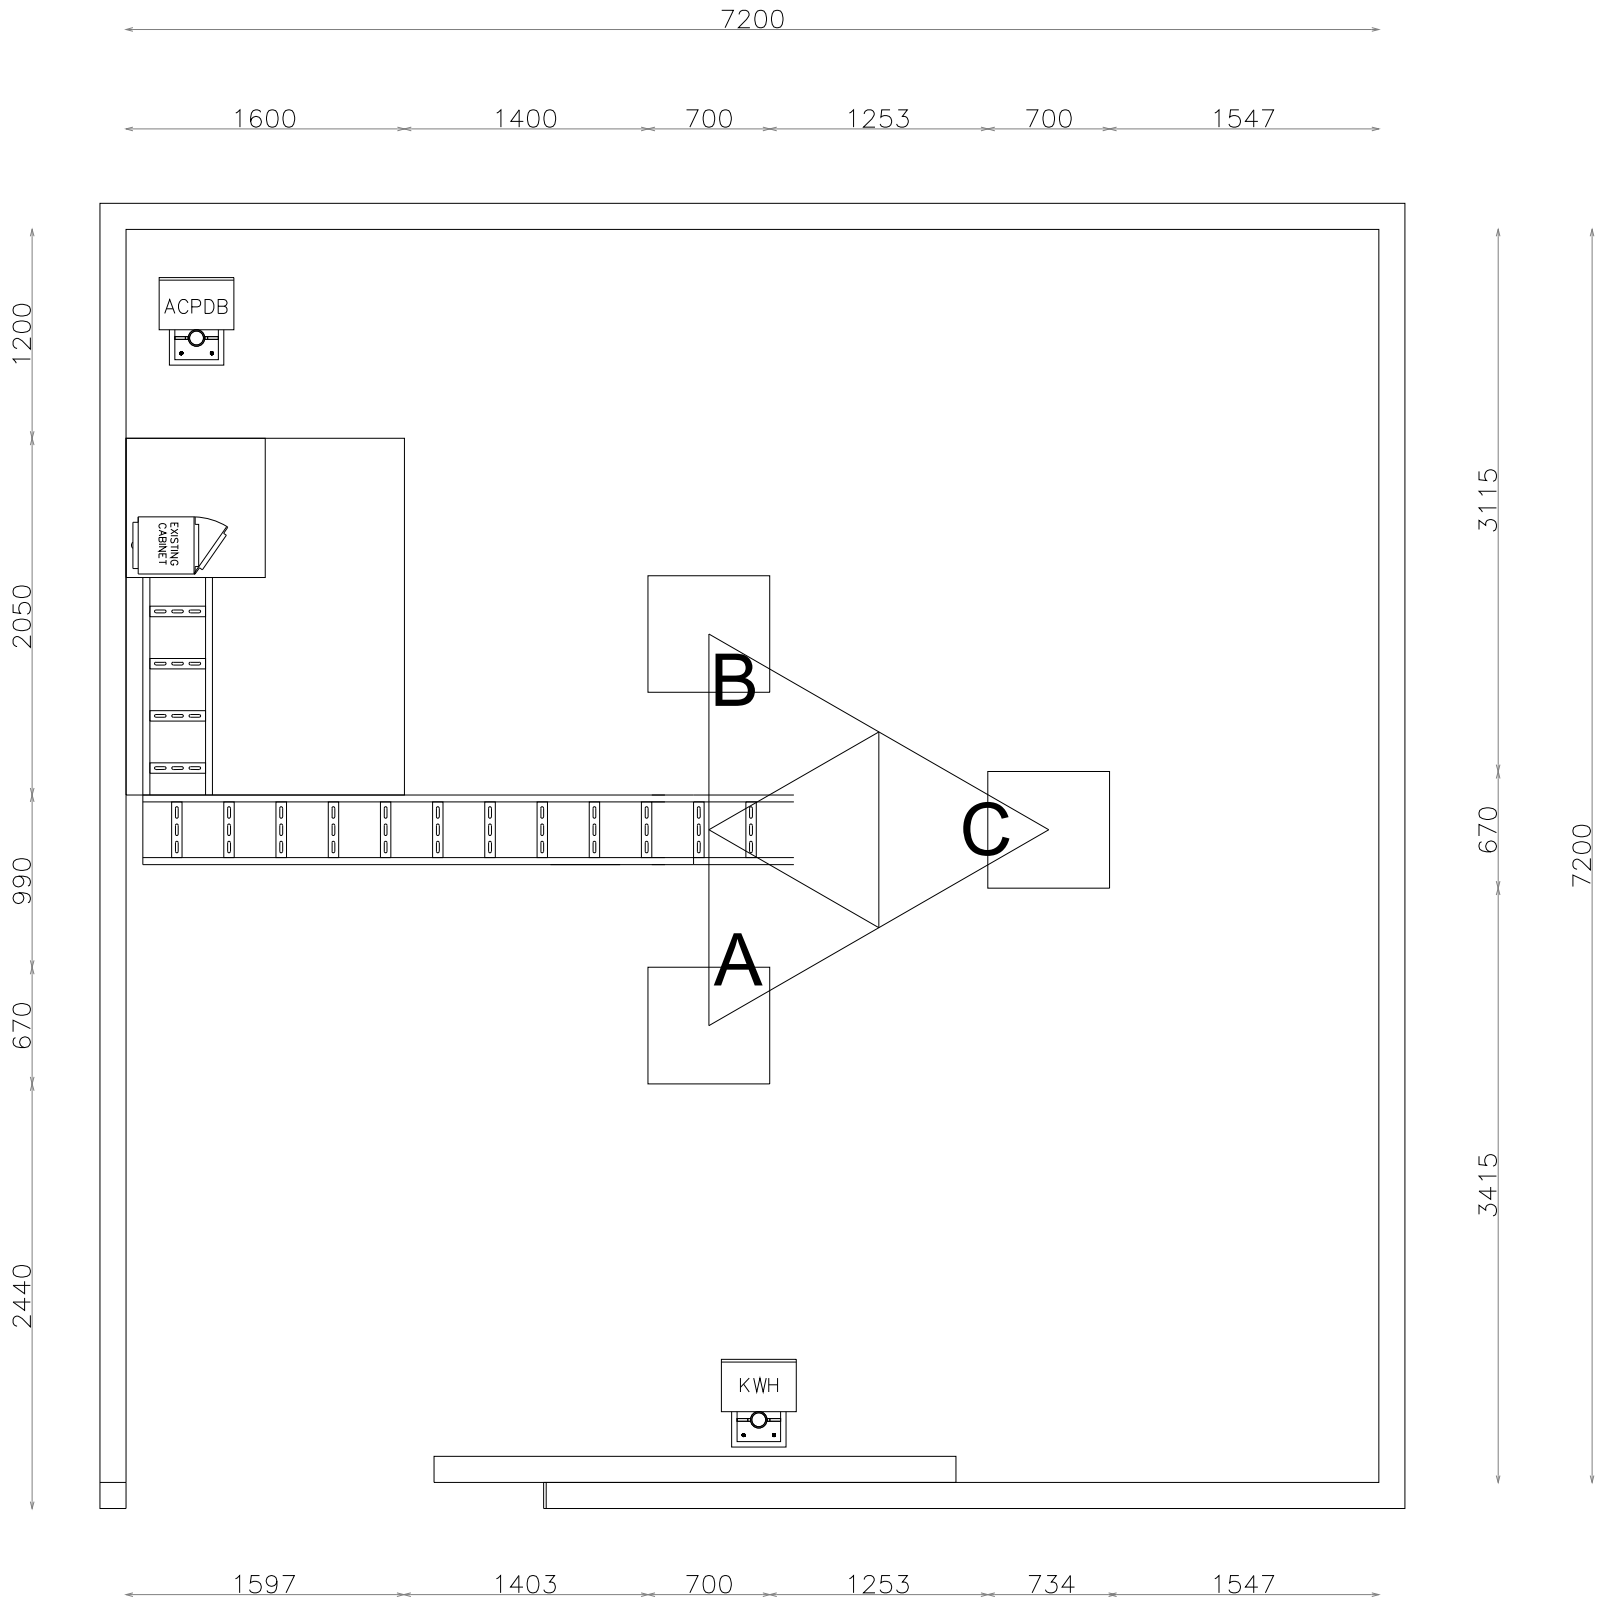


- PROPOSED POWER CABLE
- PROPOSED POWER CABLE
- PROPOSED GROUNDING C
- PROPOSED HYBRID CABLE
- PROPOSED OPTICAL CABL
- COAXIAL CABLE
- EXISTING FEEDER
- EXISTING JUMPER
- PROPOSED JUMPER
- PROPOSED CABINET
- DISMANTLE EQUIPMENT
- EXISTING EQUIPMENT

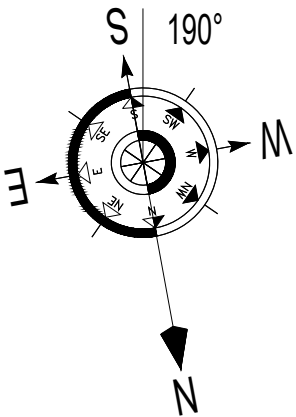

REMARKS

1. ALL DIMENSIONS ARE IN MILIMETER UNLESS NOTED ON THE DRAWING
2. ALL DIMENSIONS SHALL BE CONFIRMED ON SITES

APPROVED BY

CHECKED BY



REGIONAL_PROJECT_MANAGER_AREA

CHECKED BY

DATE	REVISION	SIGN

THIS DOCUMENT AND ALL MATERIAL CONTAINED HEREIN IS PROTECTED BY COPYRIGHT, TRADEMARKS AND OTHER RIGHTS WHICH ARE OWNED AND/OR CONTROLLED BY PT INDOSAT AND/OR ITS AFFILIATES OR BY OTHER PARTIES THAT HAVE LICENSED THEIR MATERIAL TO ITS AFFILIATES

PROJECT NAME

DRAWING TITLE

SITE NAME	WARGALUYU_ARJASARI
SITE ID	ZBDG_6380
SCALE	
DRAWING BY	
CHECKED BY	
VERIFIED BY	
CONTRACT NO	
PROJECT NO	

DRAWING NUMBER	TOTAL DRAWING
PAGE NUMBER	TOTAL PAGE

PROPOSED POWER CABLE

PROPOSED POWER CABLE

PROPOSED GROUNDING C

PROPOSED HYBRID CABLE

PROPOSED OPTICAL CABL

COAXIAL CABLE

EXISTING FEEDER


EXISTING JUMPER

PROPOSED JUMPER

PROPOSED CABINET

DISMANTLE EQUIPMENT

EXISTING EQUIPMENT

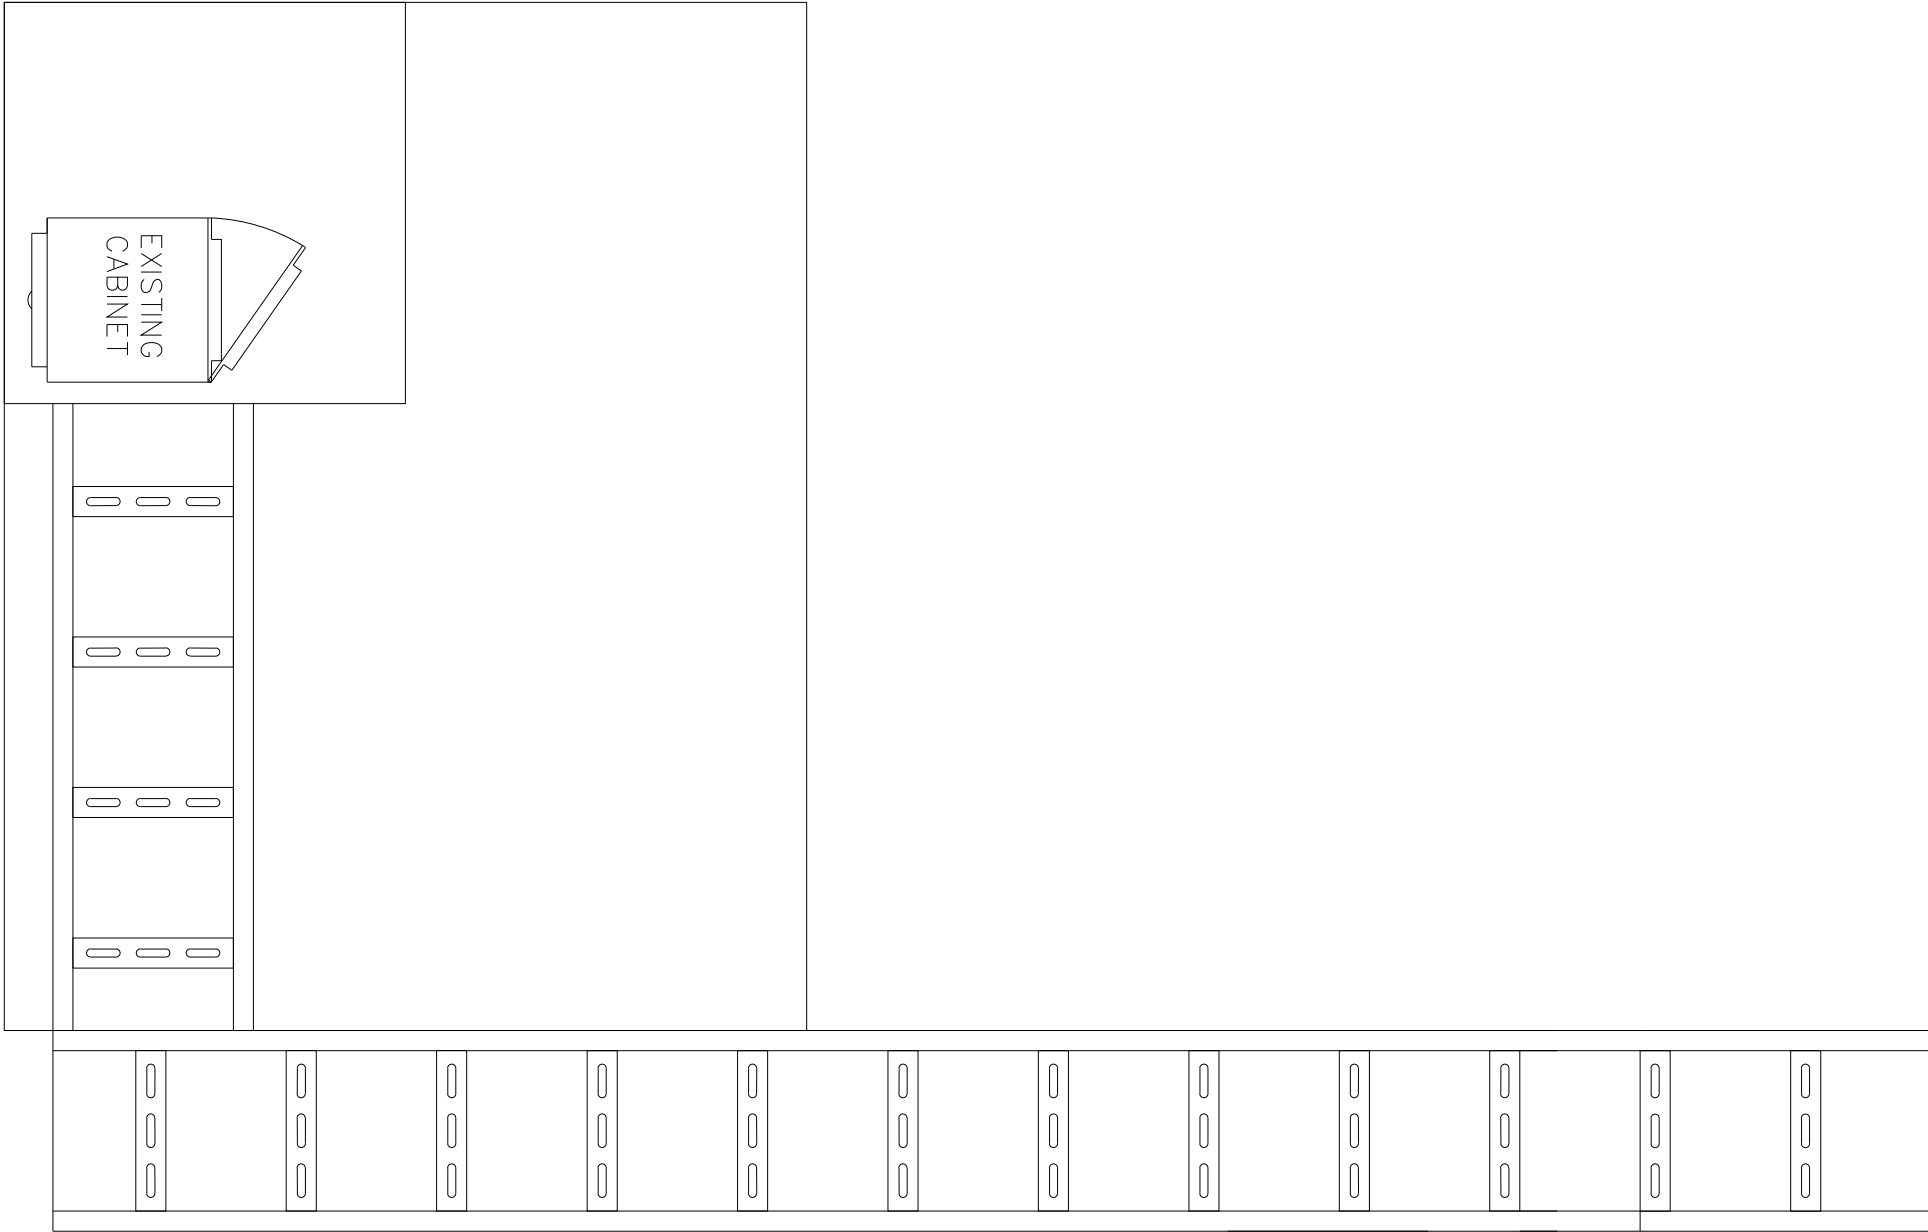

REMARKS

1. ALL DIMENSIONS ARE IN MILIMETER UNLESS NOTED ON THE DRAWING

2. ALL DIMENSIONS SHALL BE CONFIRMED ON SITES

APPROVED BY

CHECKED BY

 PT. HUAWEI TECH INVESTMENT

REGIONAL_PROJECT_MANAGER_AREA

CHECKED BY

DATE	REVISION	SIGN

THIS DOCUMENT AND ALL MATERIAL CONTAINED HEREIN IS PROTECTED BY COPYRIGHT, TRADEMARKS AND OTHER RIGHTS WHICH ARE OWNED AND/OR CONTROLLED BY PT INDOSAT AND/OR ITS AFFILIATES OR BY OTHER PARTIES THAT HAVE LICENSED THEIR MATERIAL TO ITS AFFILIATES

PROJECT NAME	
DRAWING TITLE	
SITE NAME	WARGALUYU_ARJASARI
SITE ID	ZBDG_6380
SCALE	
DRAWING BY	
CHECKED BY	
VERIFIED BY	
CONTRACT NO	
PROJECT NO	
DRAWING NUMBER	TOTAL DRAWING
PAGE NUMBER	TOTAL PAGE

PROPOSED POWER CABLE

PROPOSED POWER CABLE

PROPOSED GROUNDING C

PROPOSED HYBRID CABLE

PROPOSED OPTICAL CABL

COAXIAL CABLE

EXISTING FEEDER


EXISTING JUMPER

PROPOSED JUMPER

PROPOSED CABINET

DISMANTLE EQUIPMENT

EXISTING EQUIPMENT

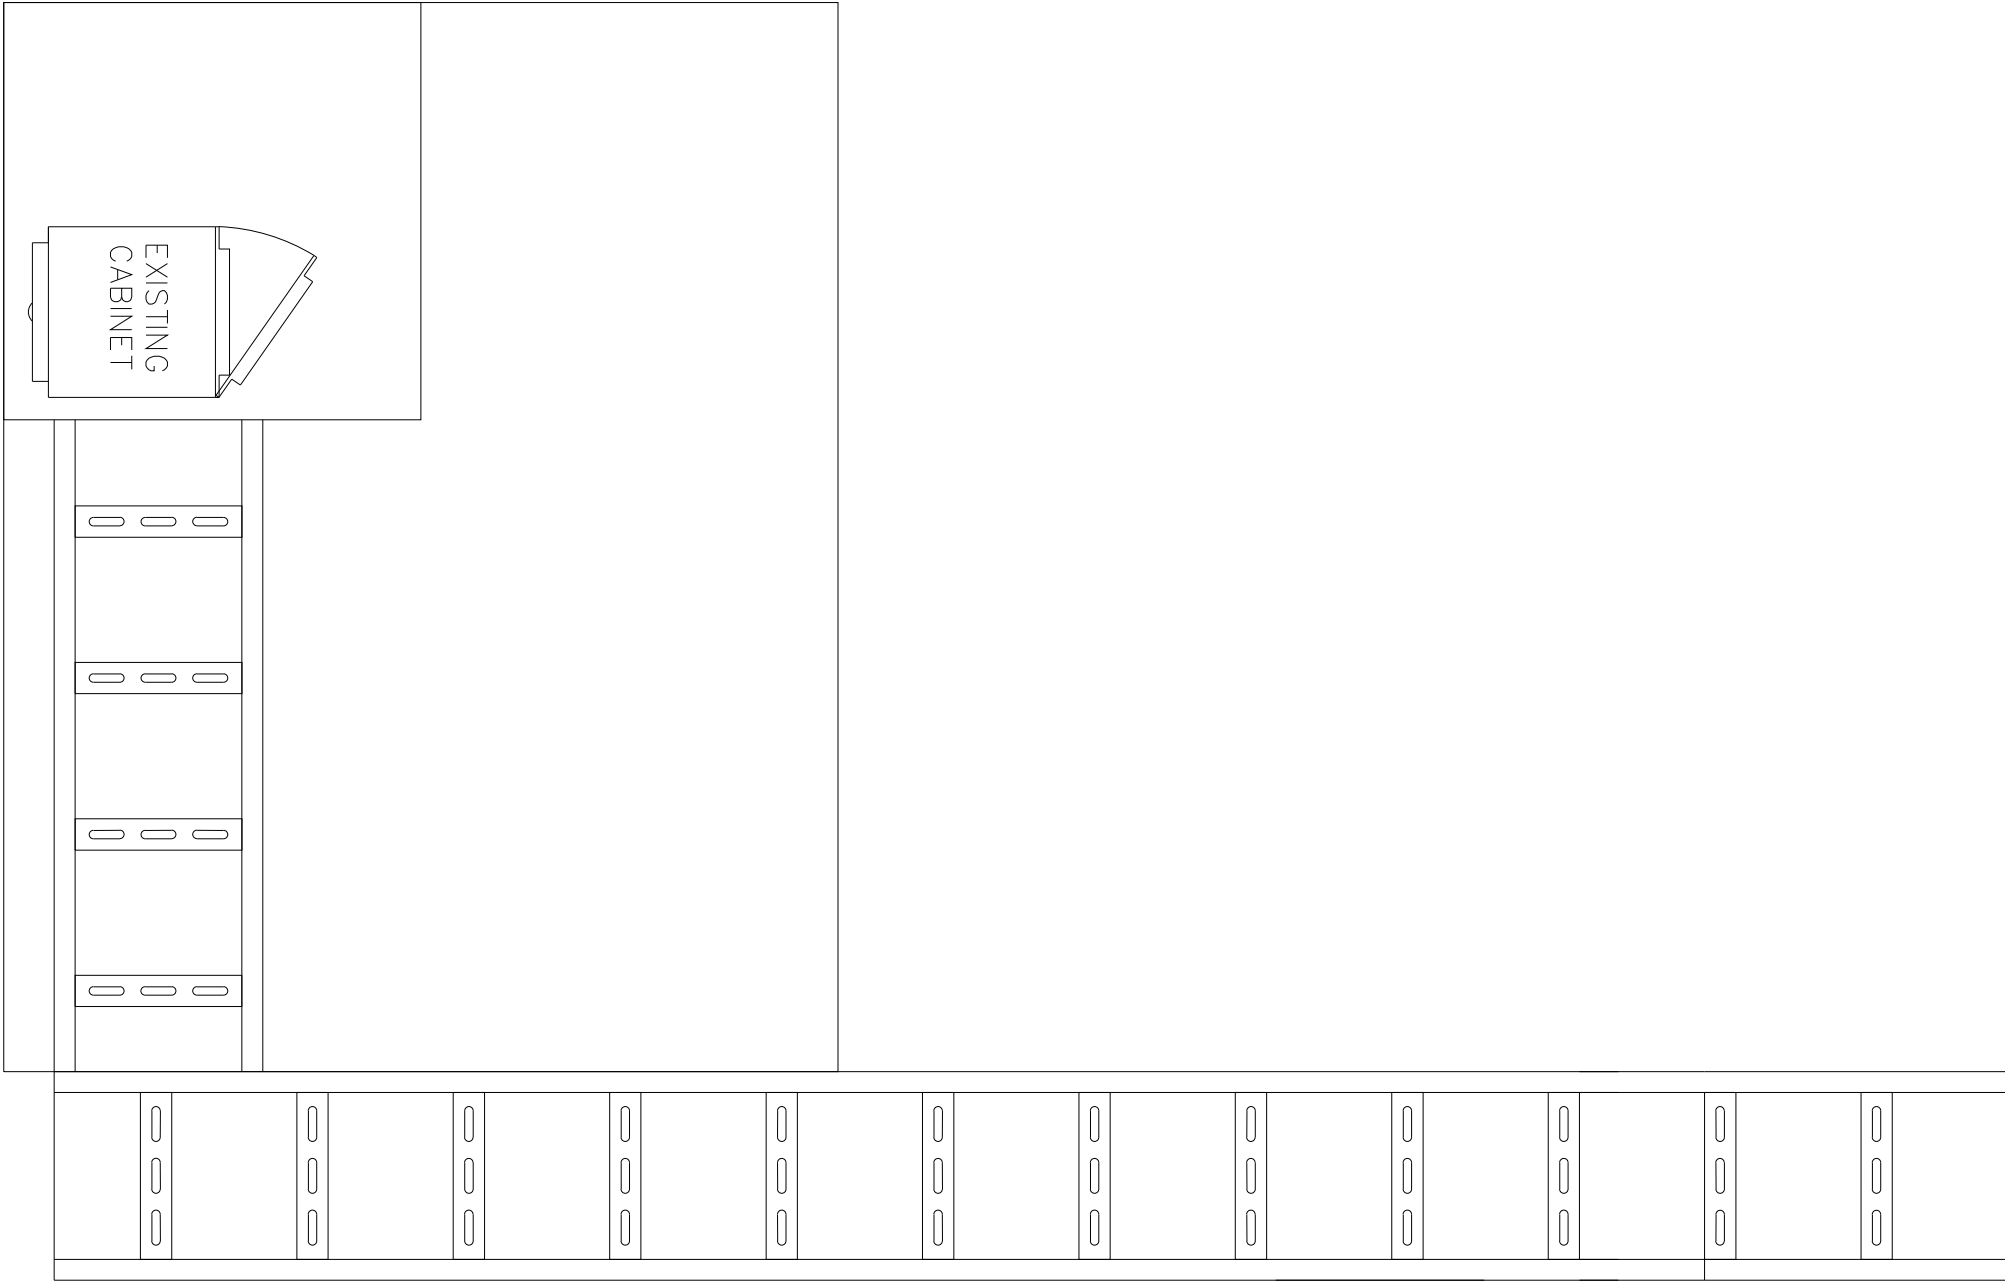

REMARKS

- ALL DIMENSIONS ARE IN MILIMETER UNLESS NOTED ON THE DRAWING
- ALL DIMENSIONS SHALL BE CONFIRMED ON SITES

APPROVED BY

CHECKED BY



PT. HUAWEI TECH INVESTMENT

REGIONAL_PROJECT_MANAGER_AREA

CHECKED BY

DATE	REVISION	SIGN


THIS DOCUMENT AND ALL MATERIAL CONTAINED HEREIN IS PROTECTED BY COPYRIGHT, TRADEMARKS AND OTHER RIGHTS WHICH ARE OWNED AND/OR CONTROLLED BY PT INDOSAT AND/OR ITS AFFILIATES OR BY OTHER PARTIES THAT HAVE LICENSED THEIR MATERIAL TO ITS AFFILIATES


PROJECT NAME


DRAWING TITLE

SITE NAME	WARGALUYU_ARJASARI
SITE ID	ZBDG_6380
SCALE	
DRAWING BY	
CHECKED BY	
VERIFIED BY	
CONTRACT NO	
PROJECT NO	
DRAWING NUMBER	TOTAL DRAWING
PAGE NUMBER	TOTAL PAGE



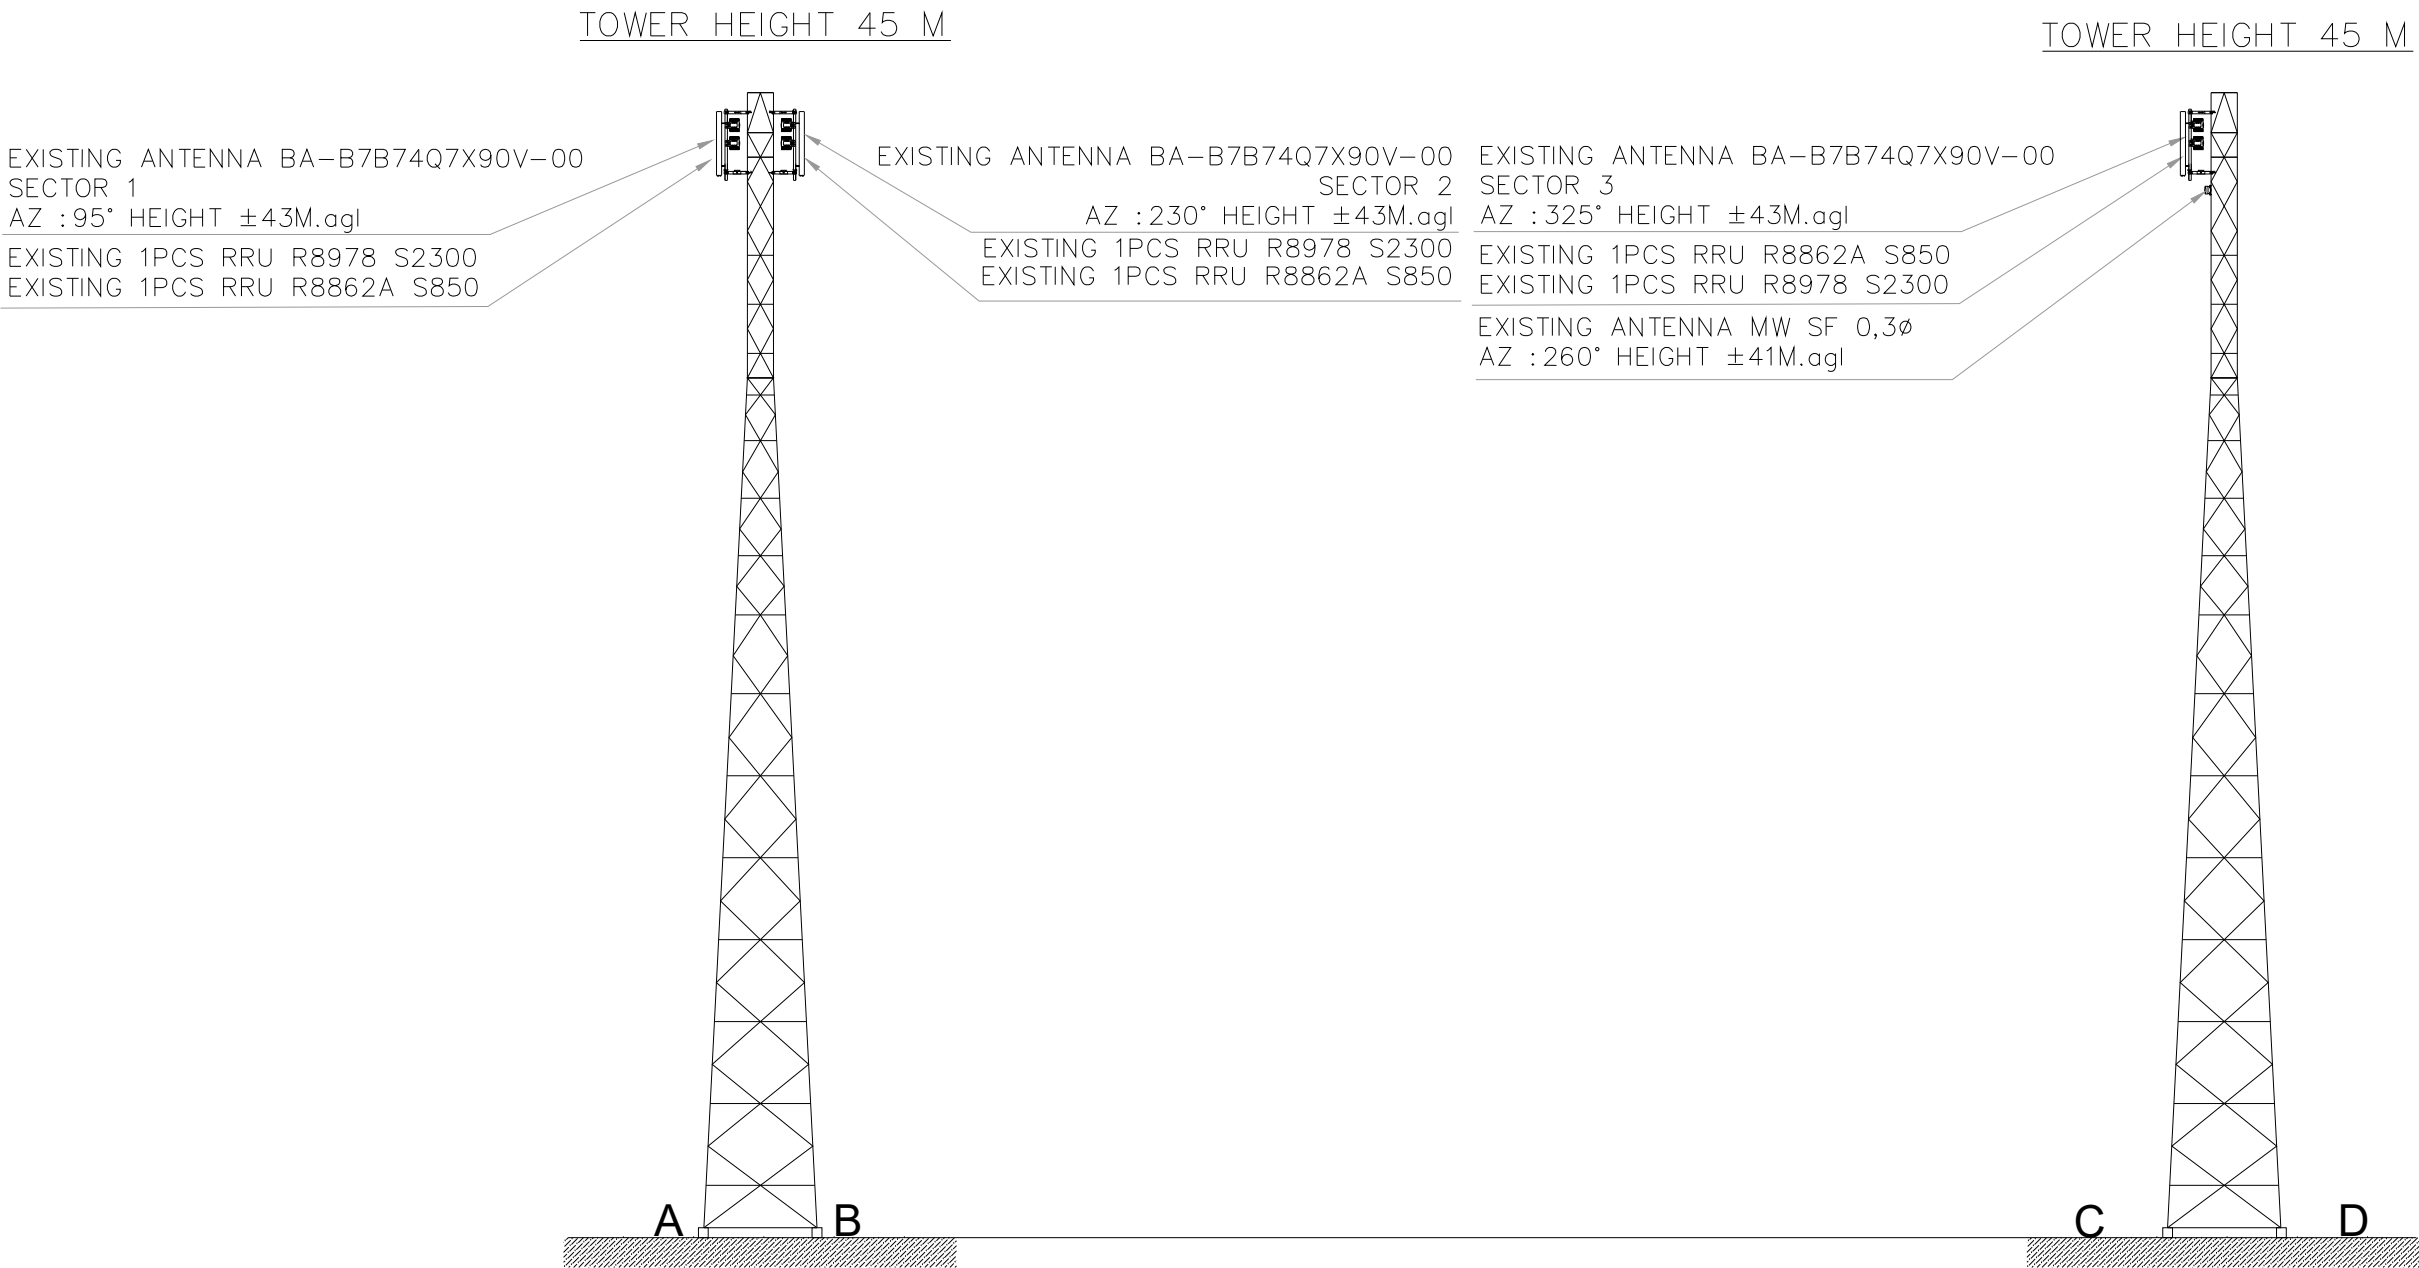

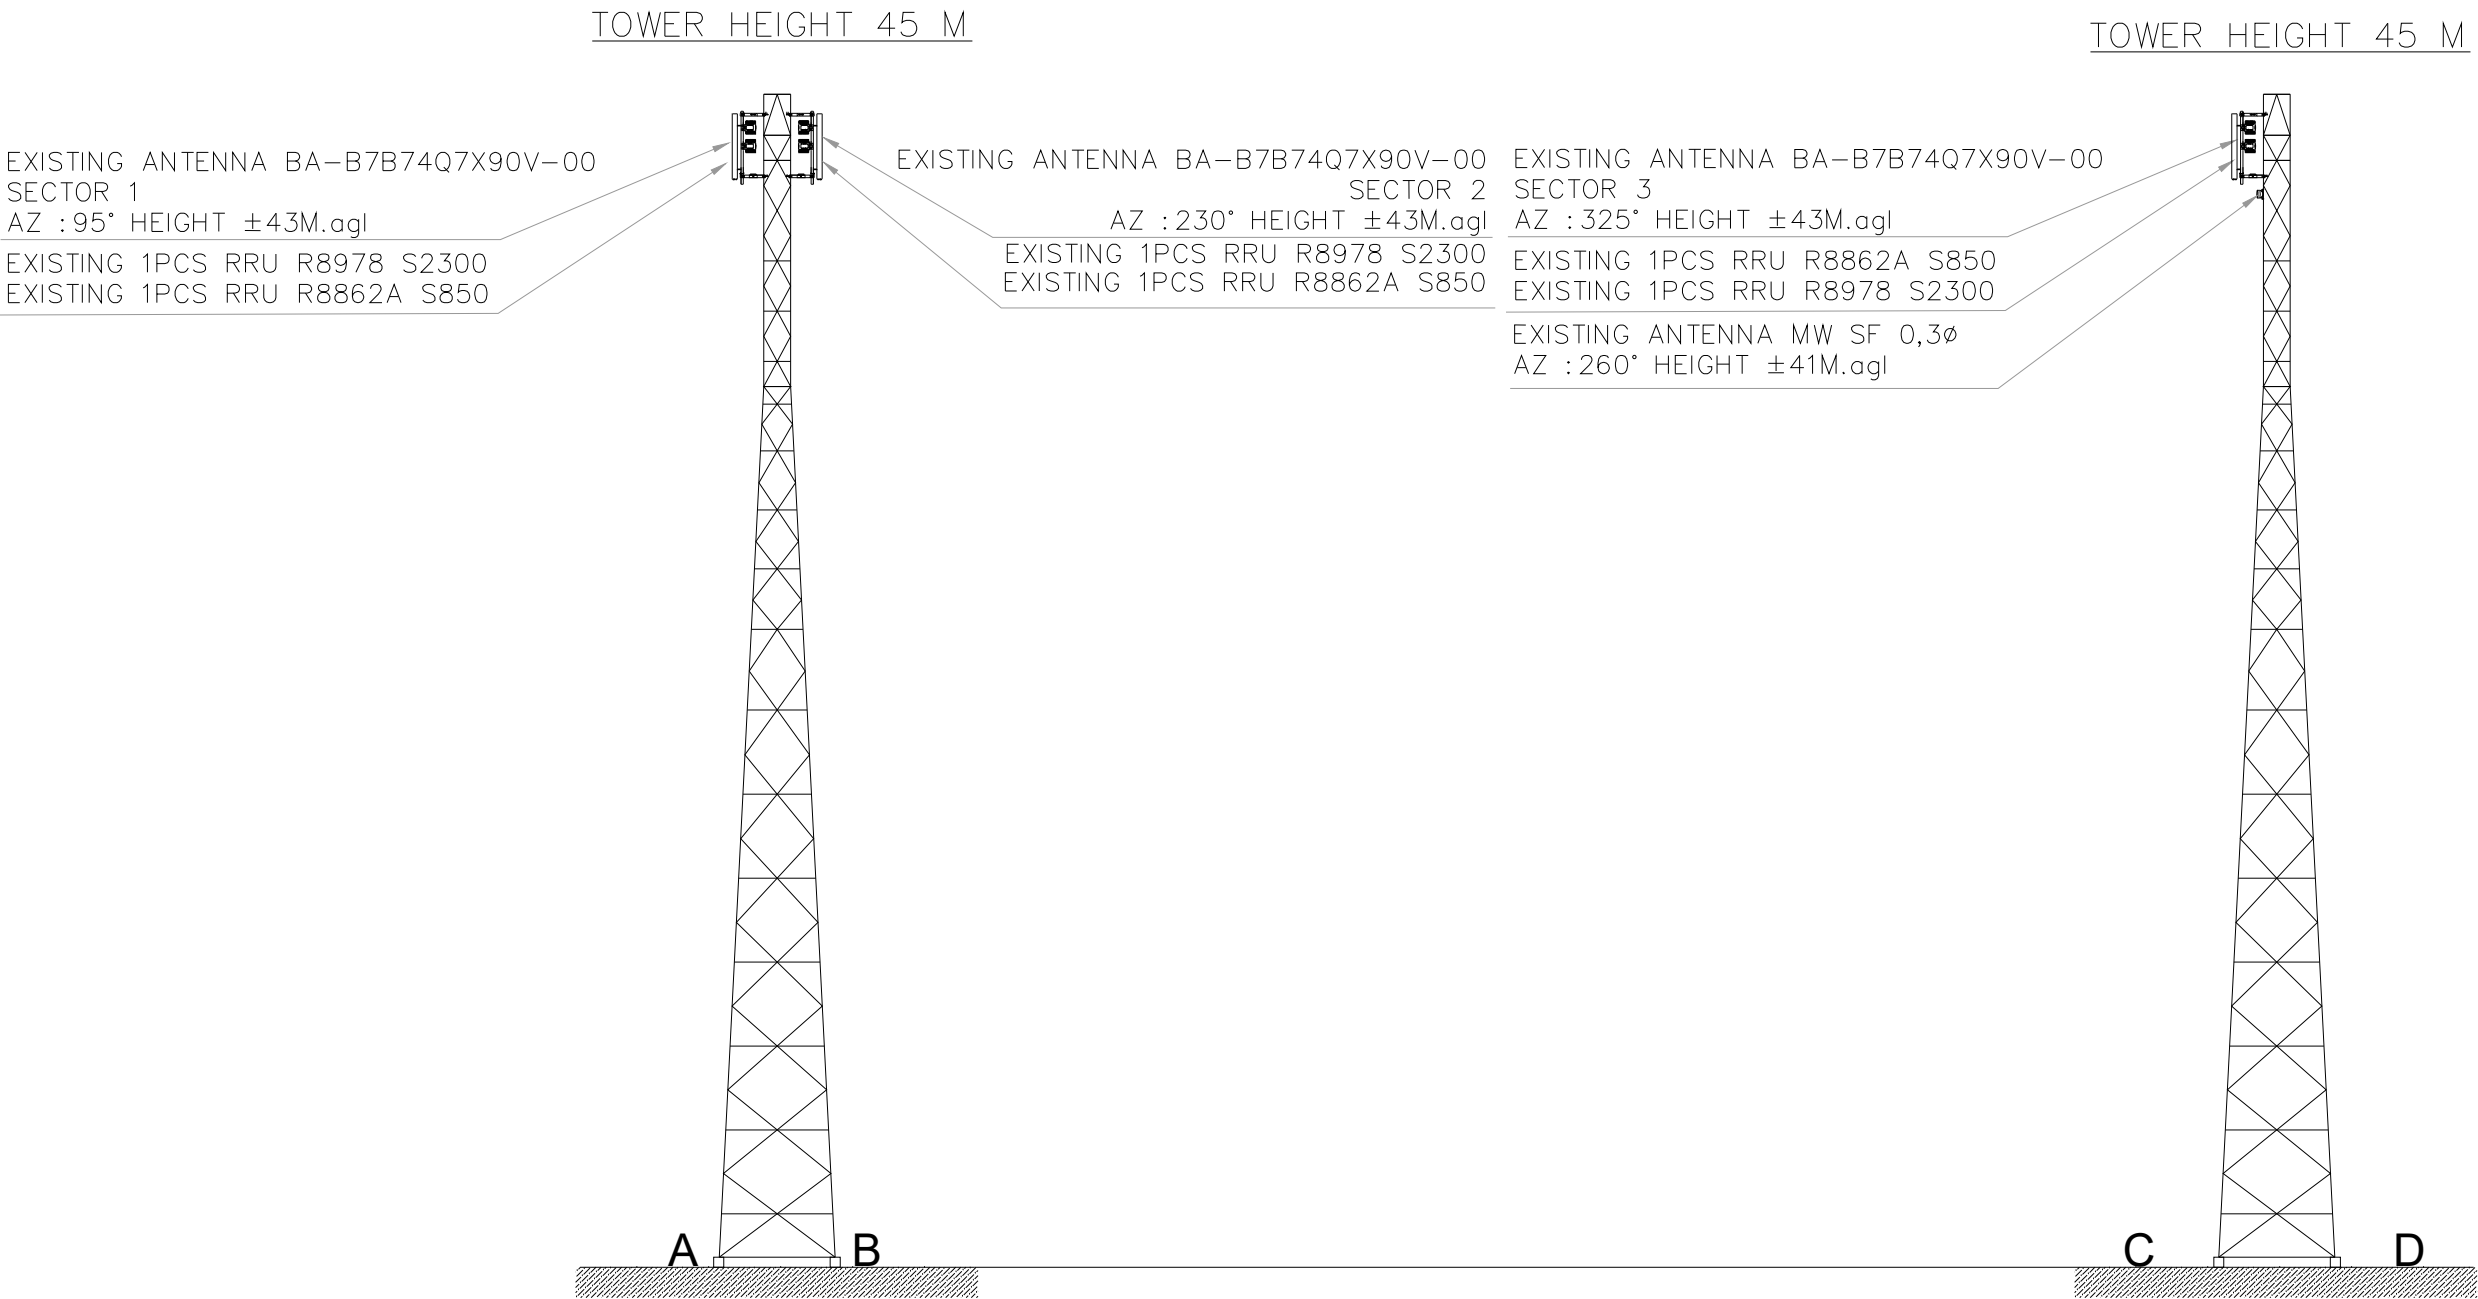

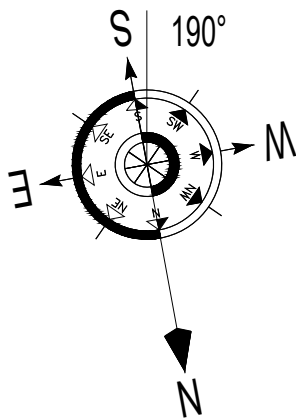

EXISTING ANTENNA BA-B7B74Q7X90V-00
SECTOR 2
AZ : 230° HEIGHT ±43M.agl
EXISTING 1PCS RRU R8978 S2300
EXISTING 1PCS RRU R8862A S850

EXISTING ANTENNA BA-B7B74Q7X90V-00
SECTOR 1
AZ : 95° HEIGHT ±43M.agl
EXISTING 1PCS RRU R8978 S2300
EXISTING 1PCS RRU R8862A S850

EXISTING ANTENNA BA-B7B74Q7X90V-00
SECTOR 3
AZ : 325° HEIGHT ±43M.agl
EXISTING 1PCS RRU R8862A S850
EXISTING 1PCS RRU R8978 S2300

REMARKS

- 1. ALL DIMENSIONS ARE IN MILIMETER UNLESS NOTED ON THE DRAWING
- 2. ALL DIMENSIONS SHALL BE CONFIRMED ON SITES

APPROVED BY

CHECKED BY



REGIONAL_PROJECT_MANAGER_AREA

CHECKED BY

DATE	REVISION	SIGN


THIS DOCUMENT AND ALL MATERIAL CONTAINED HEREIN IS PROTECTED BY COPYRIGHT, TRADEMARKS AND OTHER RIGHTS WHICH ARE OWNED AND/OR CONTROLLED BY PT INDOSAT AND/OR ITS AFFILIATES OR BY OTHER PARTIES THAT HAVE LICENSED THEIR MATERIAL TO ITS AFFILIATES

PROJECT NAME

DRAWING TITLE


SITE NAME	WARGALUYU_ARJASARI
SITE ID	ZBDG_6380
SCALE	
DRAWING BY	
CHECKED BY	
VERIFIED BY	
CONTRACT NO	
PROJECT NO	

DRAWING NUMBER	TOTAL DRAWING
PAGE NUMBER	TOTAL PAGE

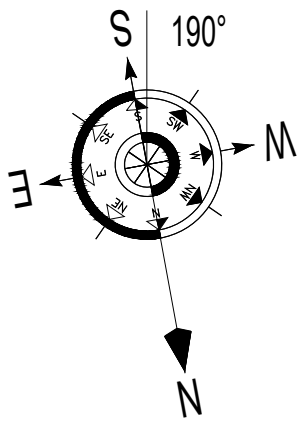

EXISTING ANTENNA BA-B7B74Q7X90V-00
SECTOR 2
AZ : 230° HEIGHT ±43M.agl
EXISTING 1PCS RRU R8978 S2300
EXISTING 1PCS RRU R8862A S850

EXISTING ANTENNA BA-B7B74Q7X90V-00
SECTOR 1
AZ : 95° HEIGHT ±43M.agl
EXISTING 1PCS RRU R8978 S2300
EXISTING 1PCS RRU R8862A S850

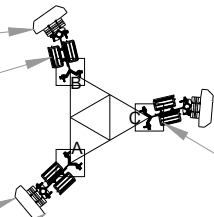

EXISTING ANTENNA BA-B7B74Q7X90V-00
SECTOR 3
AZ : 325° HEIGHT ±43M.agl
EXISTING 1PCS RRU R8862A S850
EXISTING 1PCS RRU R8978 S2300

REMARKS

- 1. ALL DIMENSIONS ARE IN MILIMETER UNLESS NOTED ON THE DRAWING
- 2. ALL DIMENSIONS SHALL BE CONFIRMED ON SITES

APPROVED BY

CHECKED BY



REGIONAL_PROJECT_MANAGER_AREA

CHECKED BY

DATE	REVISION	SIGN

THIS DOCUMENT AND ALL MATERIAL CONTAINED HEREIN IS PROTECTED BY COPYRIGHT, TRADEMARKS AND OTHER RIGHTS WHICH ARE OWNED AND/OR CONTROLLED BY PT INDOSAT AND/OR ITS AFFILIATES OR BY OTHER PARTIES THAT HAVE LICENSED THEIR MATERIAL TO ITS AFFILIATES


PROJECT NAME

DRAWING TITLE

SITE NAME	WARGALUYU_ARJASARI
SITE ID	ZBDG_6380
SCALE	
DRAWING BY	
CHECKED BY	
VERIFIED BY	
CONTRACT NO	
PROJECT NO	


DRAWING NUMBER	TOTAL DRAWING
----------------	---------------

PAGE NUMBER	TOTAL PAGE
-------------	------------

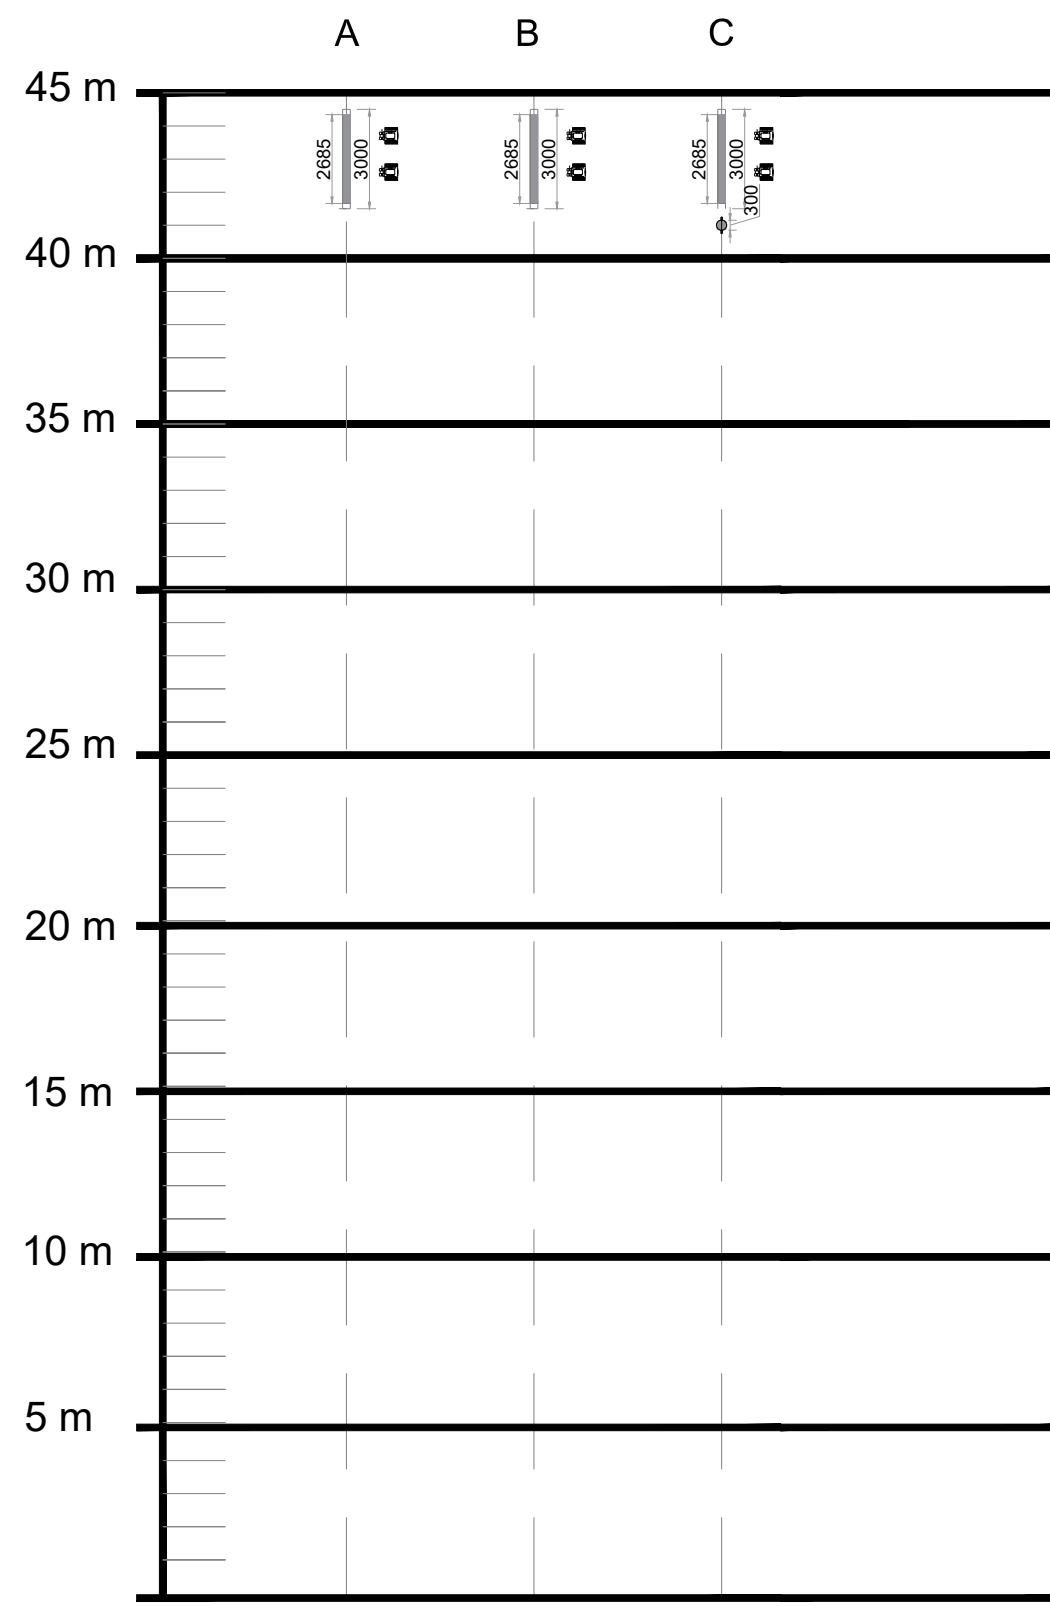

TOWER LEG ID
(CLOCKWISE FROM NORTH DIRECTION)

COLOR LEGENDS

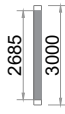

EXISTING RF ANTENNA SF (ex-IO)



EXISTING RRU SF



EXISTING MW ANTENNA SF 0.3Ø (ex-IO)

REMARKS

1. ALL DIMENSIONS ARE IN MILIMETER UNLESS NOTED ON THE DRAWING

2. ALL DIMENSIONS SHALL BE CONFIRMED ON SITES

APPROVED BY

CHECKED BY

 PT. HUAWEI TECH INVESTMENT

REGIONAL_PROJECT_MANAGER_AREA

CHECKED BY

DATE	REVISION	SIGN


THIS DOCUMENT AND ALL MATERIAL CONTAINED HEREIN IS PROTECTED BY COPYRIGHT, TRADEMARKS AND OTHER RIGHTS WHICH ARE OWNED AND/OR CONTROLLED BY PT INDOSAT AND/OR ITS AFFILIATES OR BY OTHER PARTIES THAT HAVE LICENSED THEIR MATERIAL TO ITS AFFILIATES

PROJECT NAME

DRAWING TITLE

SITE NAME	WARGALUYU_ARJASARI
SITE ID	ZBDG_6380
SCALE	
DRAWING BY	
CHECKED BY	
VERIFIED BY	
CONTRACT NO	
PROJECT NO	

DRAWING NUMBER	TOTAL DRAWING
PAGE NUMBER	TOTAL PAGE

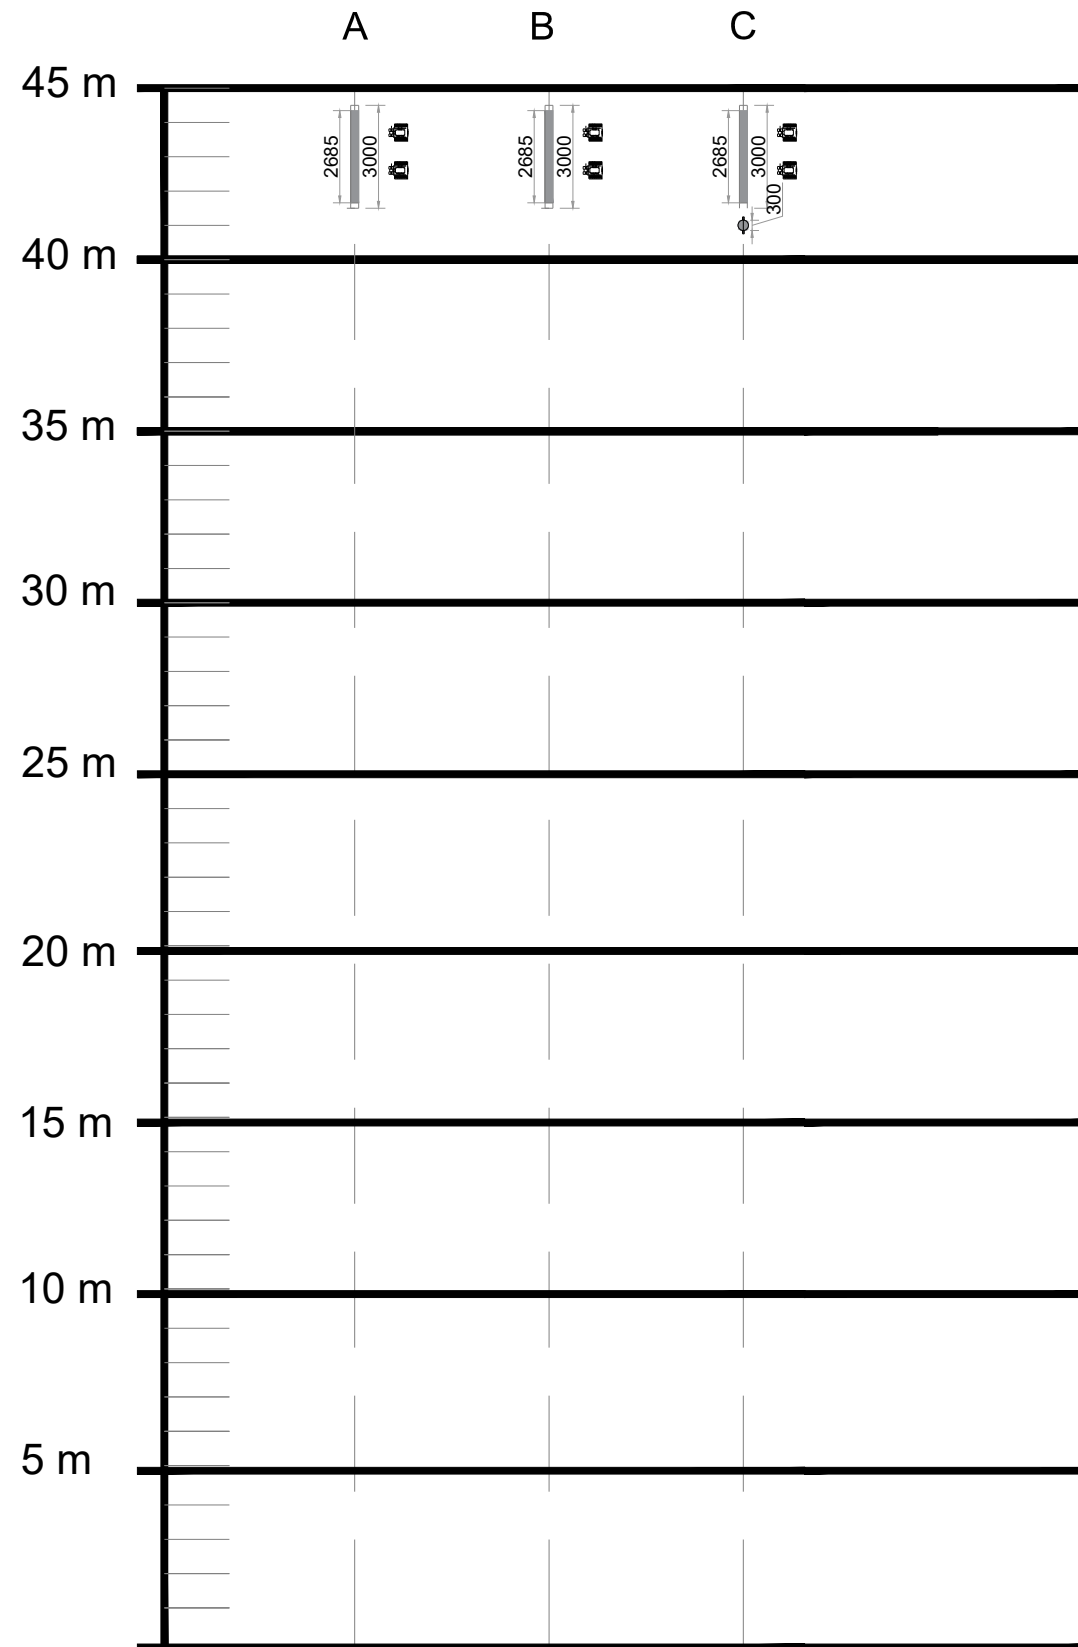

SST 3 LEG 45 METER

TOWER LEG ID
(CLOCKWISE FROM NORTH DIRECTION)

COLOR LEGENDS

EXISTING RF ANTENNA SF (ex-IO)

EXISTING RRU SF

EXISTING MW ANTENNA SF 0.3Ø (ex-IO)

REMARKS

1. ALL DIMENSIONS ARE IN MILIMETER UNLESS NOTED ON THE DRAWING

2. ALL DIMENSIONS SHALL BE CONFIRMED ON SITES

APPROVED BY

CHECKED BY

PT. HUAWEI TECH INVESTMENT

REGIONAL_PROJECT_MANAGER_AREA

CHECKED BY

DATE	REVISION	SIGN

THIS DOCUMENT AND ALL MATERIAL CONTAINED HEREIN IS PROTECTED BY COPYRIGHT, TRADEMARKS AND OTHER RIGHTS WHICH ARE OWNED AND/OR CONTROLLED BY PT INDOSAT AND/OR ITS AFFILIATES OR BY OTHER PARTIES THAT HAVE LICENSED THEIR MATERIAL TO ITS AFFILIATES

PROJECT NAME

DRAWING TITLE

SITE NAME	WARGALUYU_ARJASARI
SITE ID	ZBDG_6380
SCALE	
DRAWING BY	
CHECKED BY	
VERIFIED BY	
CONTRACT NO	
PROJECT NO	
DRAWING NUMBER	TOTAL DRAWING
PAGE NUMBER	TOTAL PAGE